




CASA DE CULTURA
SLOBOZIA

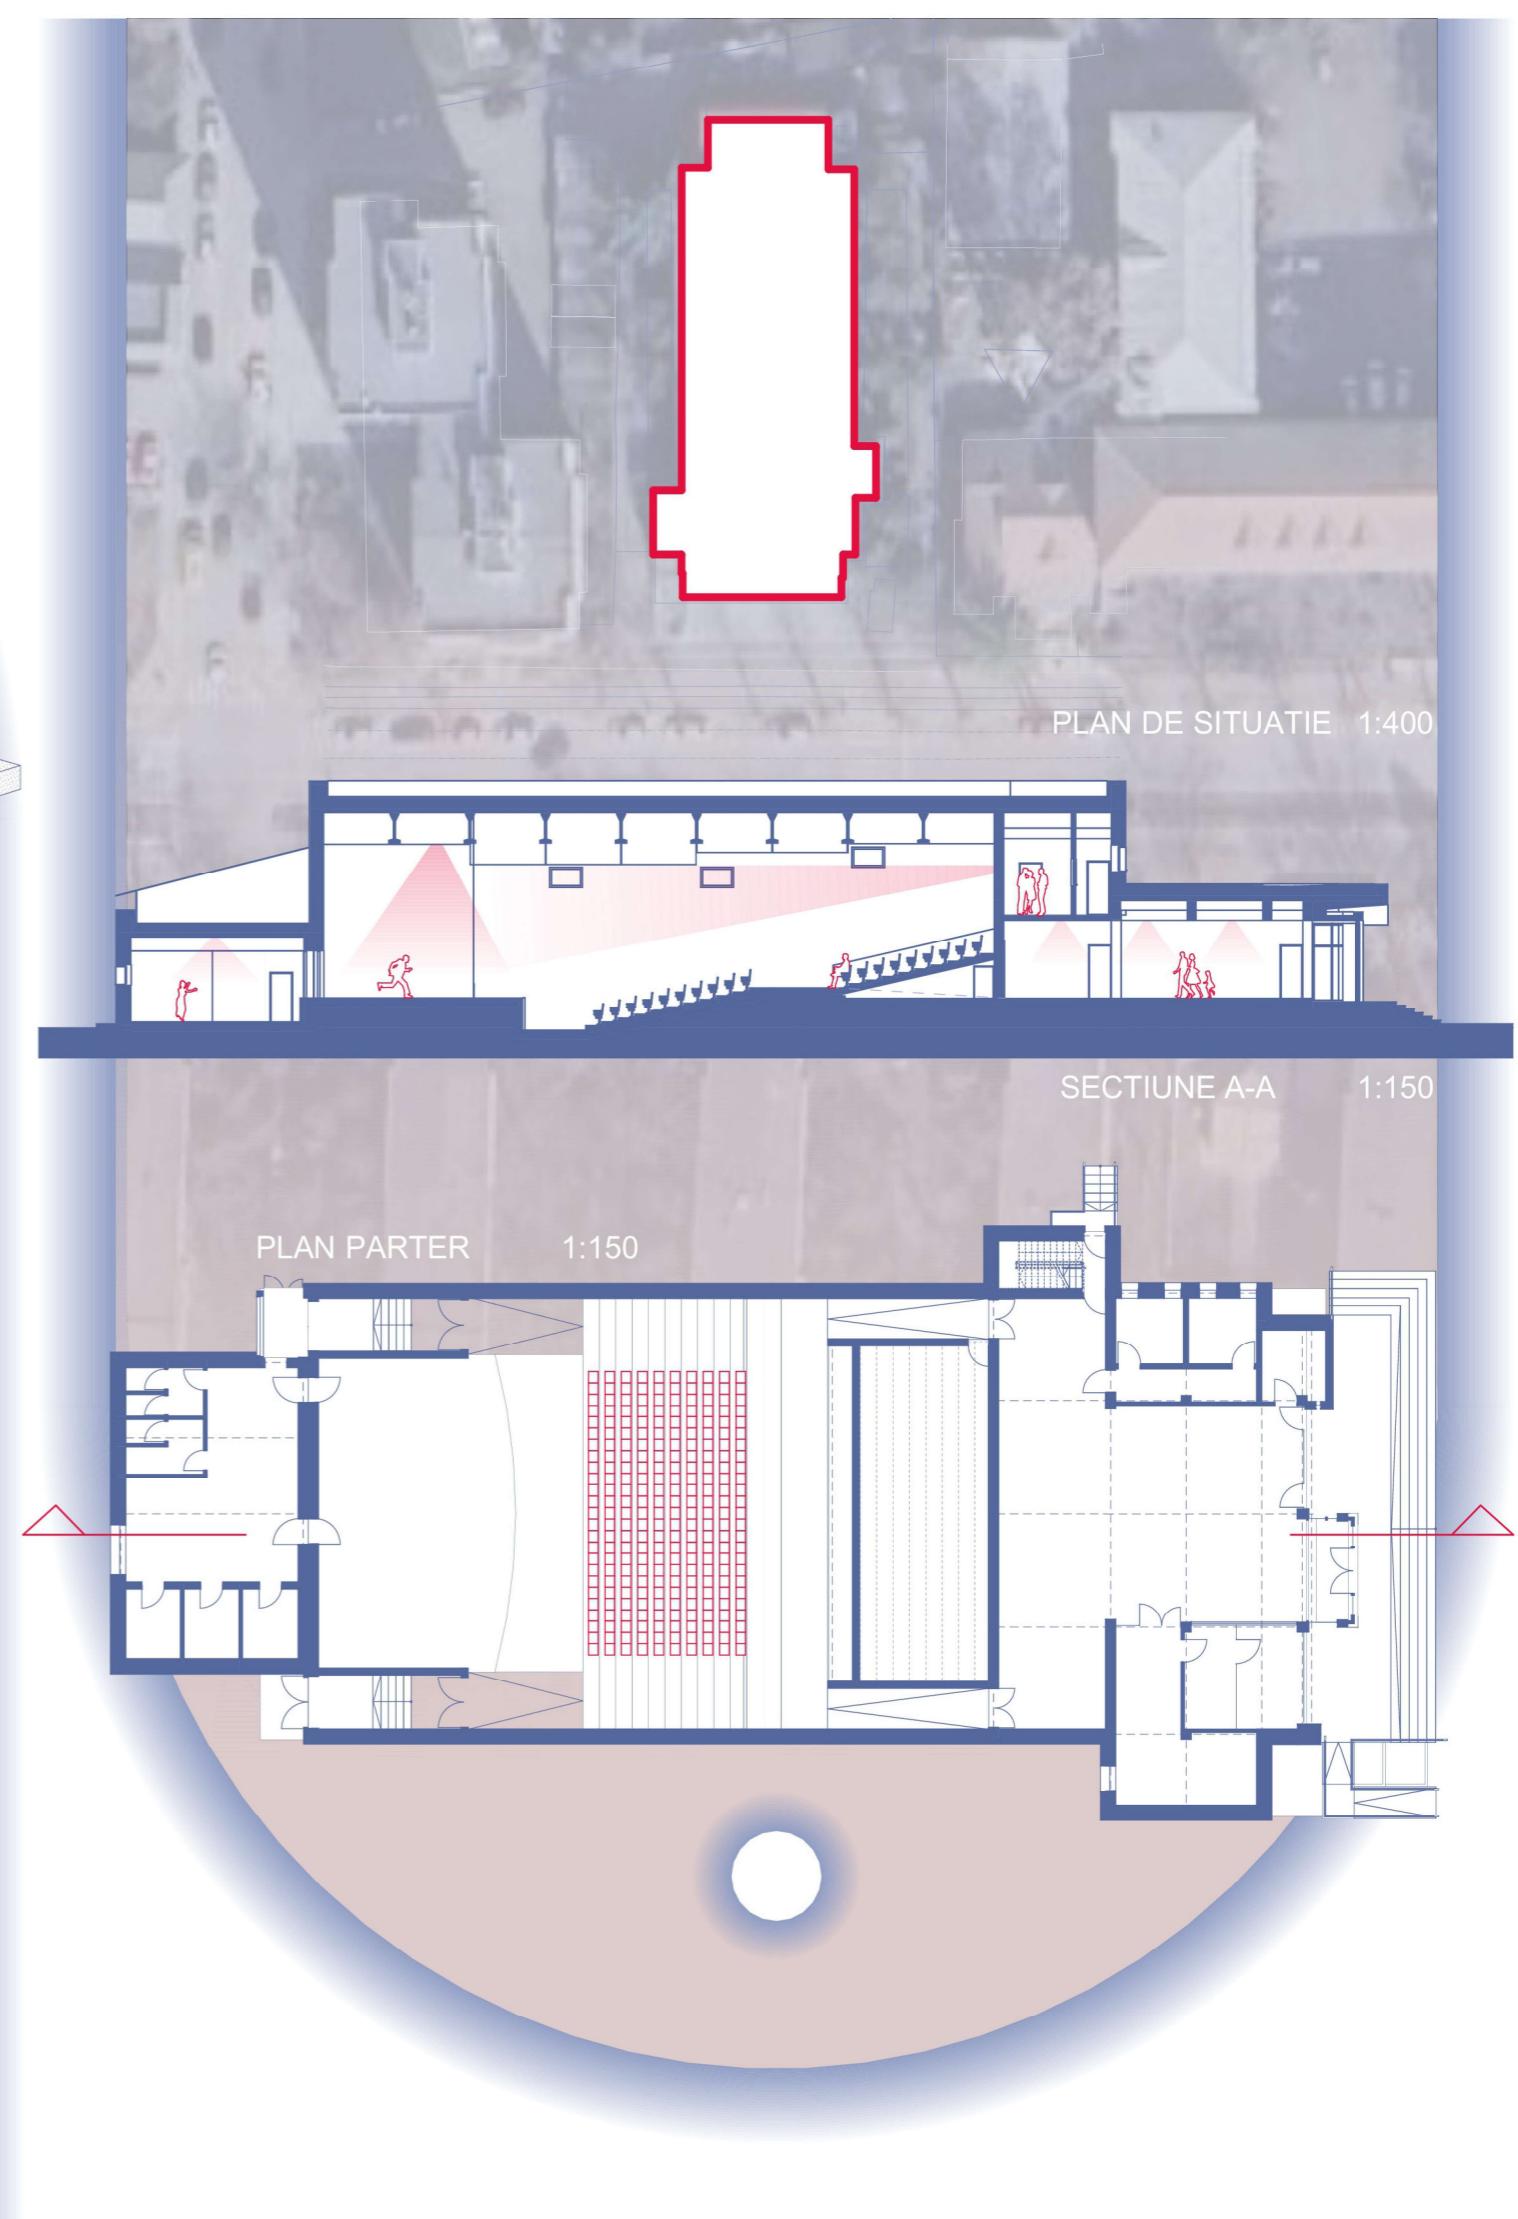


PIATA AGRO-ALIMENTARA
STEFANESTI - BOTOSANI

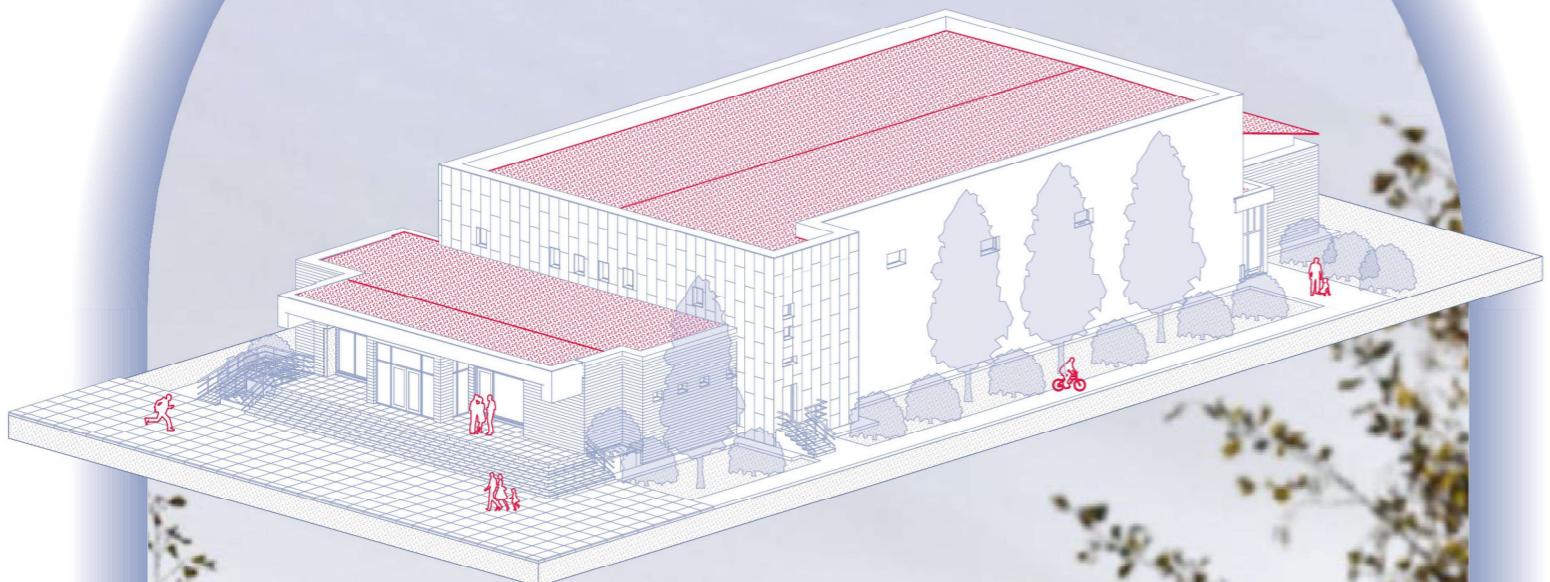


PLAN PARTER 1:150




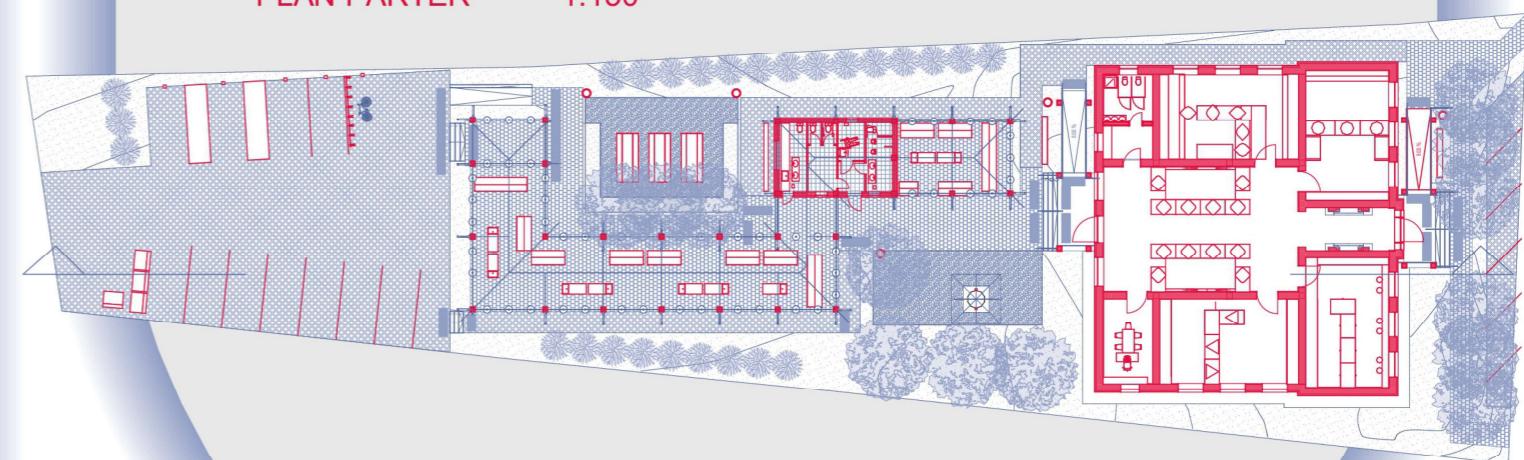


CASA SECUIENI ROMAN

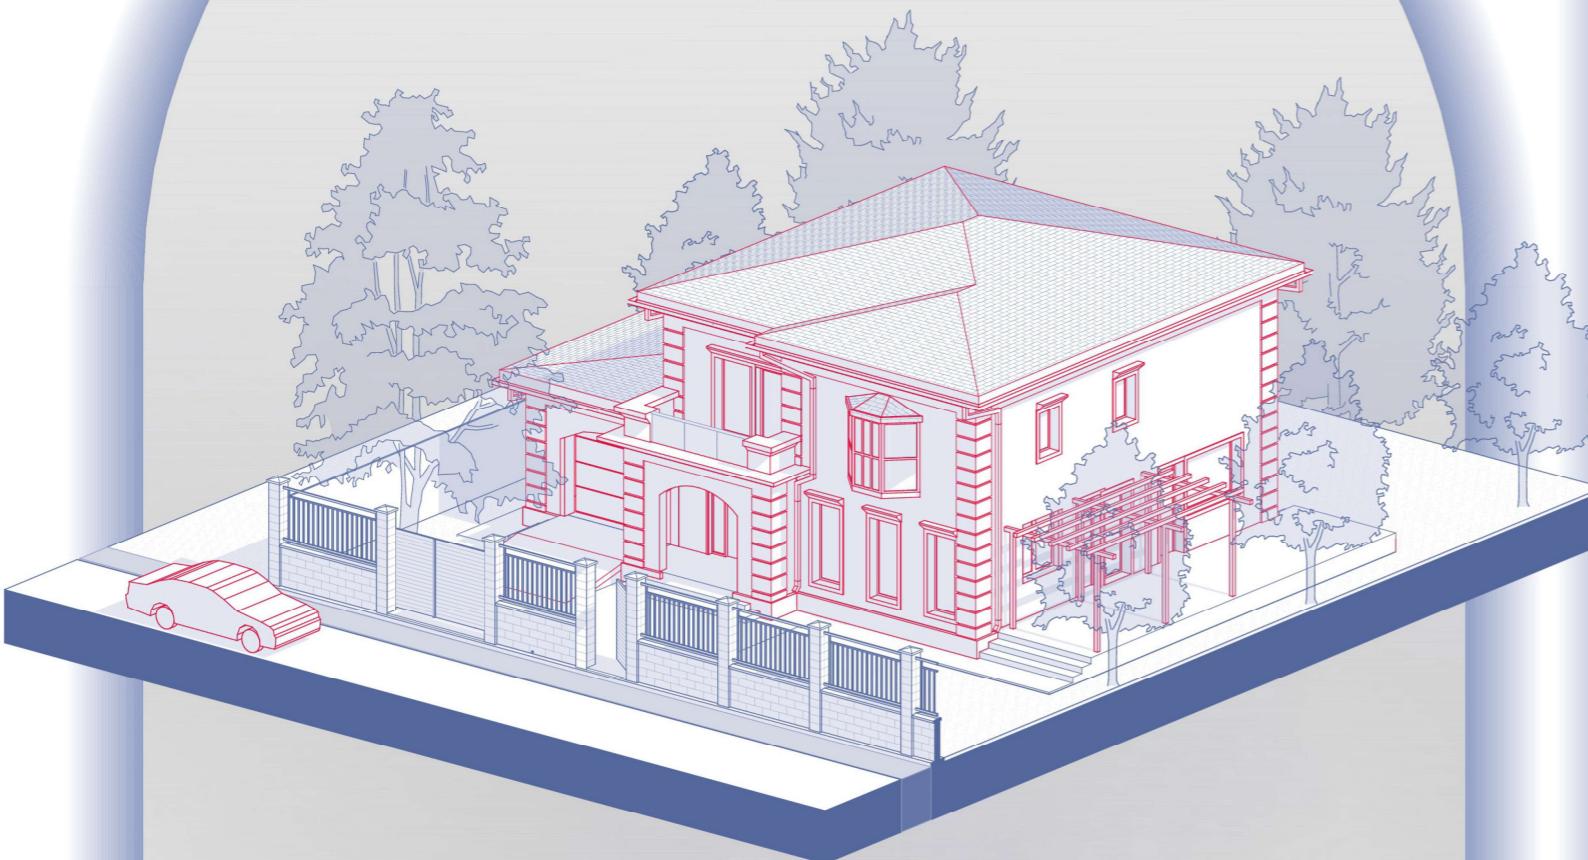

PLAN PARTER

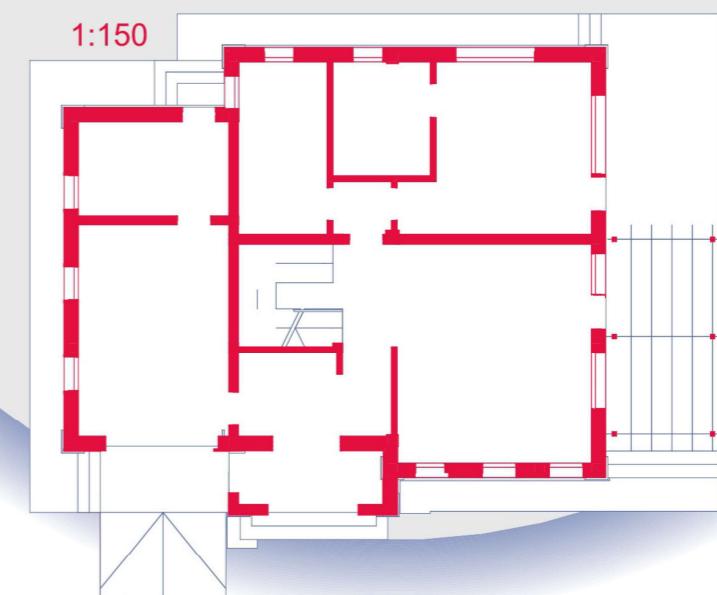


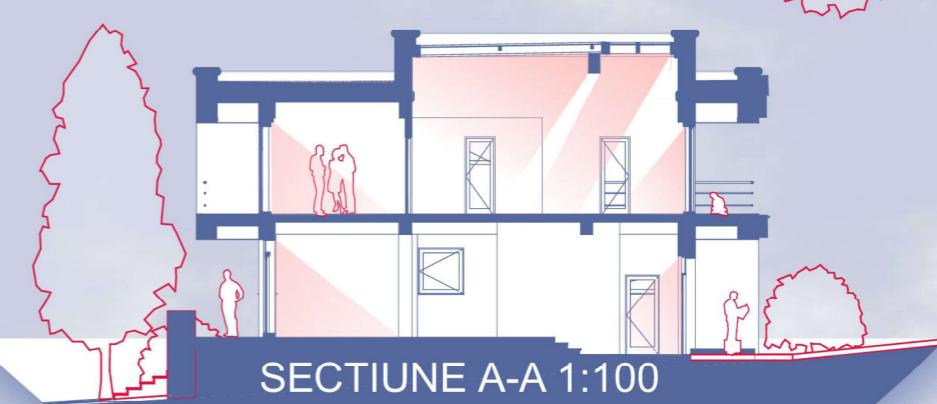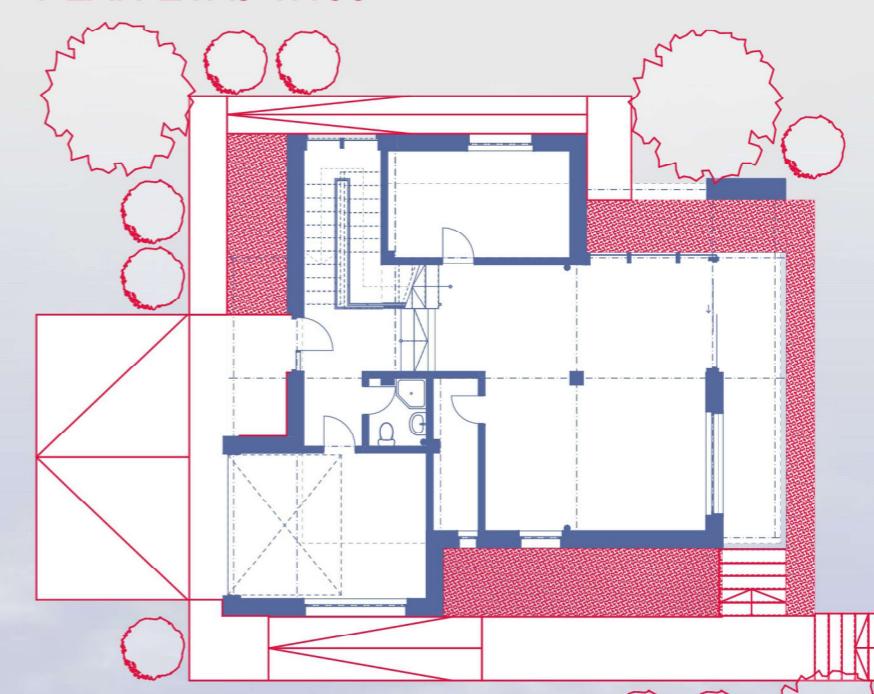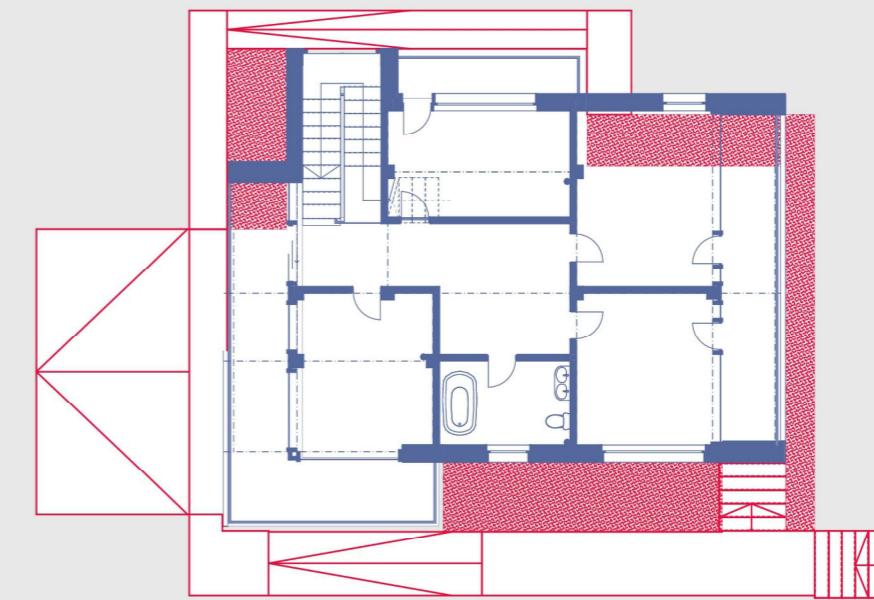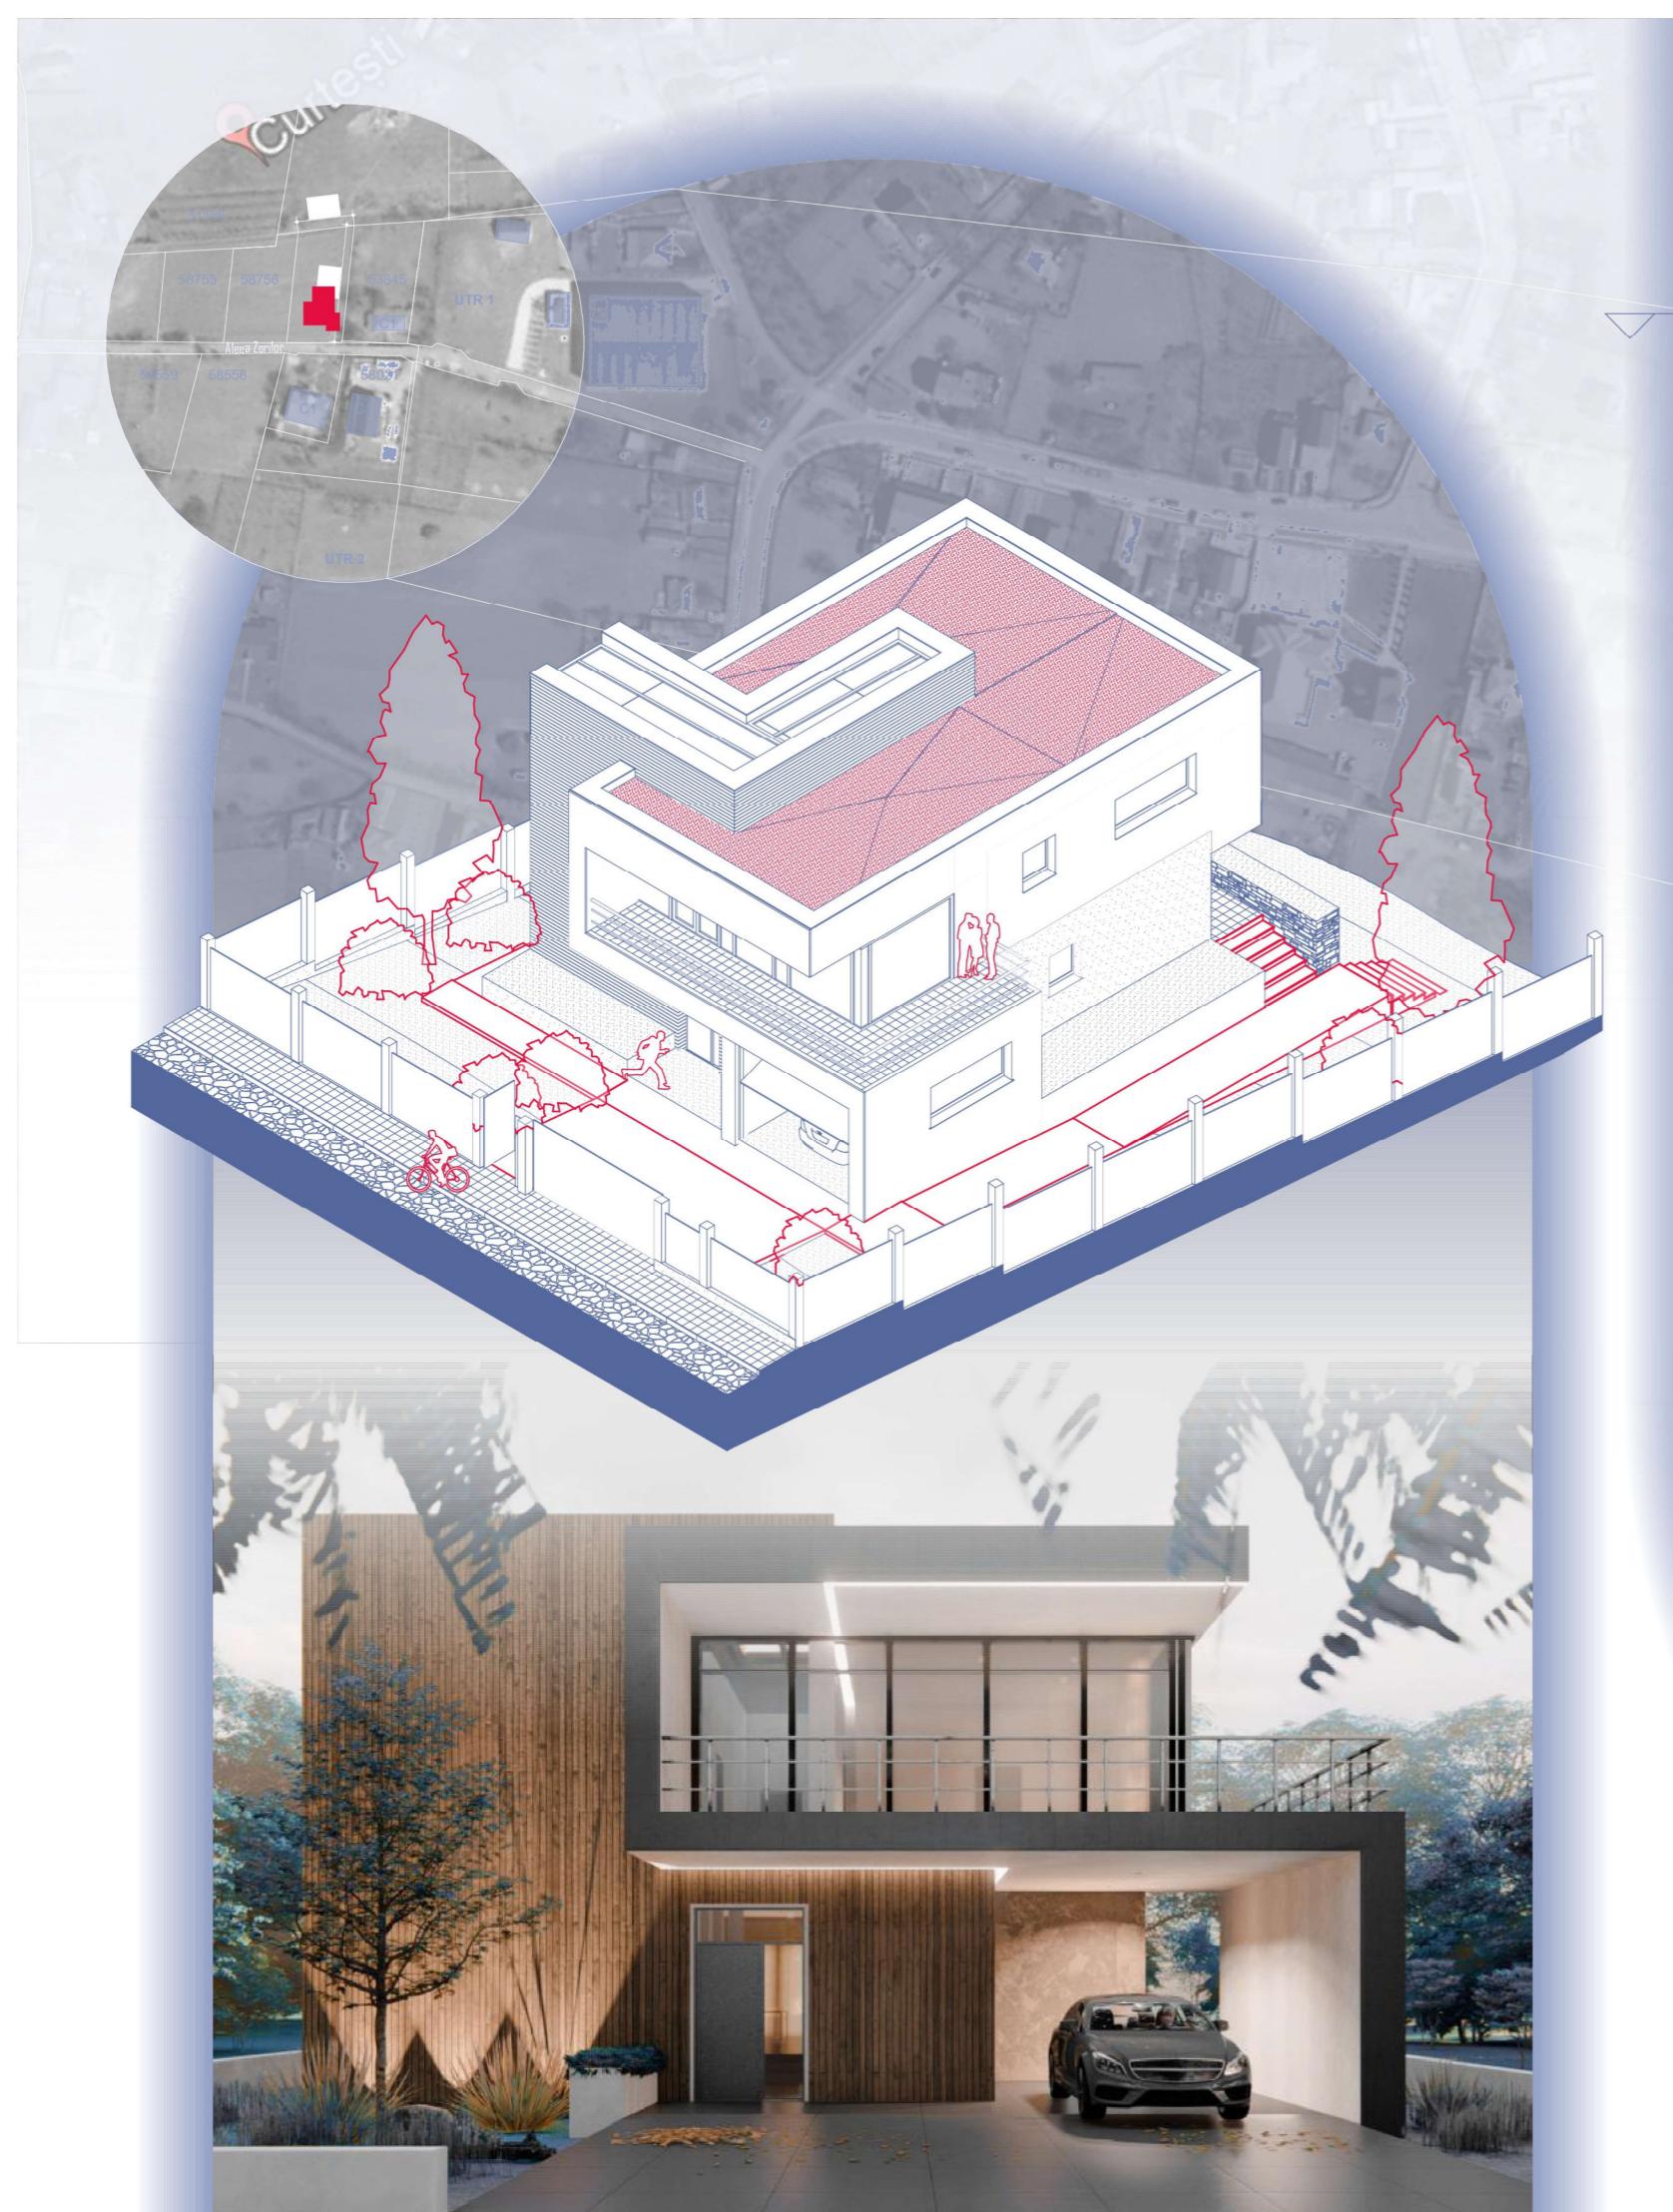


MODUL SCAUN



MODUL BANCA

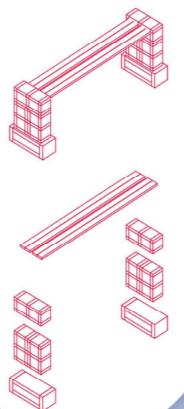





MODUL MASA

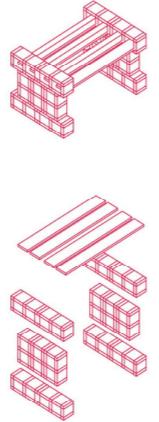


MODUL COS




PARC FONDUL ANTREPRENORILOR LOCALI | IASI

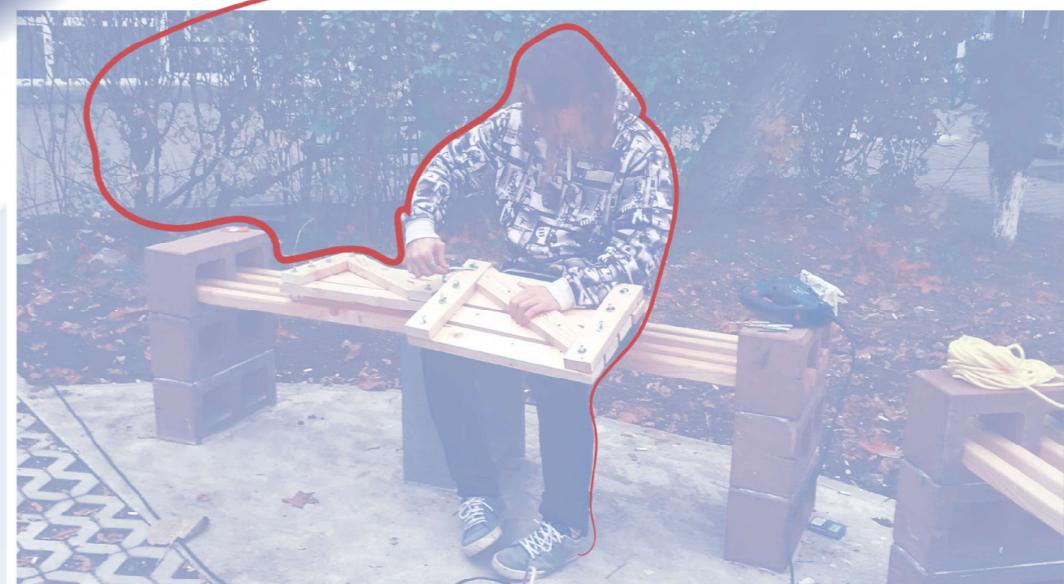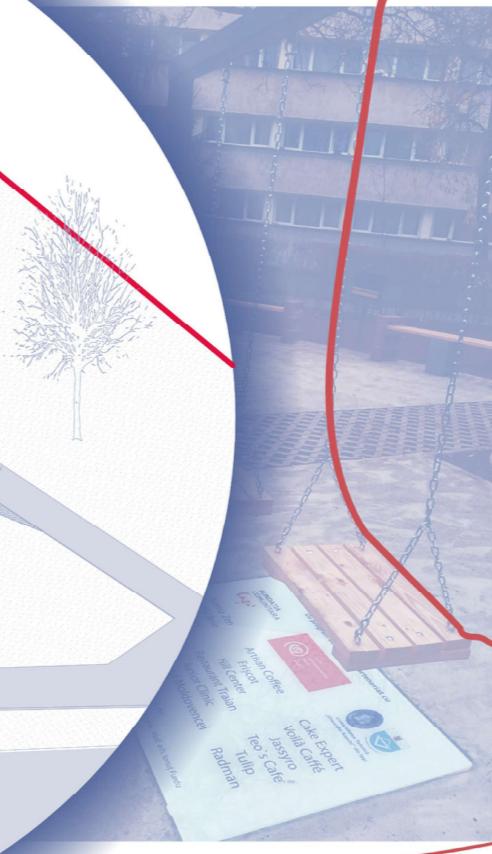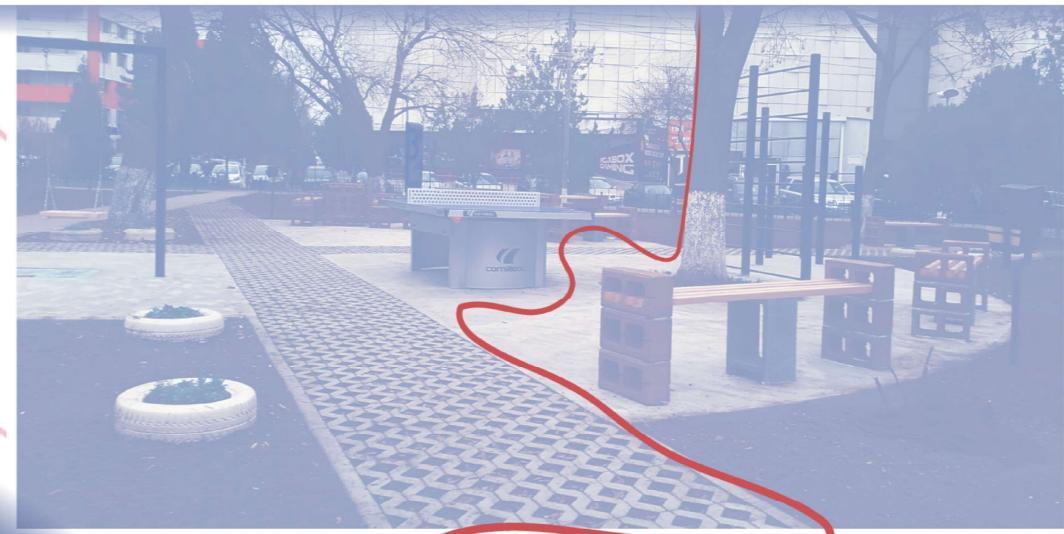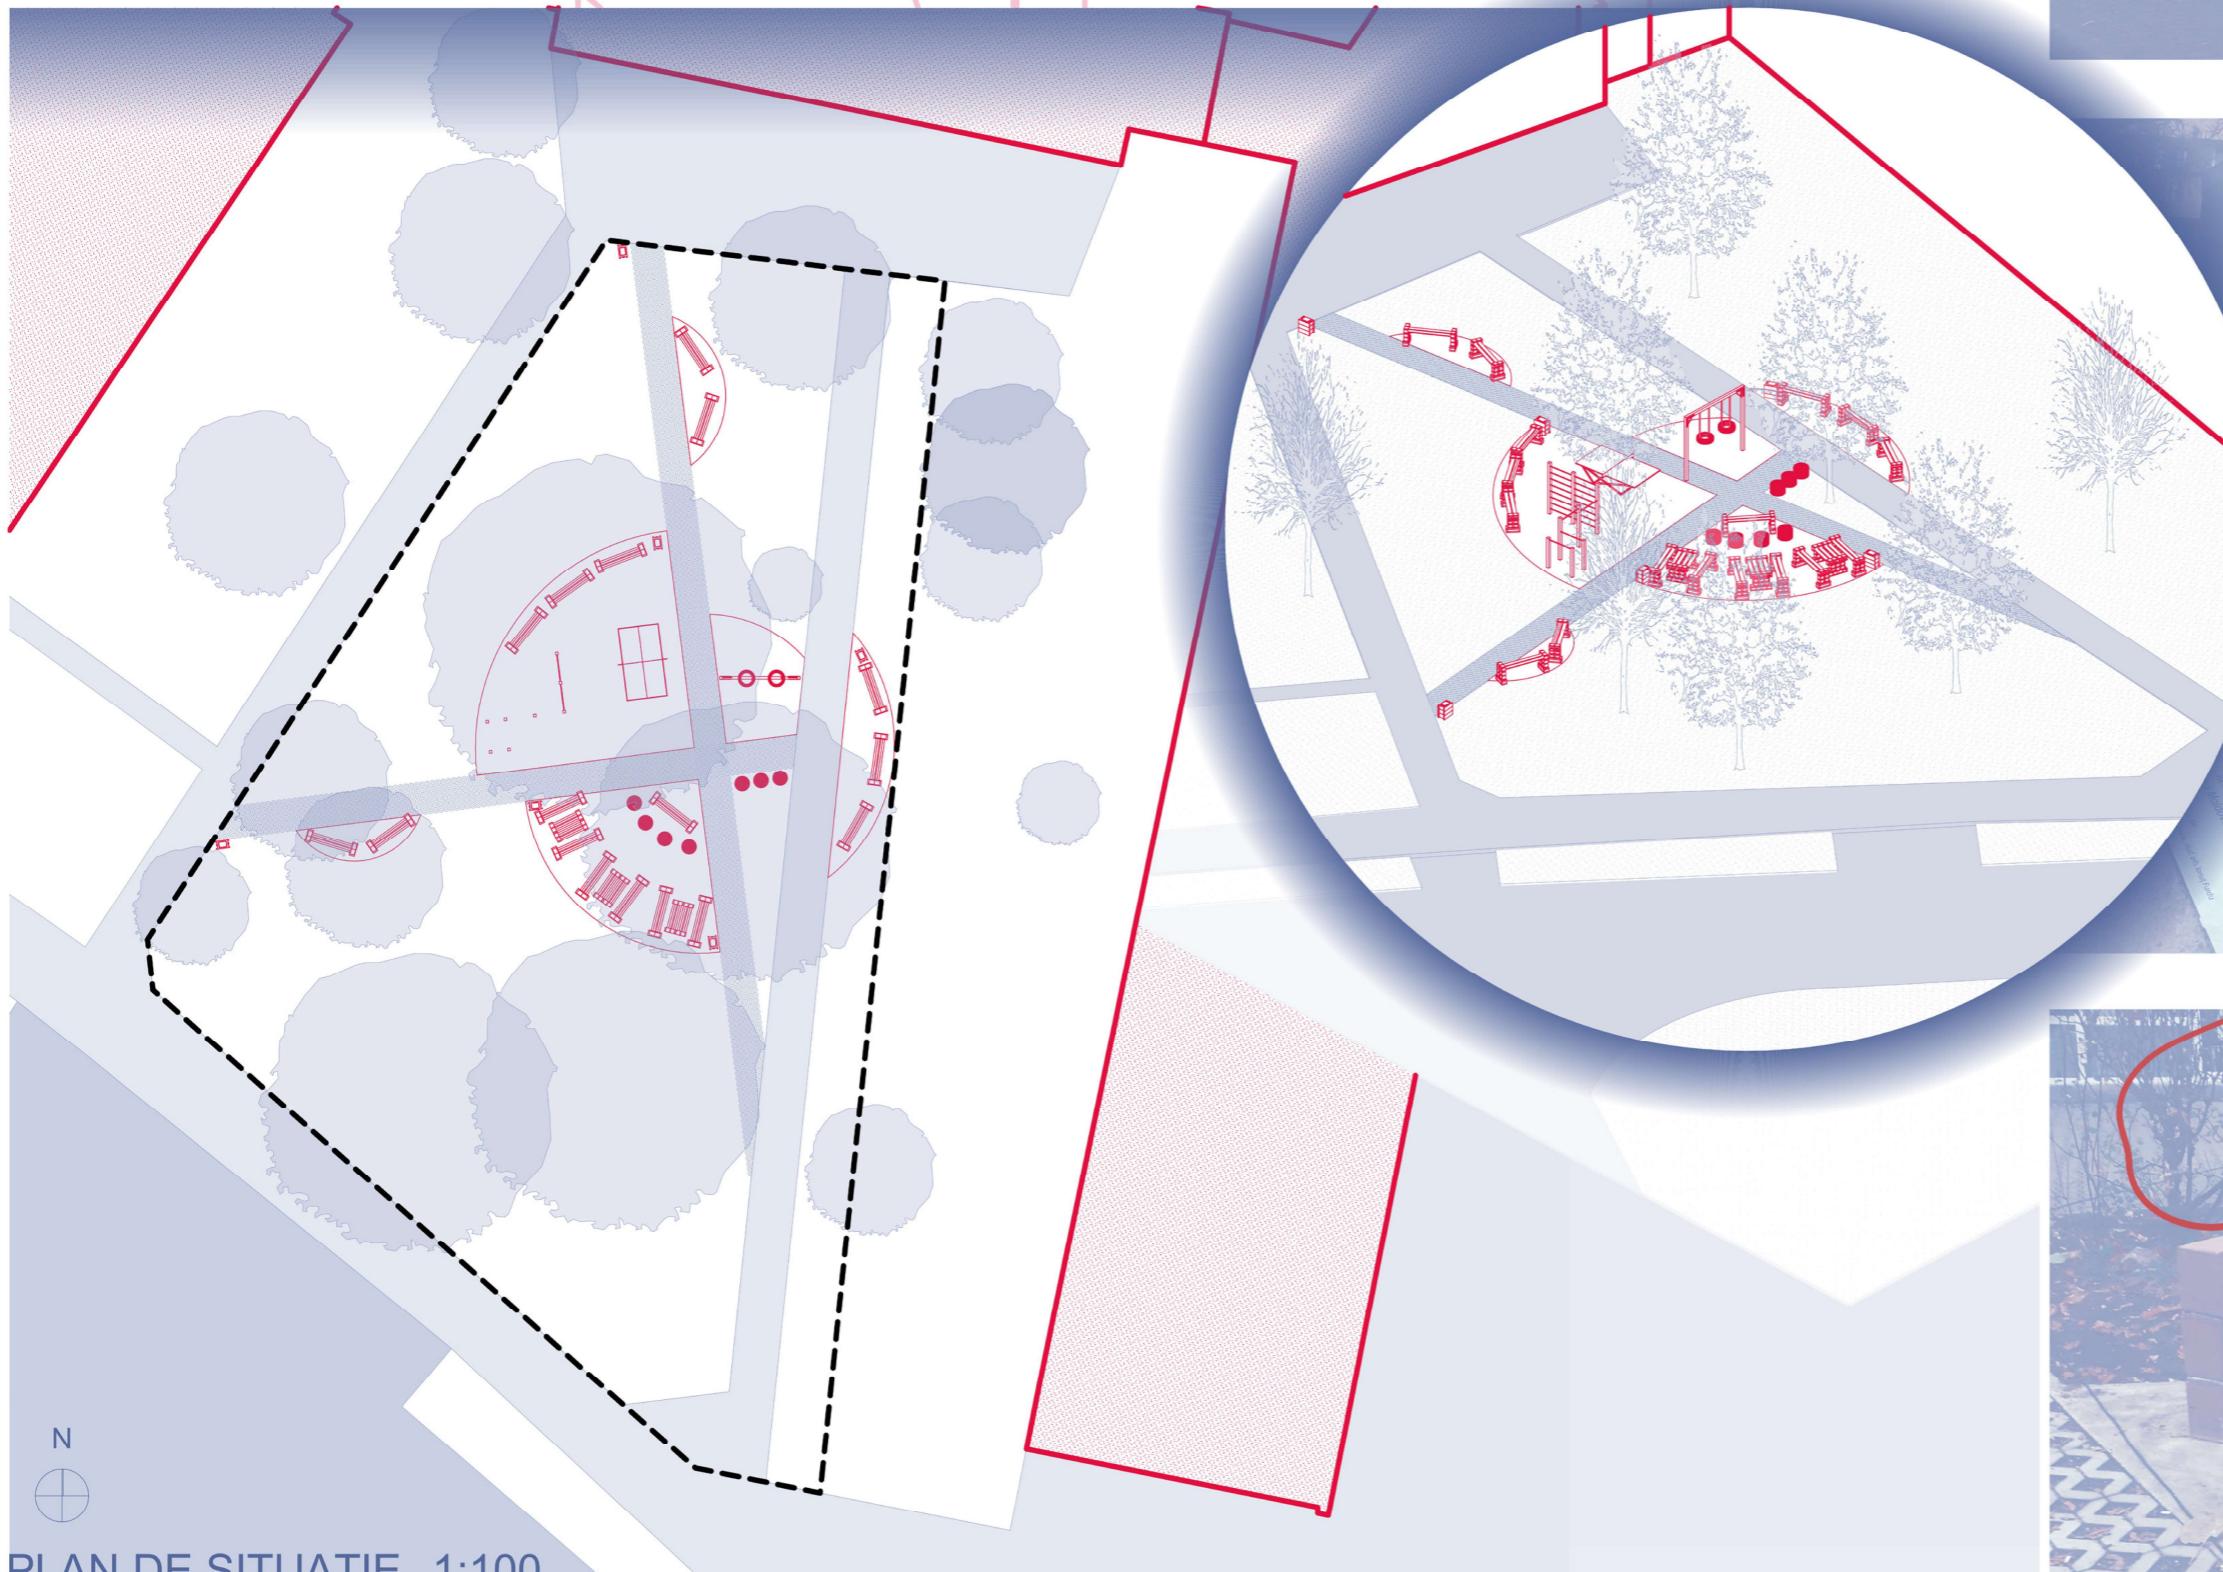


MODUL SCENA

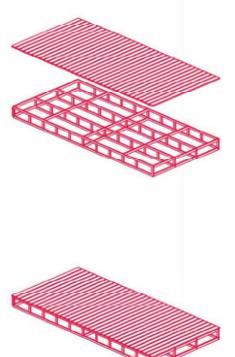





MODUL 1

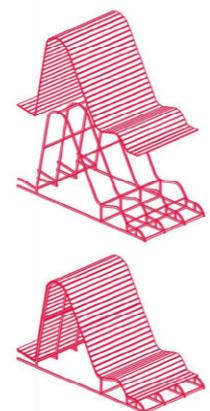

MODUL 2

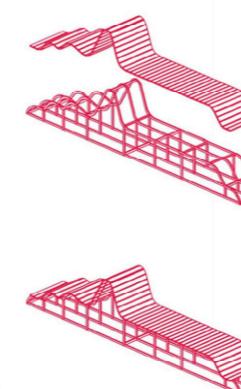

PARC TRANSGOR T10-T11 CAMPUS TUDOR VLADIMIRECU

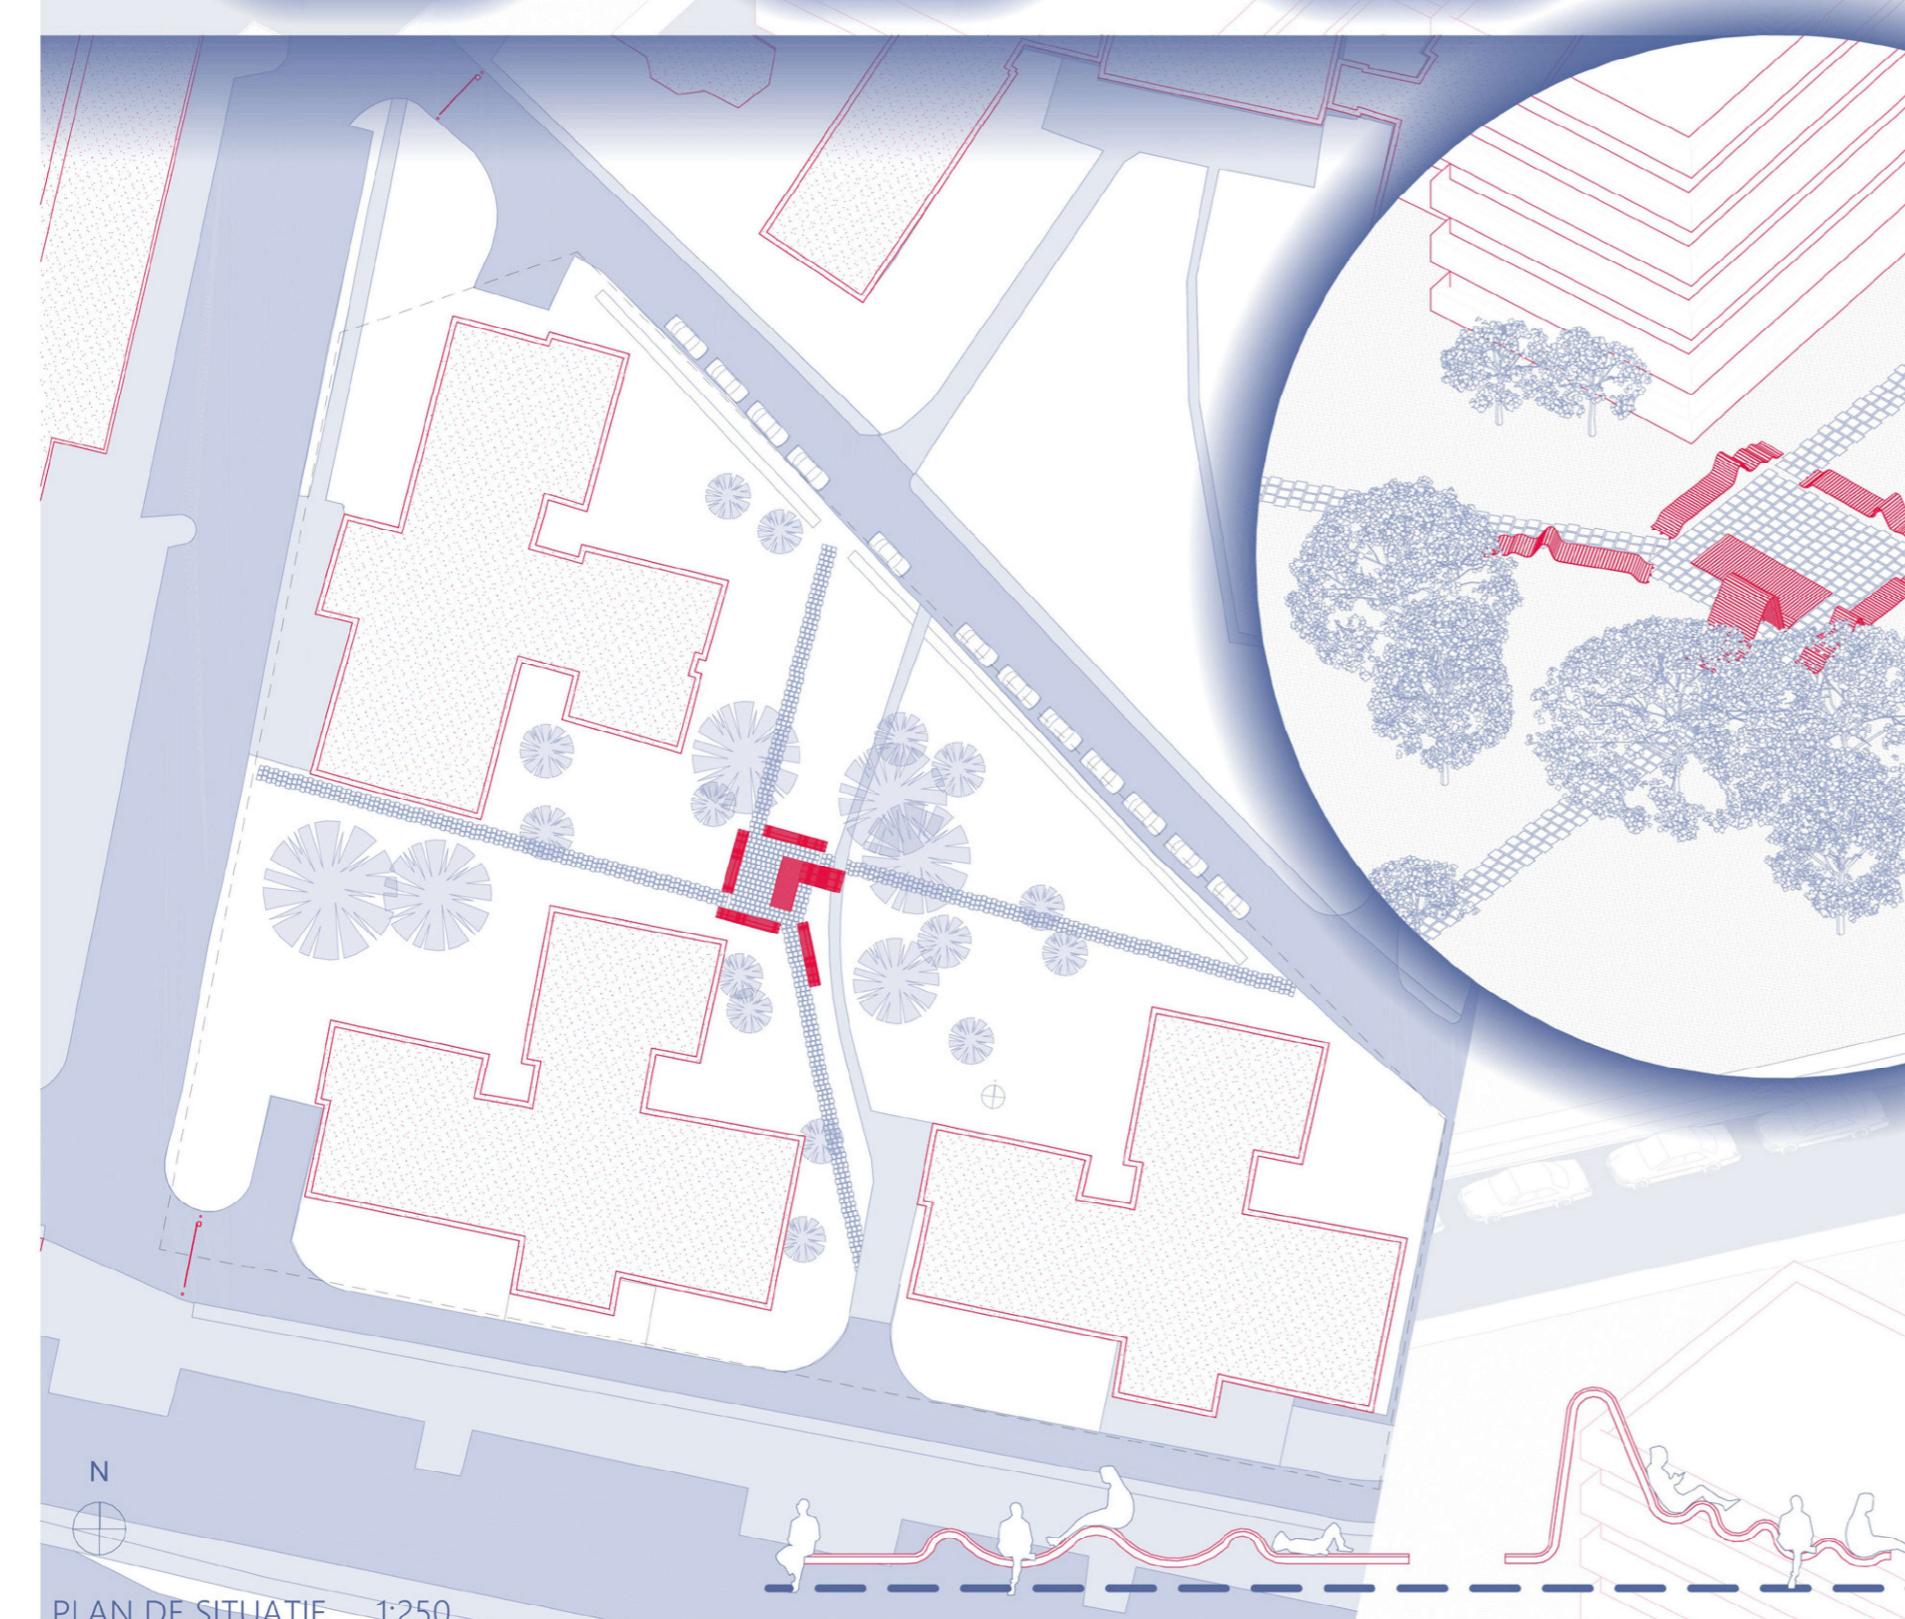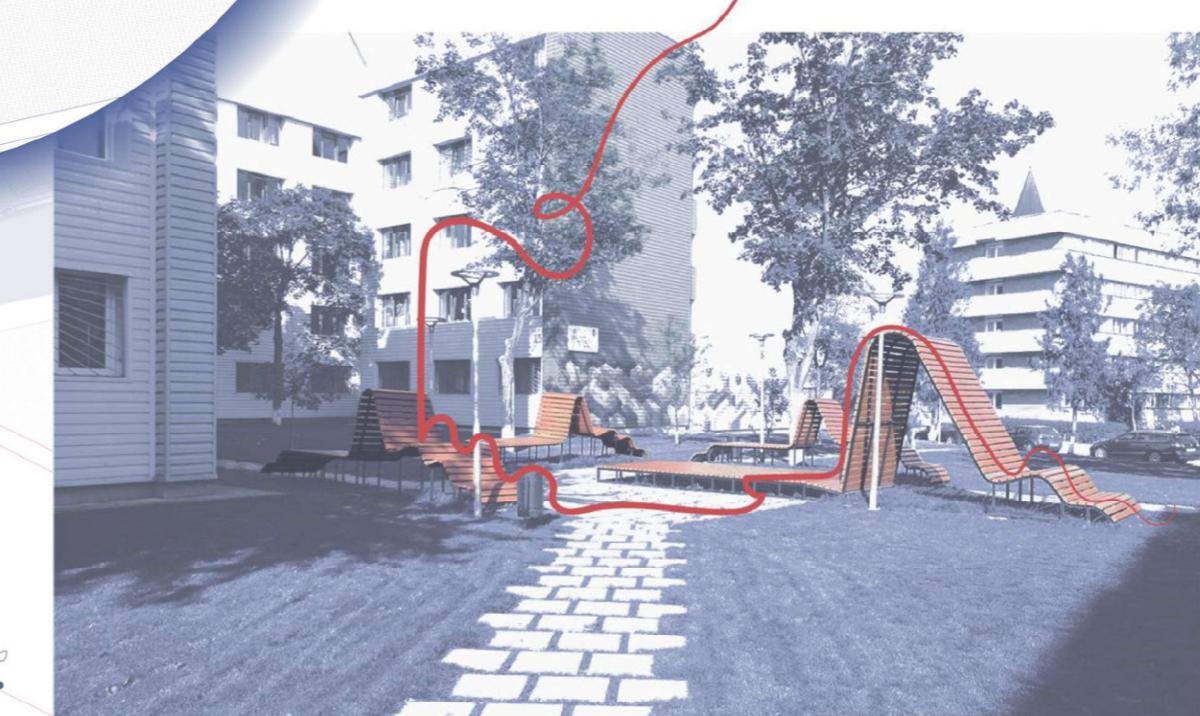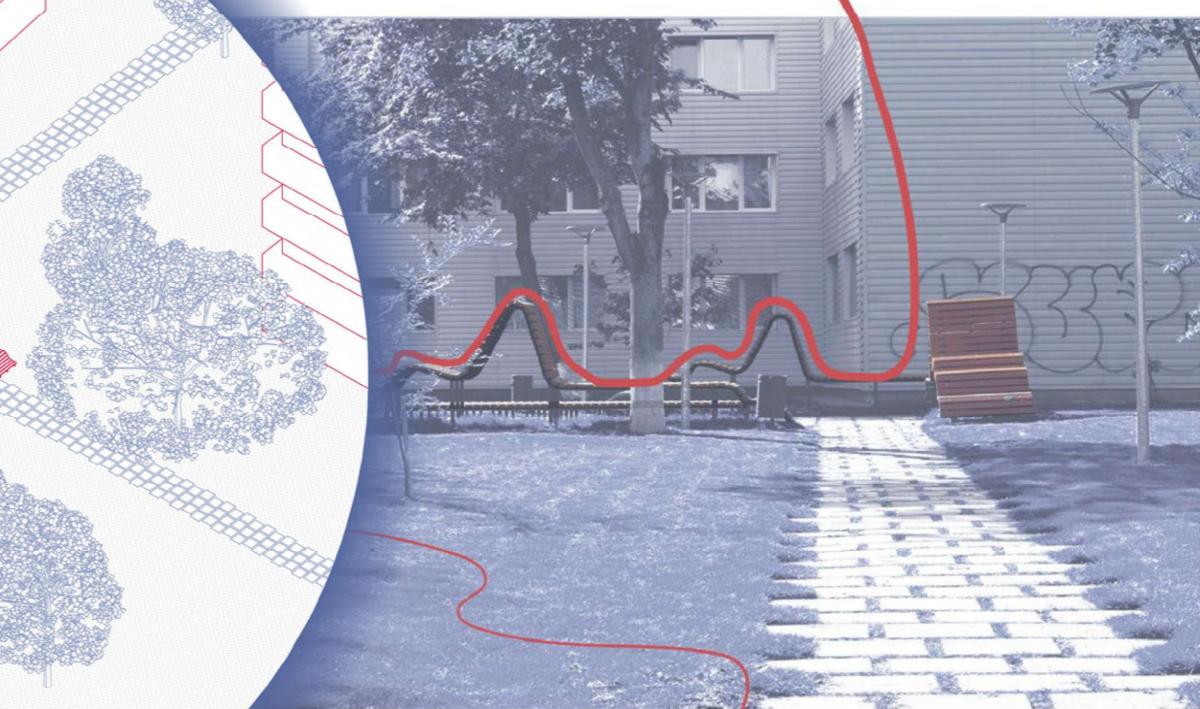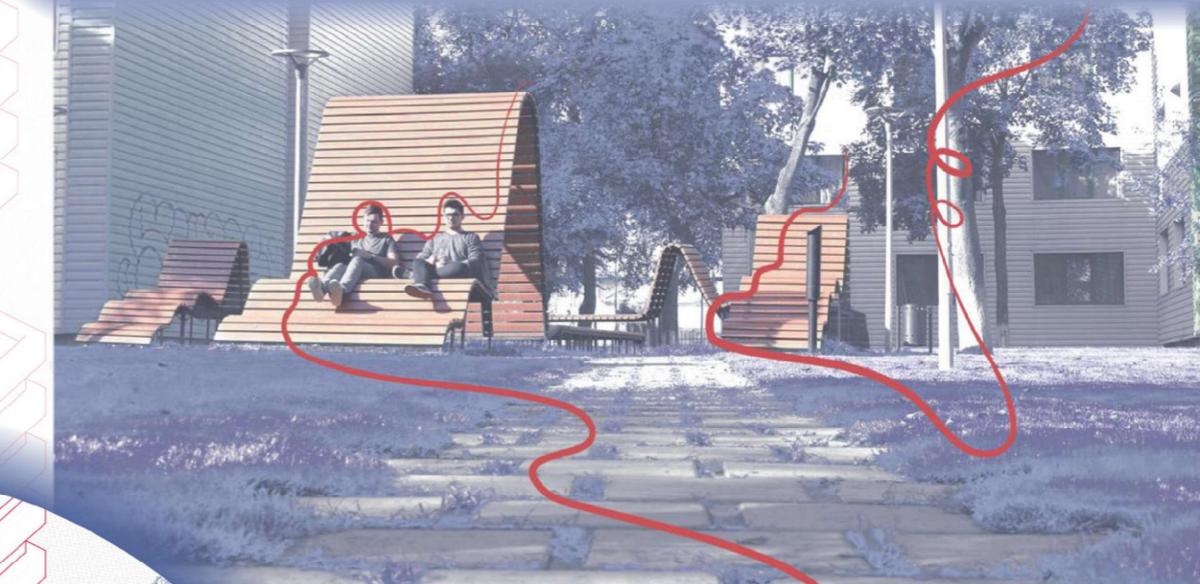

MOBILARE PRIMARIE - OFFICE

