


# CASA BACAU

arh. Mihael - Ionut FURDU




00

## PLAN DE INCADRARE 1:2000

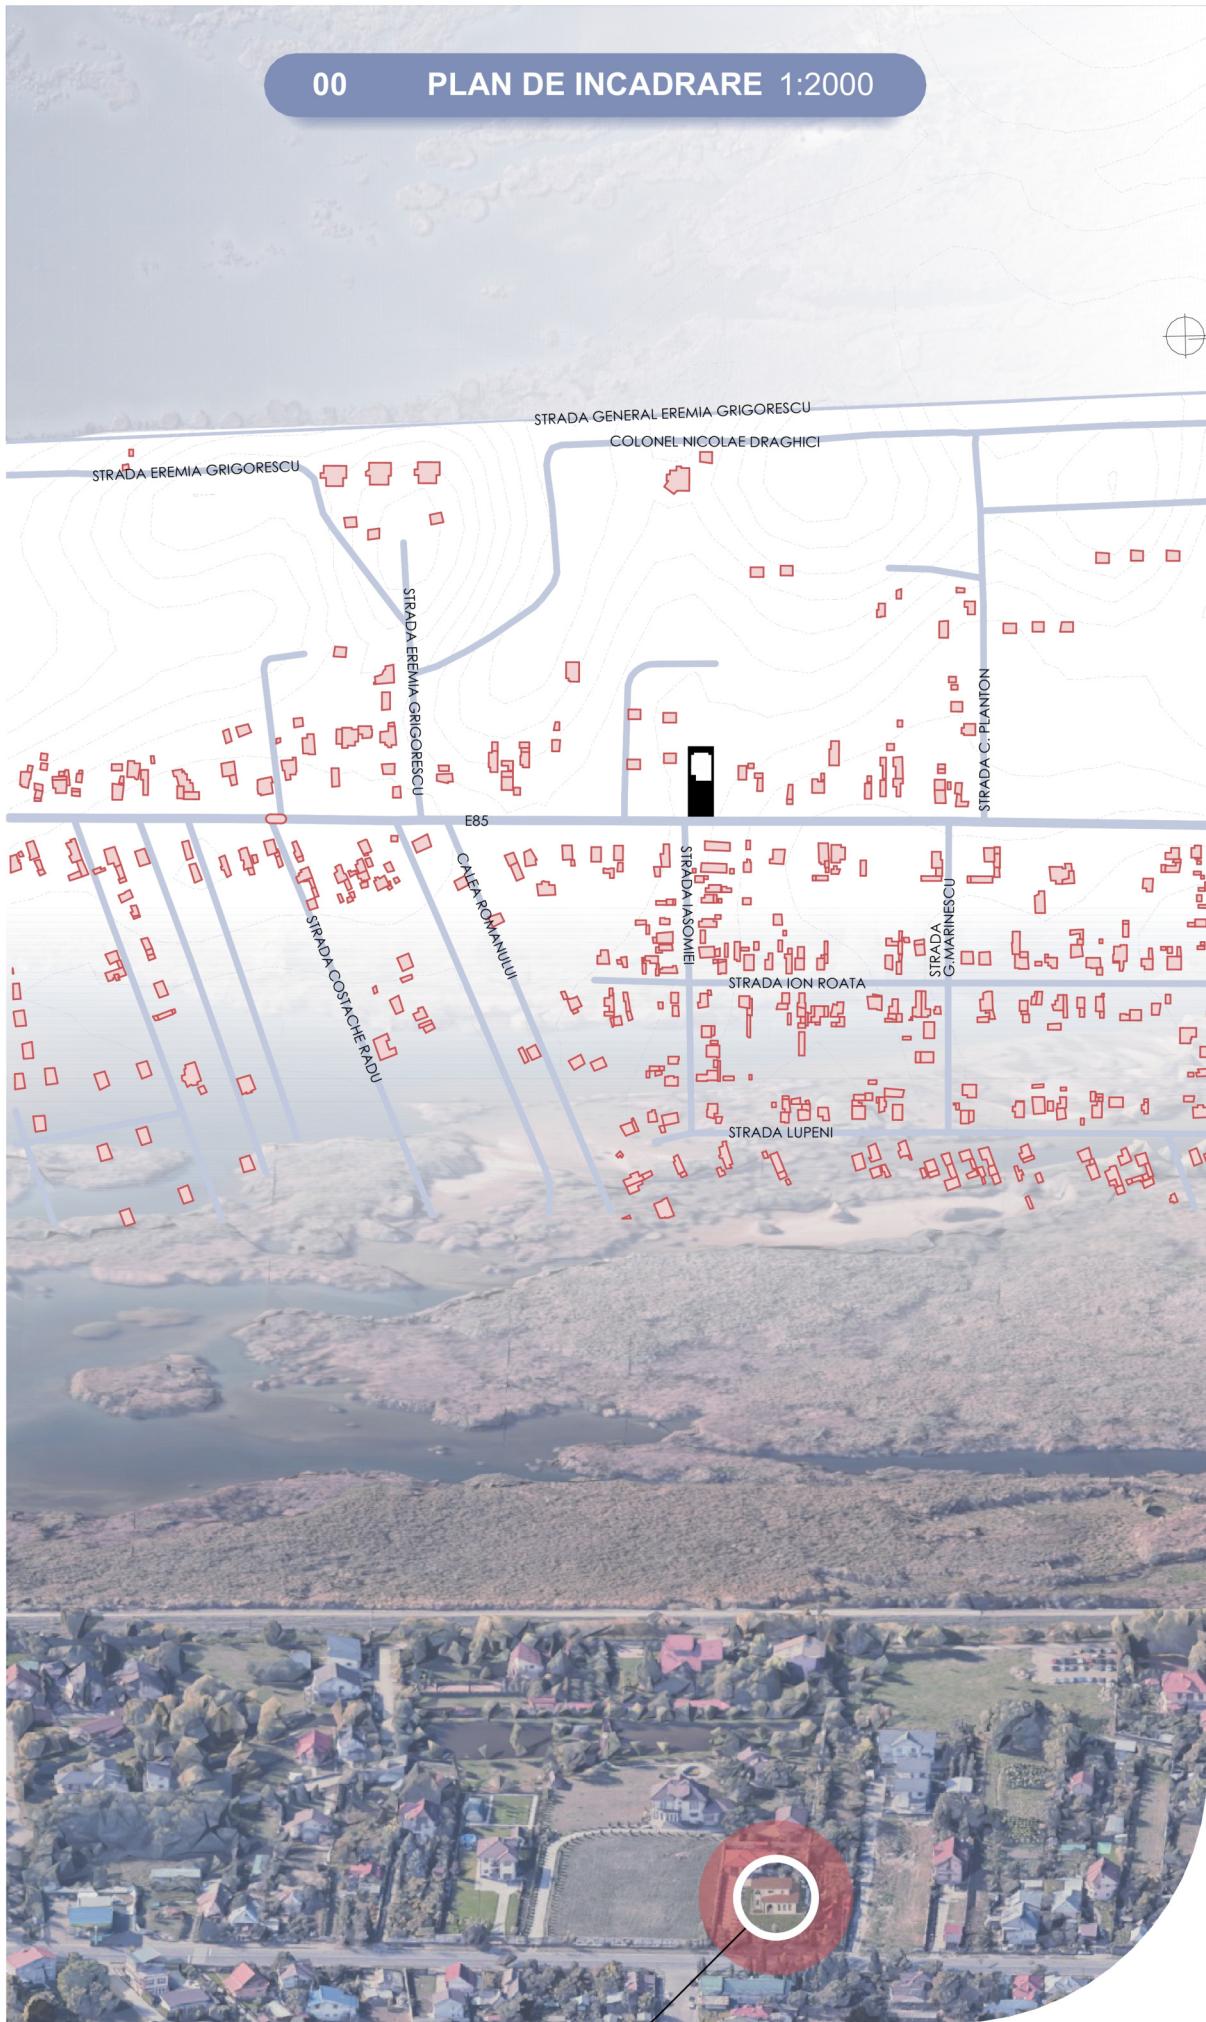


Calea Romanului 210, Bacău 600378

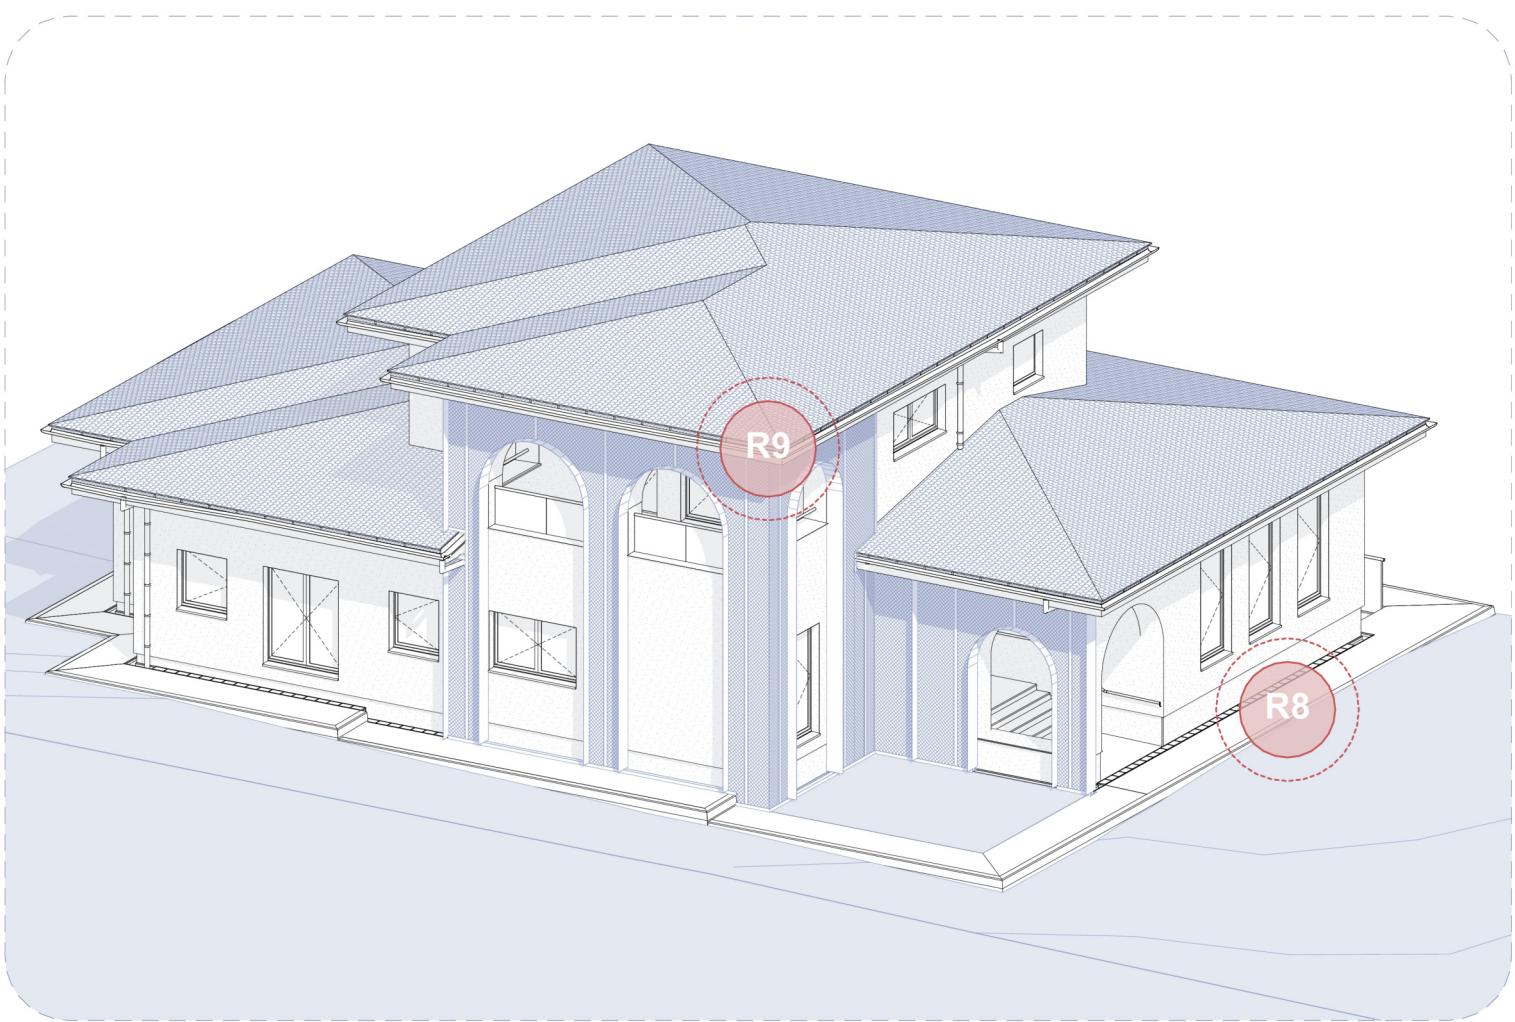


R8 - FATADA INTRARE



R9 - PERETE VERDE

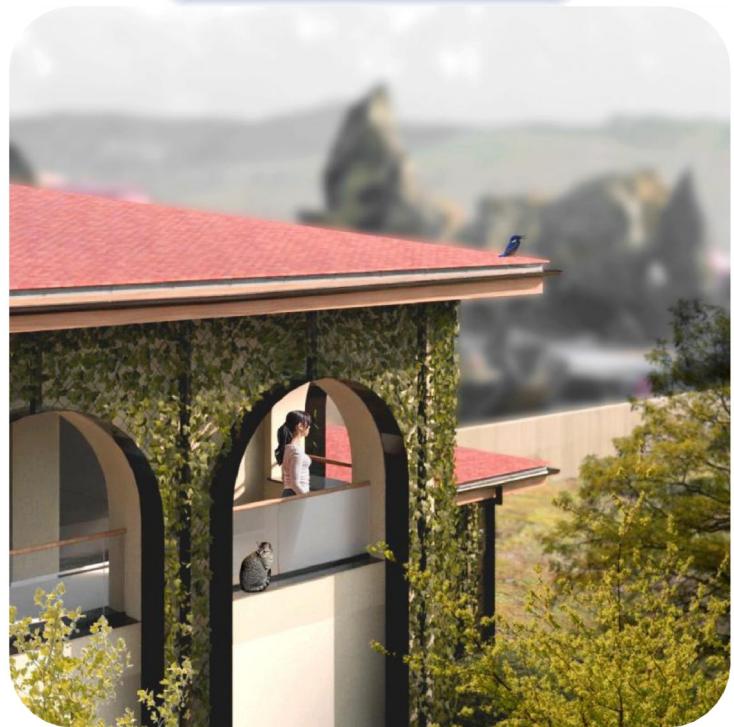

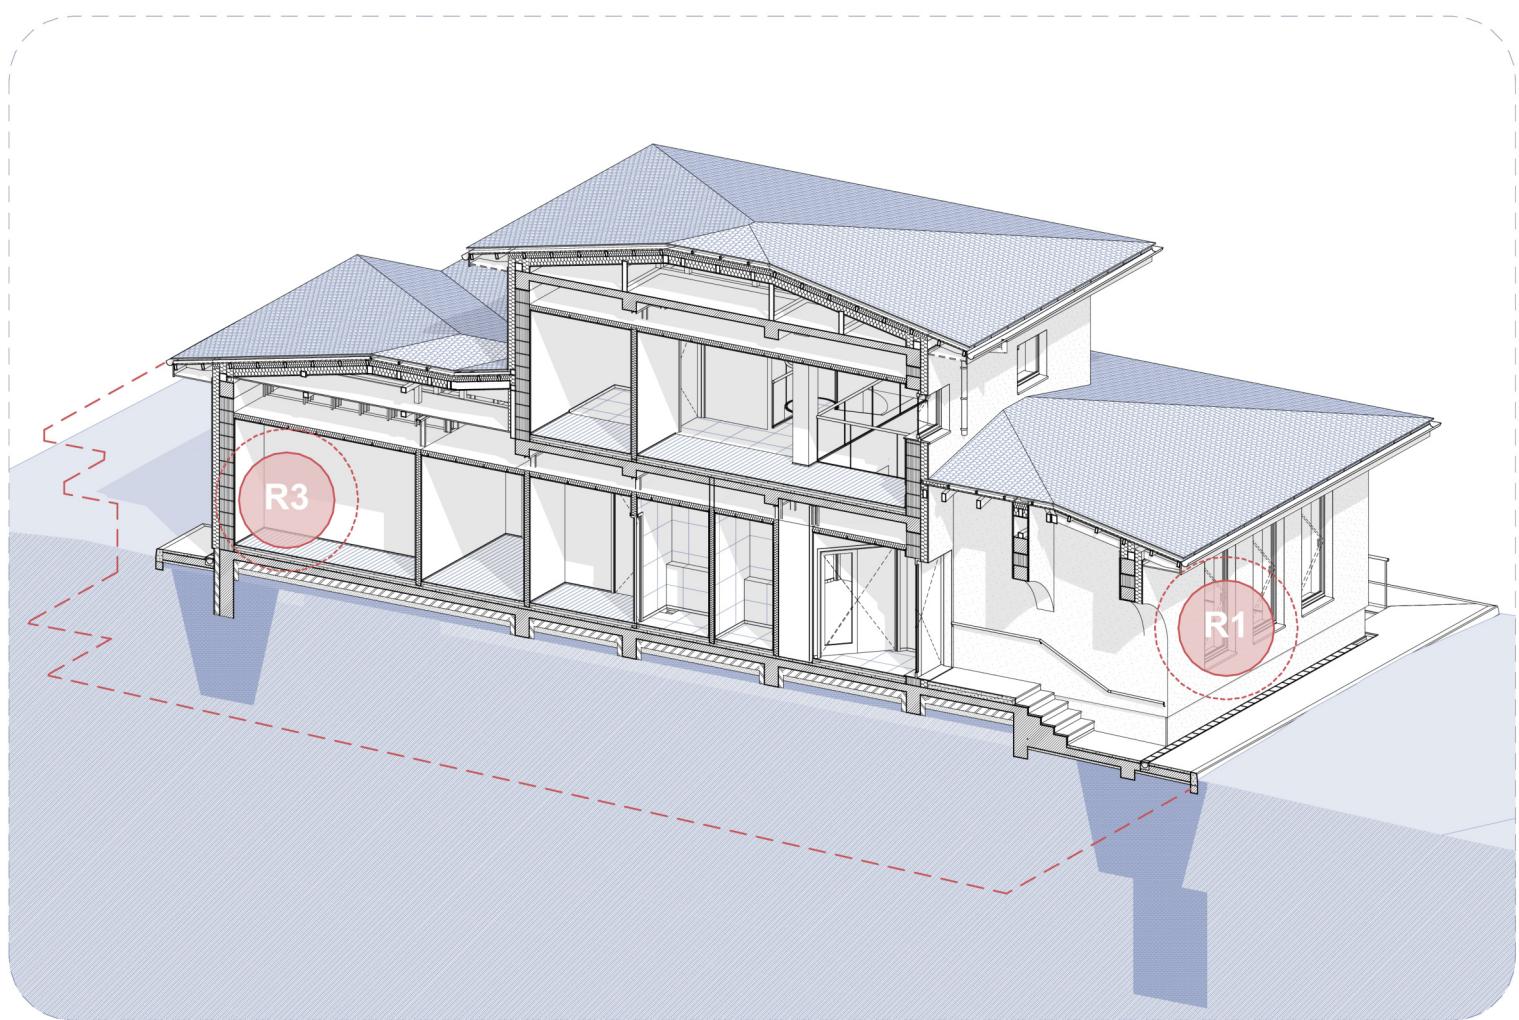


R1 - SUFRAGERIE



R3 - DORMITOR



AXO SECTIUNE B 1:50

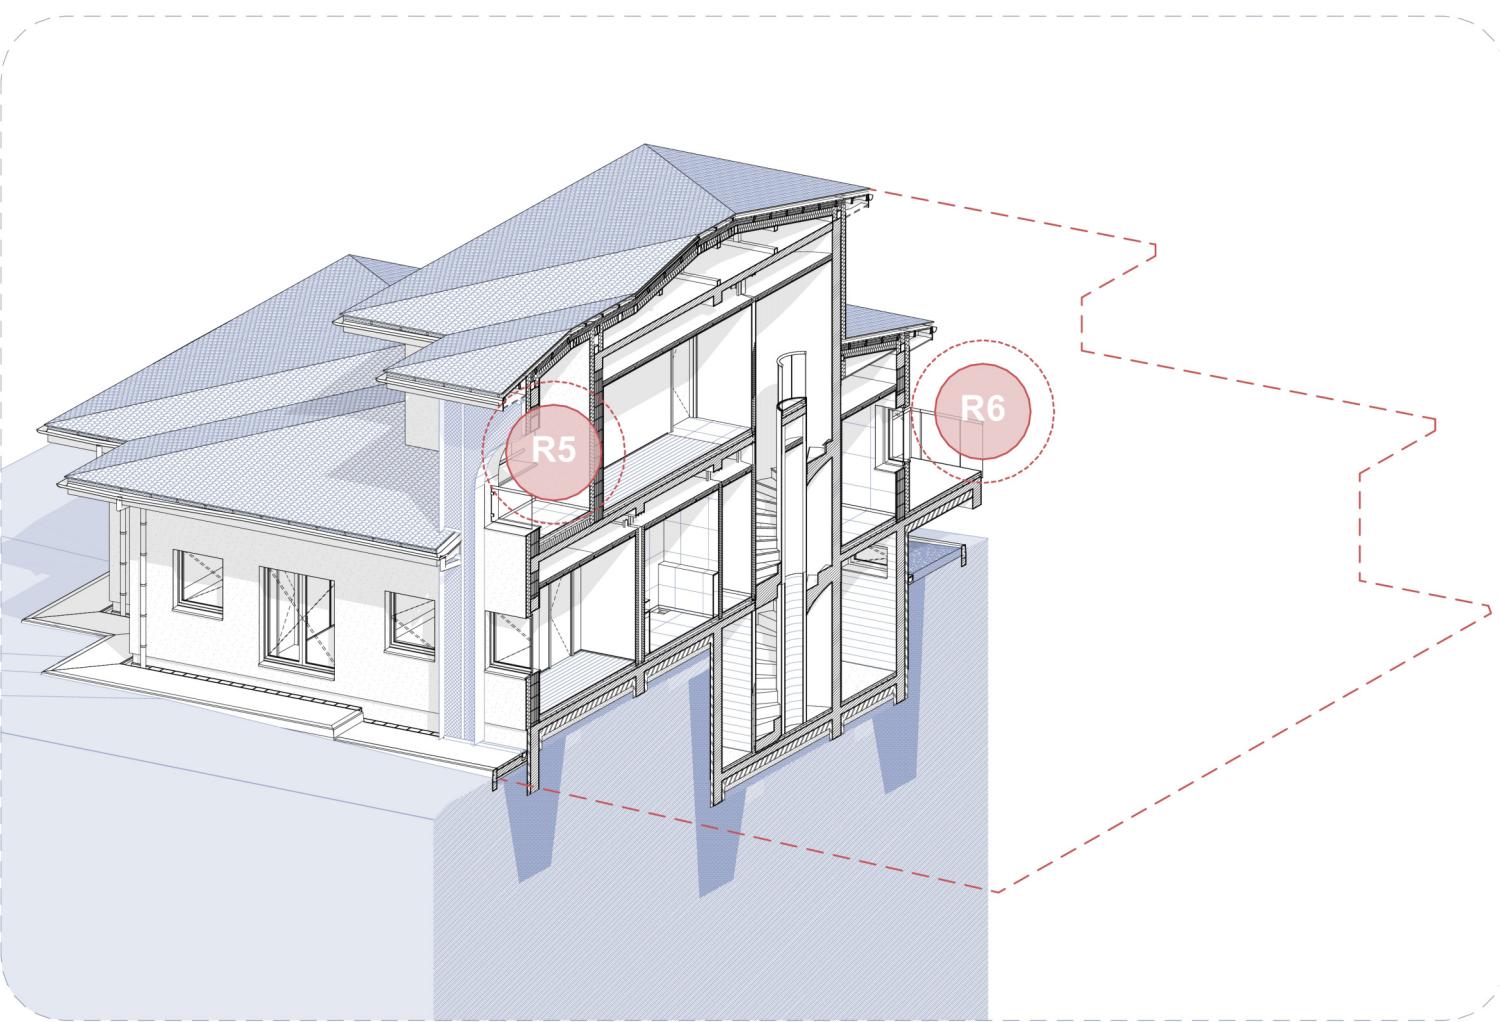


R5 - BALCON



R6 - TERASA




AXO SECTIUNE C 1:50

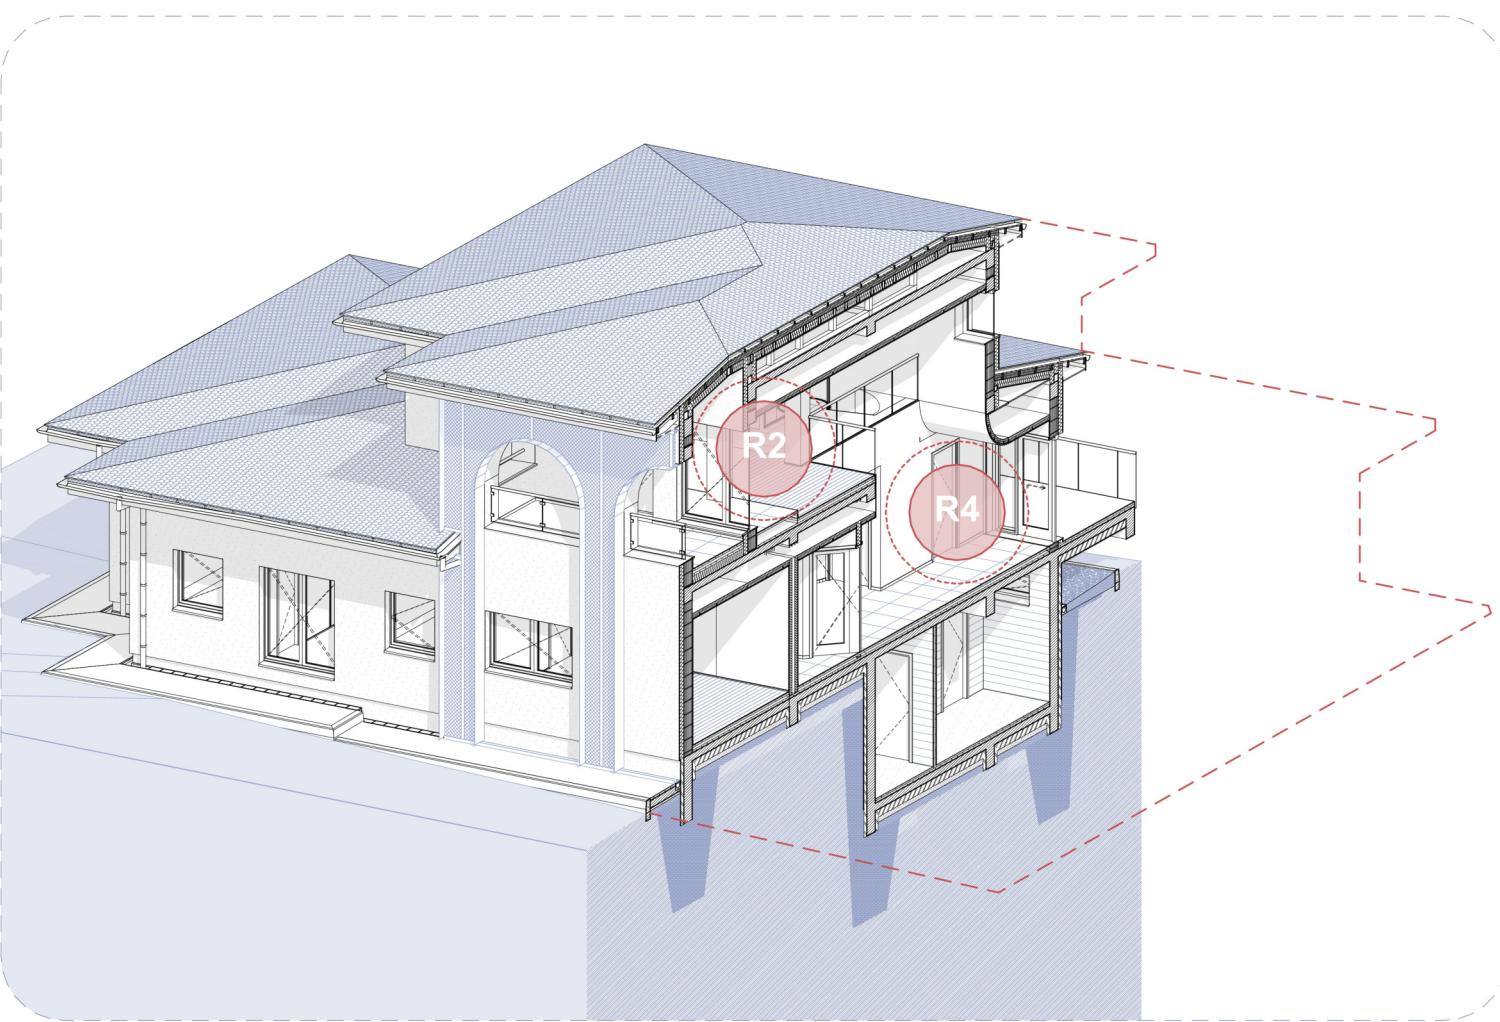


R2 - BIROU




R4 - DINING

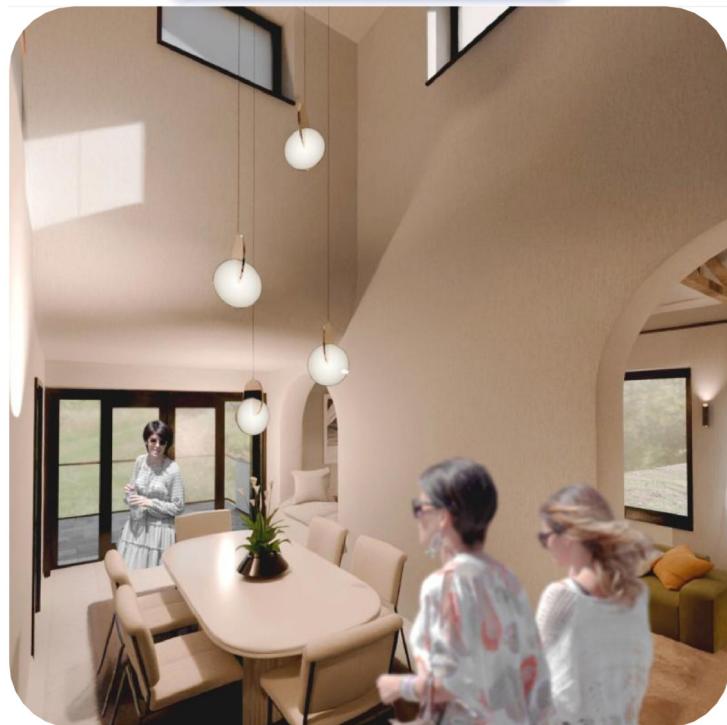


PLAN SUBSOL 1:50

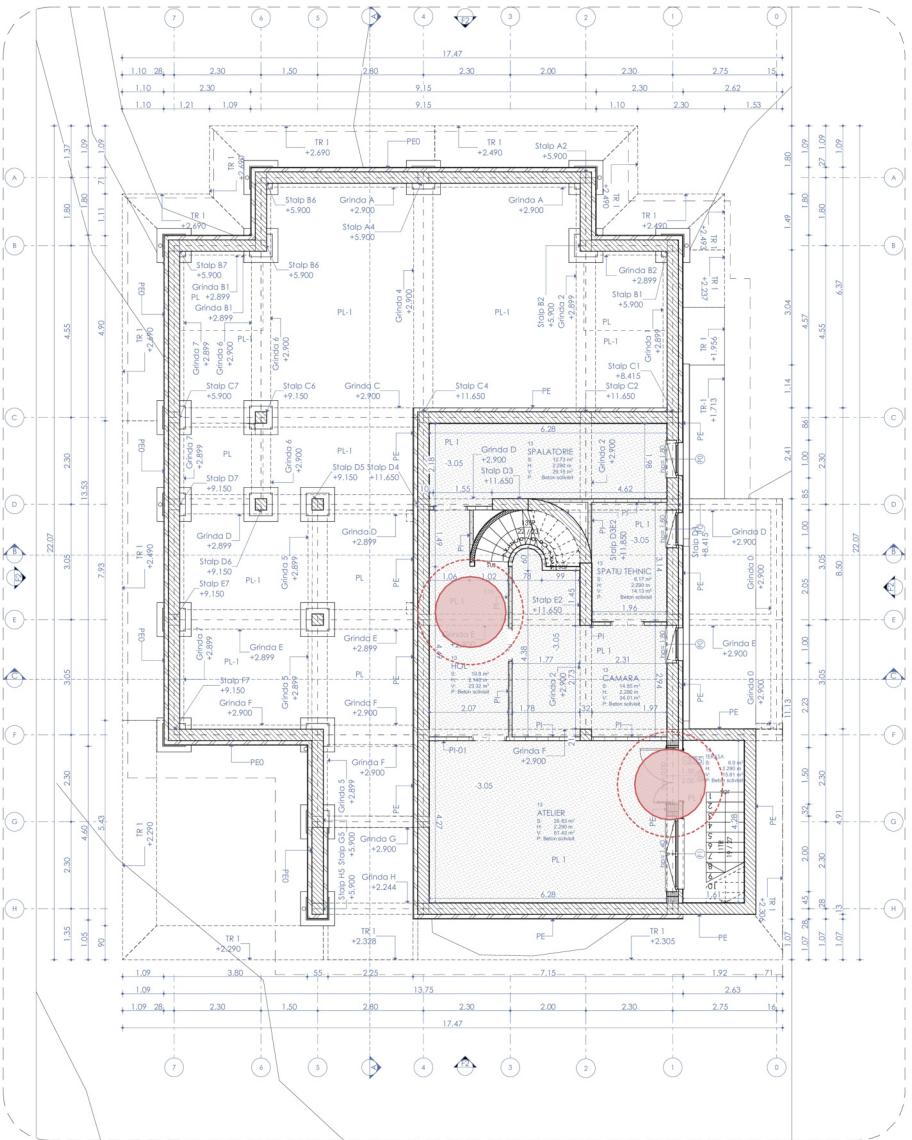


AXO SUBSOL 1:50

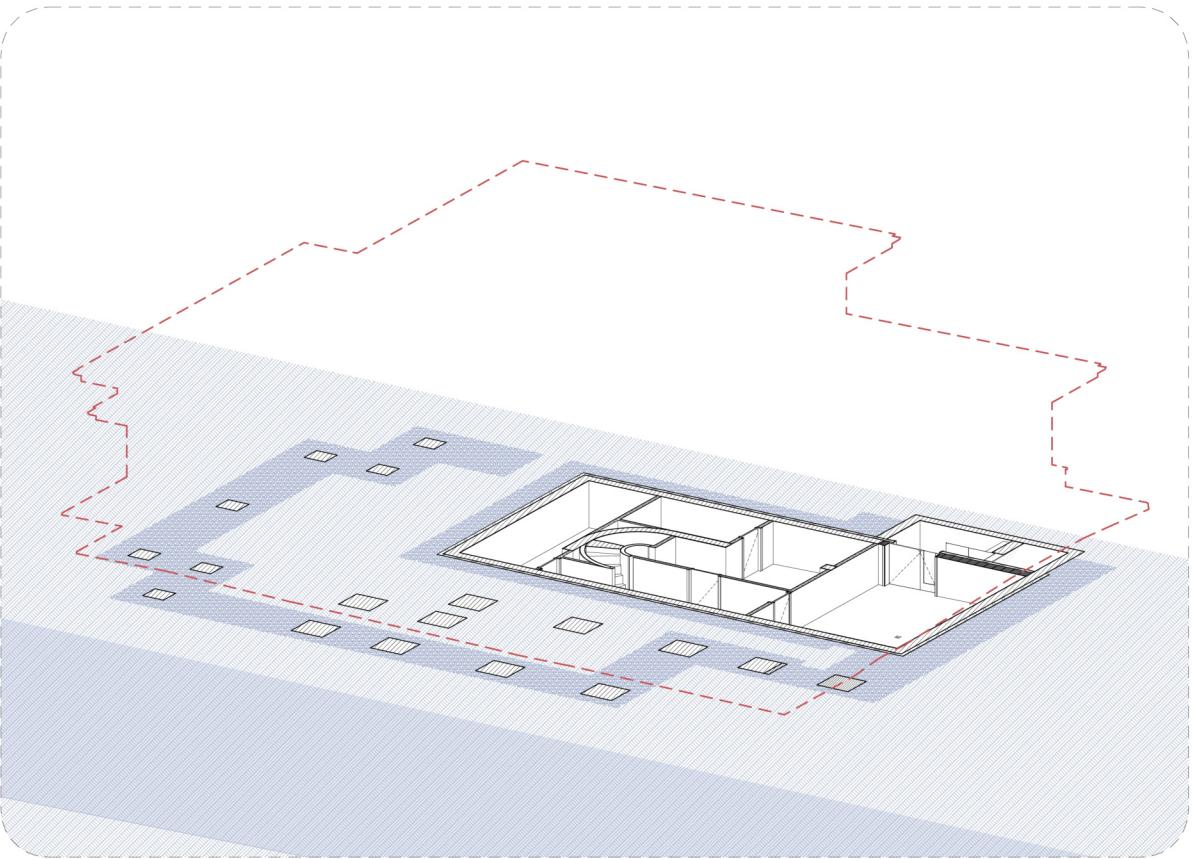


D.S.04 DETALIU 1:10

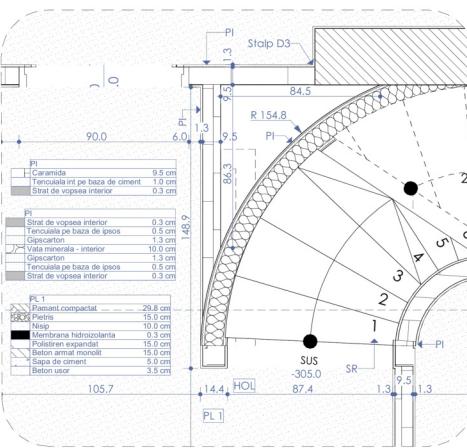


D.S.04 DETALIU 1:10

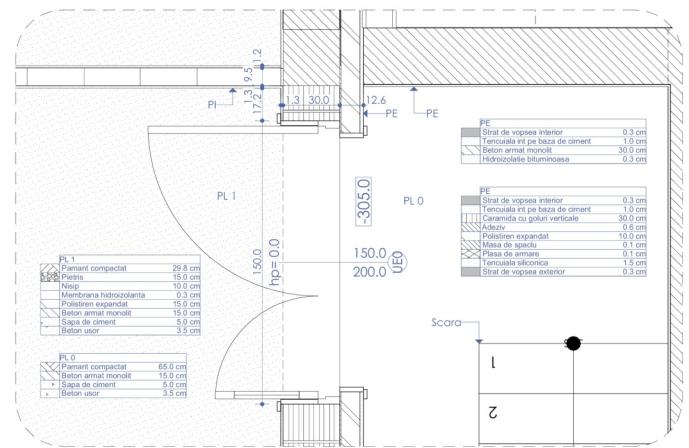


**PLAN PARTER** 1:50

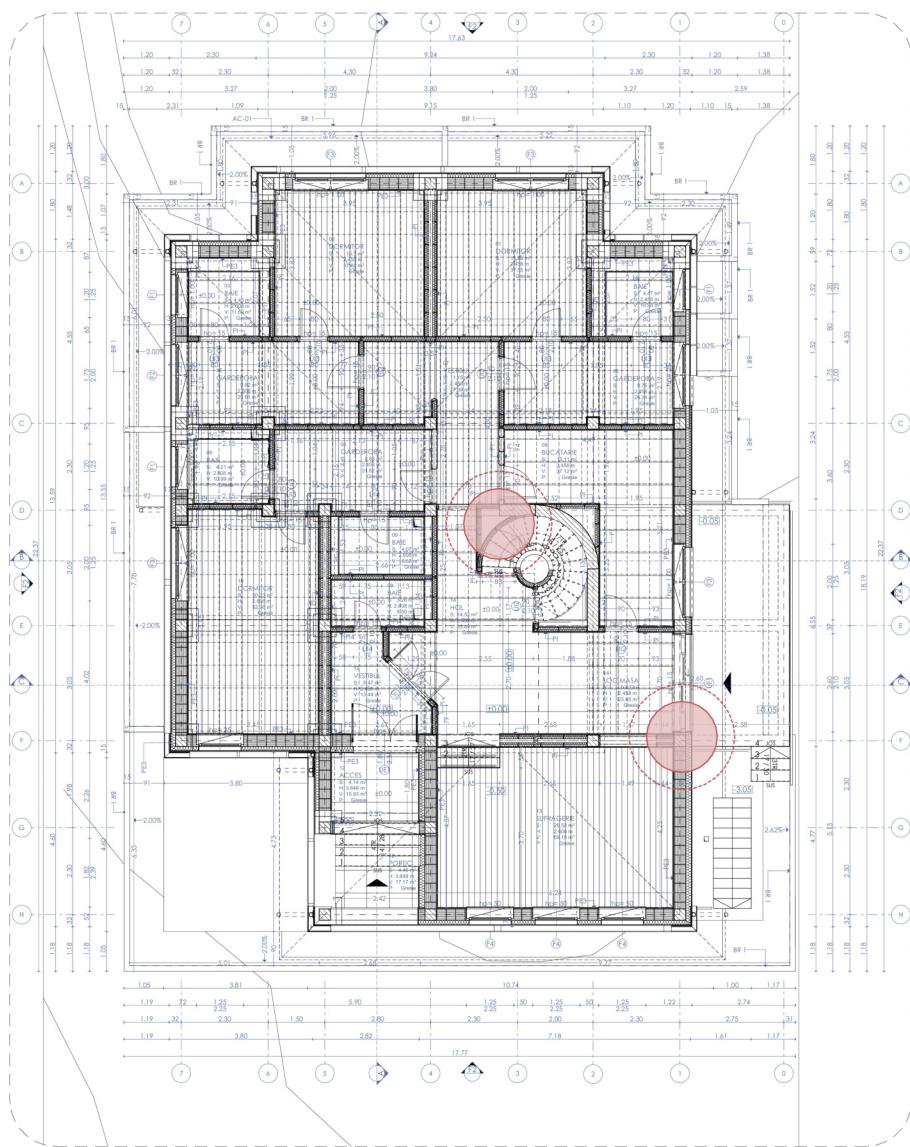


**AXO PARTER** 1:50

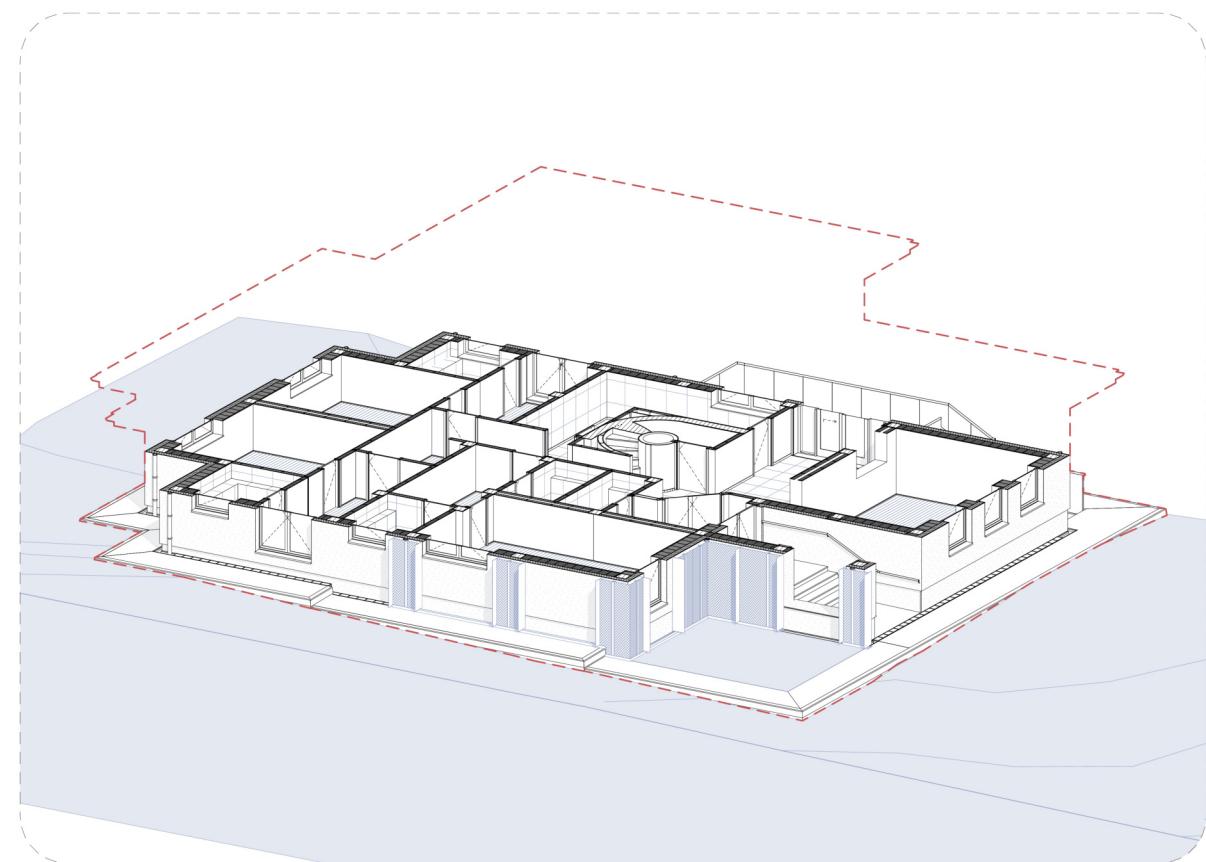


**D.P.01 DETALIU** 1:10

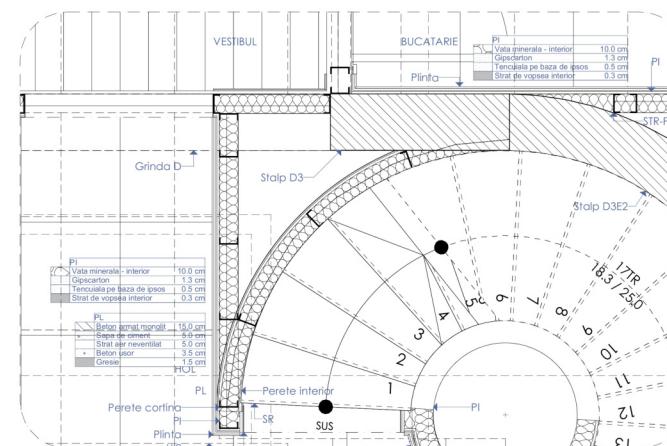


**D.P.01 DETALIU** 1:10

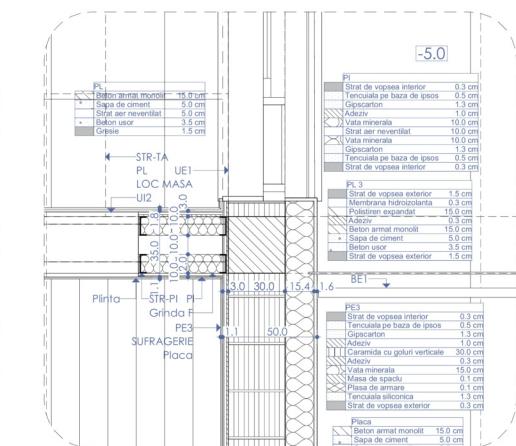


PLAN EТАJ 1:50

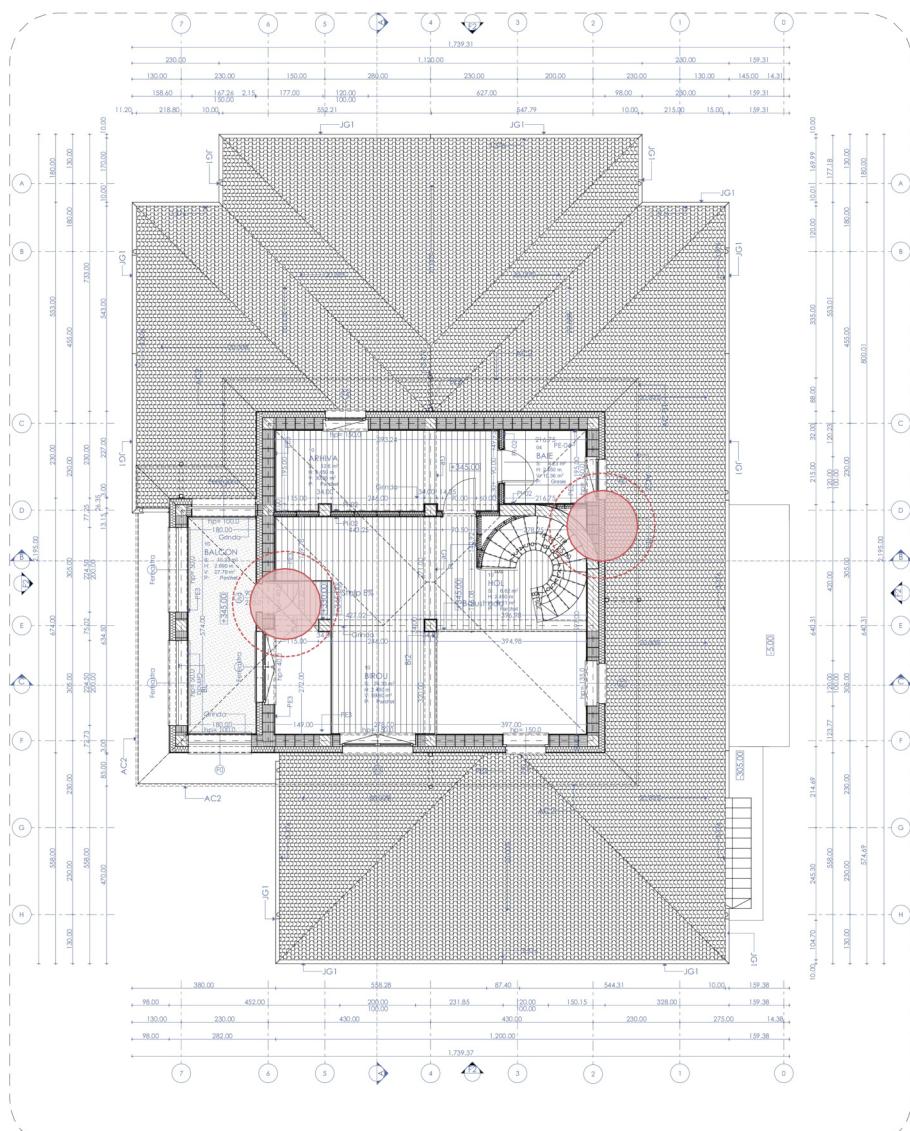


AXO ETAJ 1:50

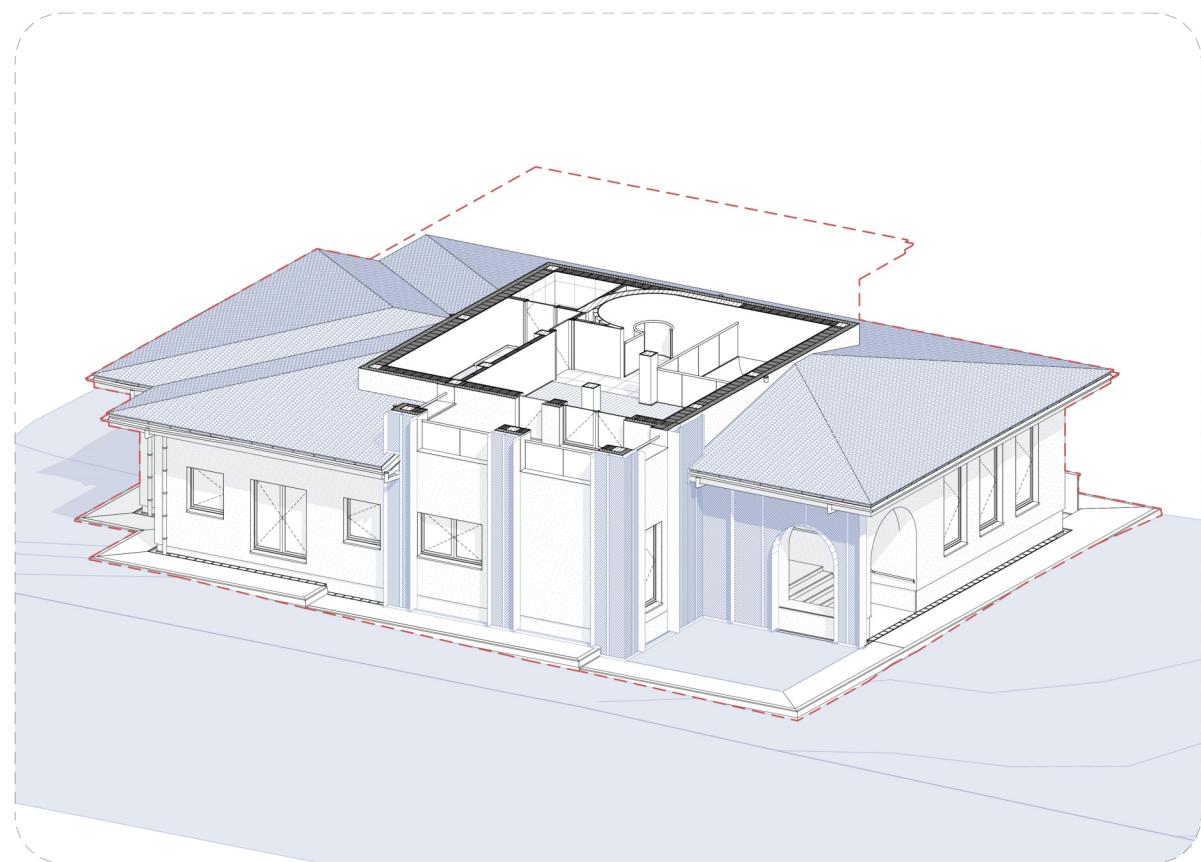


D.E.01 DETALIU 1:10

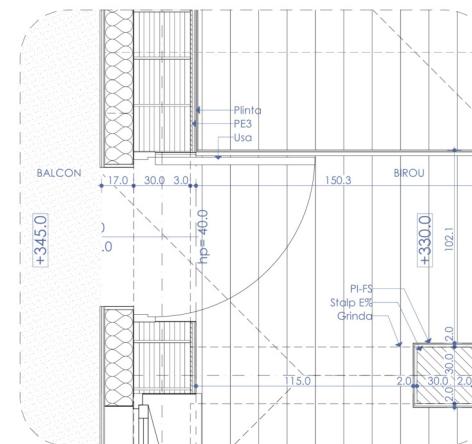


D.E.02 DETALIU 1:10

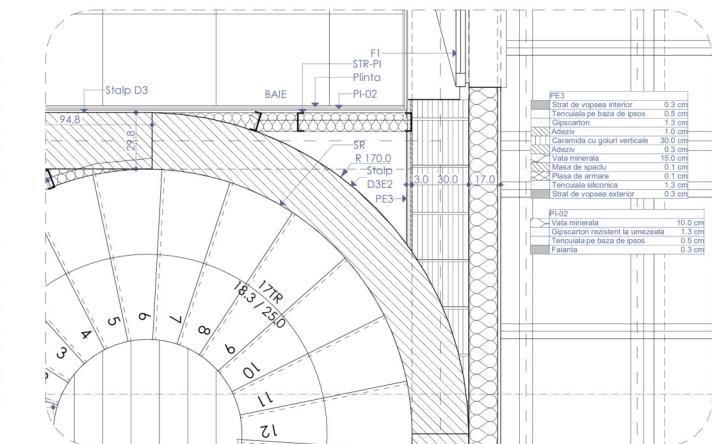


**PLAN ACOPERIS** 1:50

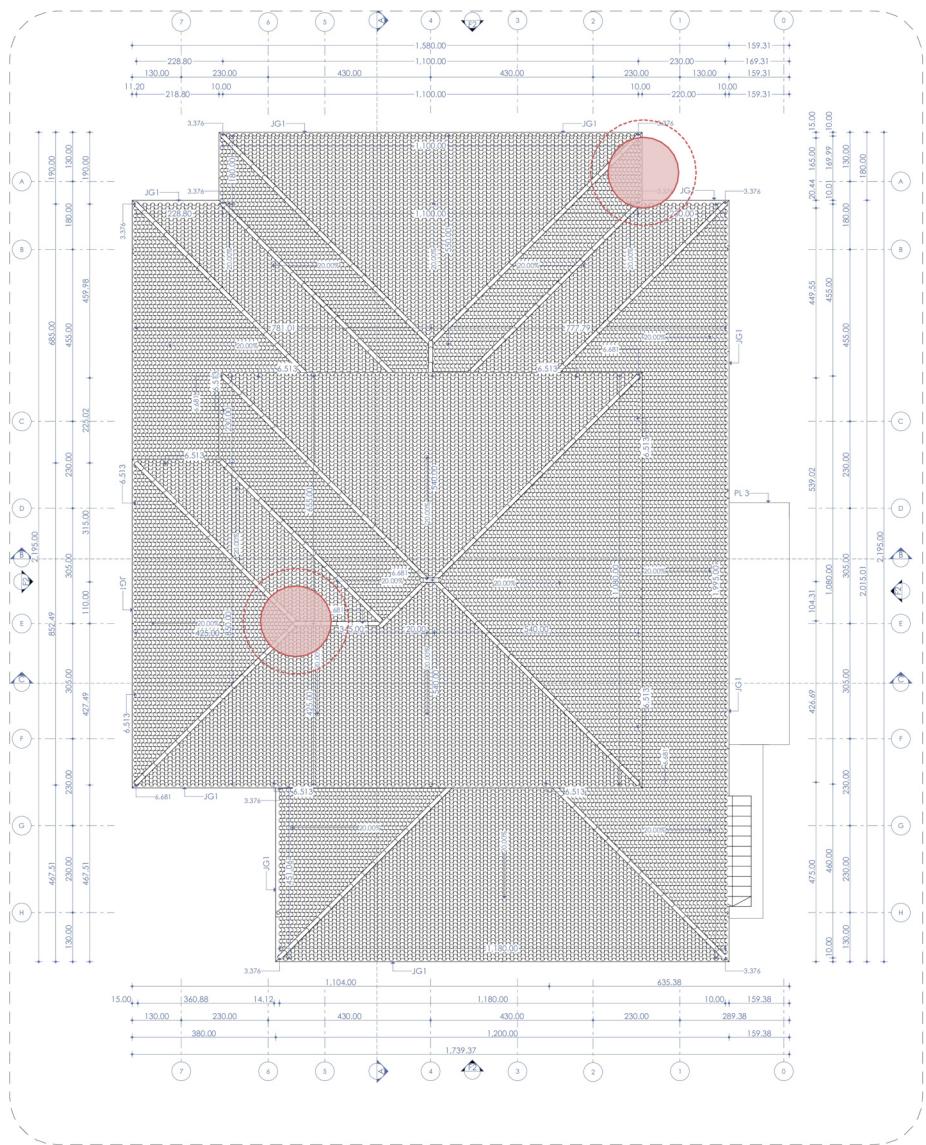


**AXO ACOPERIS** 1:50

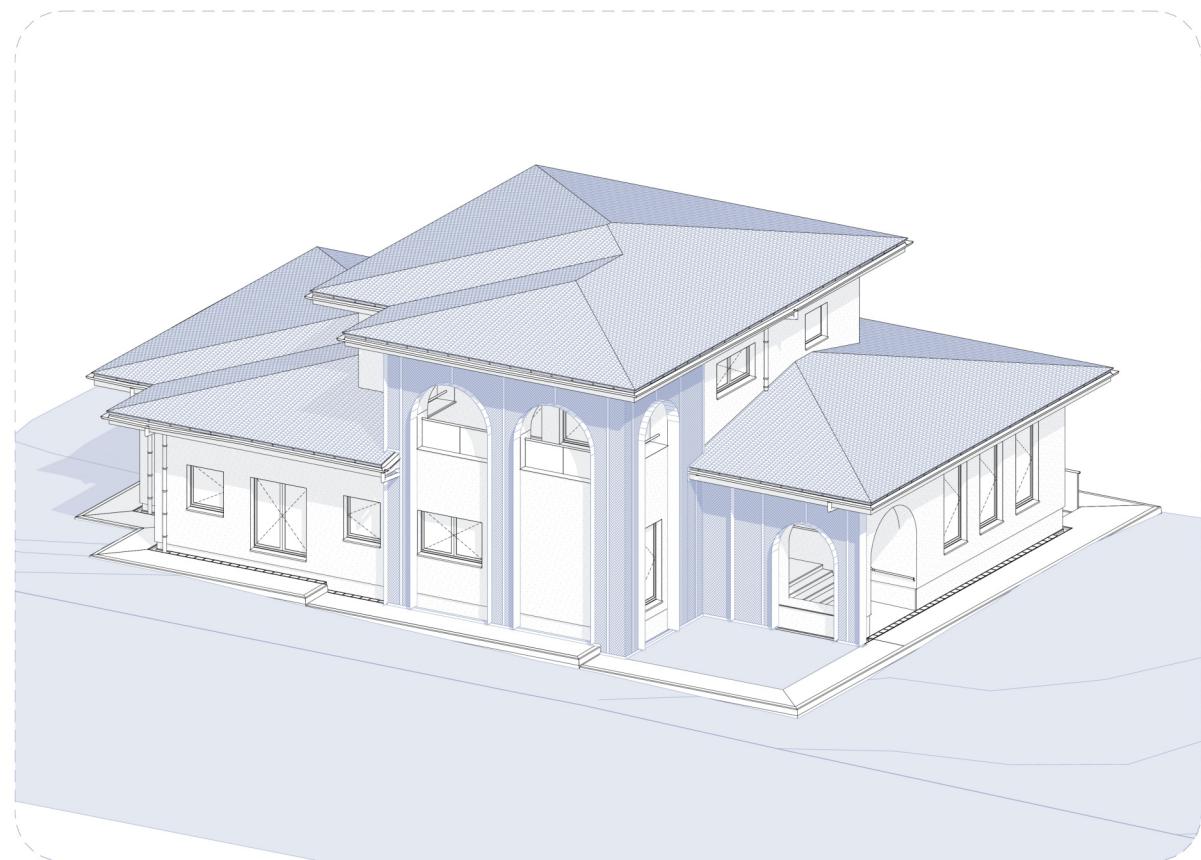

**D.A.01 DETALIU** 1:10

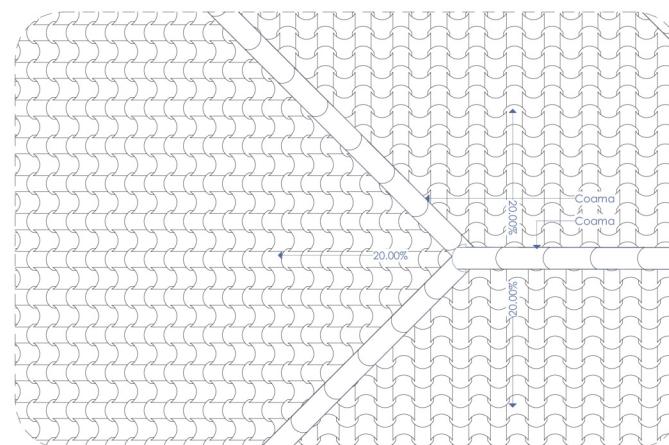

**D.A.02 DETALIU** 1:10

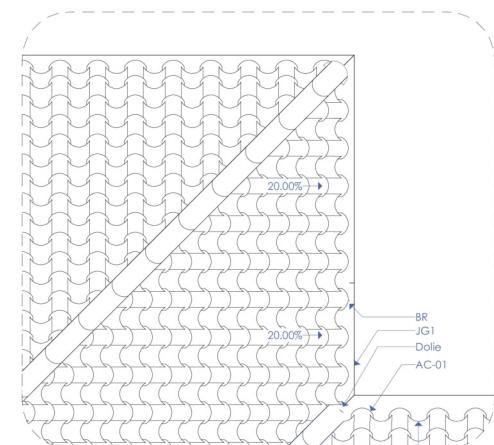

## **SECTIUNE A**

1:50

<b>PL-4</b>	
Tencuiala pe baza de ipsos	0.50 cm
Gips-carton	1.25 cm
Vata minerala	10.00 cm
Strat aer neventilat	67.50 cm
Lemn de inchidere pod	2.50 cm

<b>PL-1</b>	Pamant compactat	25.00 cm
	Pietris	15.00 cm
	Nisip	10.00 cm
<b>M</b>	Membrana hidroizolanta	0.25 cm
	Polistiren expandat	15.00 cm
	Beton armat monolit	15.00 cm
<b>S</b>	Sapa de ciment	5.00 cm
	Strat aer neventilat	5.00 cm
	Beton usor	3.50 cm
	Parchet lamelar	1.50 cm

<b>PI</b>	
Strat de vopsea interior	0.25 cm
Tencuiala pe baza de ipsos	0.50 cm
Gipscarton	1.25 cm
Vata minerală - interior	10.00 cm
Strat aer nevernălit	10.00 cm
Vata minerală - exterior	10.00 cm
Gipscarton	1.25 cm
Tencuiala pe baza de ipsos	0.50 cm
Strat de vopsea exterior	0.25 cm

PE3	
Strat de vopsea interior	0.25 cm
Tencuiala pe baza de ipsos	0.50 cm
Gipscarton	1.25 cm
Adeziv	1.00 cm
Caramida cu goluri verticale	30.00 cm
Adeziv	0.30 cm
Vata minerala	15.00 cm
Masa de spadlu	0.10 cm
Plasa de armare	0.10 cm
Tencuiala siliconica	1.25 cm
Strat de vopsea exterior	0.25 cm

	Strat de vopsea exterior	0.25 cm
<b>AC1</b>		
<input checked="" type="checkbox"/> Folie anticondens	0.25 cm	
<input type="checkbox"/> Placaj OSB	1.25 cm	
<input type="checkbox"/> Vata minerala	15.00 cm	
<input type="checkbox"/> Vata minerala	10.00 cm	
<input type="checkbox"/> Astereala	2.00 cm	
<input checked="" type="checkbox"/> Membrana hidroizolanta	0.25 cm	
<input type="checkbox"/> Spatiu sirci	5.00 cm	
<input type="checkbox"/> Spatiu sirci	3.00 cm	

<b>TR 1</b>	
Pietris	10.00 cm
Nisip	5.00 cm
Beton armat monolit	15.00 cm
Sana de ciment	5.00 cm

PL1	
Tencuiala pe baza de ipsos	0.50 cm
Gipscarton	1.25 cm
Vata minerala	10.00 cm
Strat aer neventilat	46.50 cm
Beton armat monolit	15.00 cm

