



CASA BACAU

arh. Mihael - Ionut FURDU

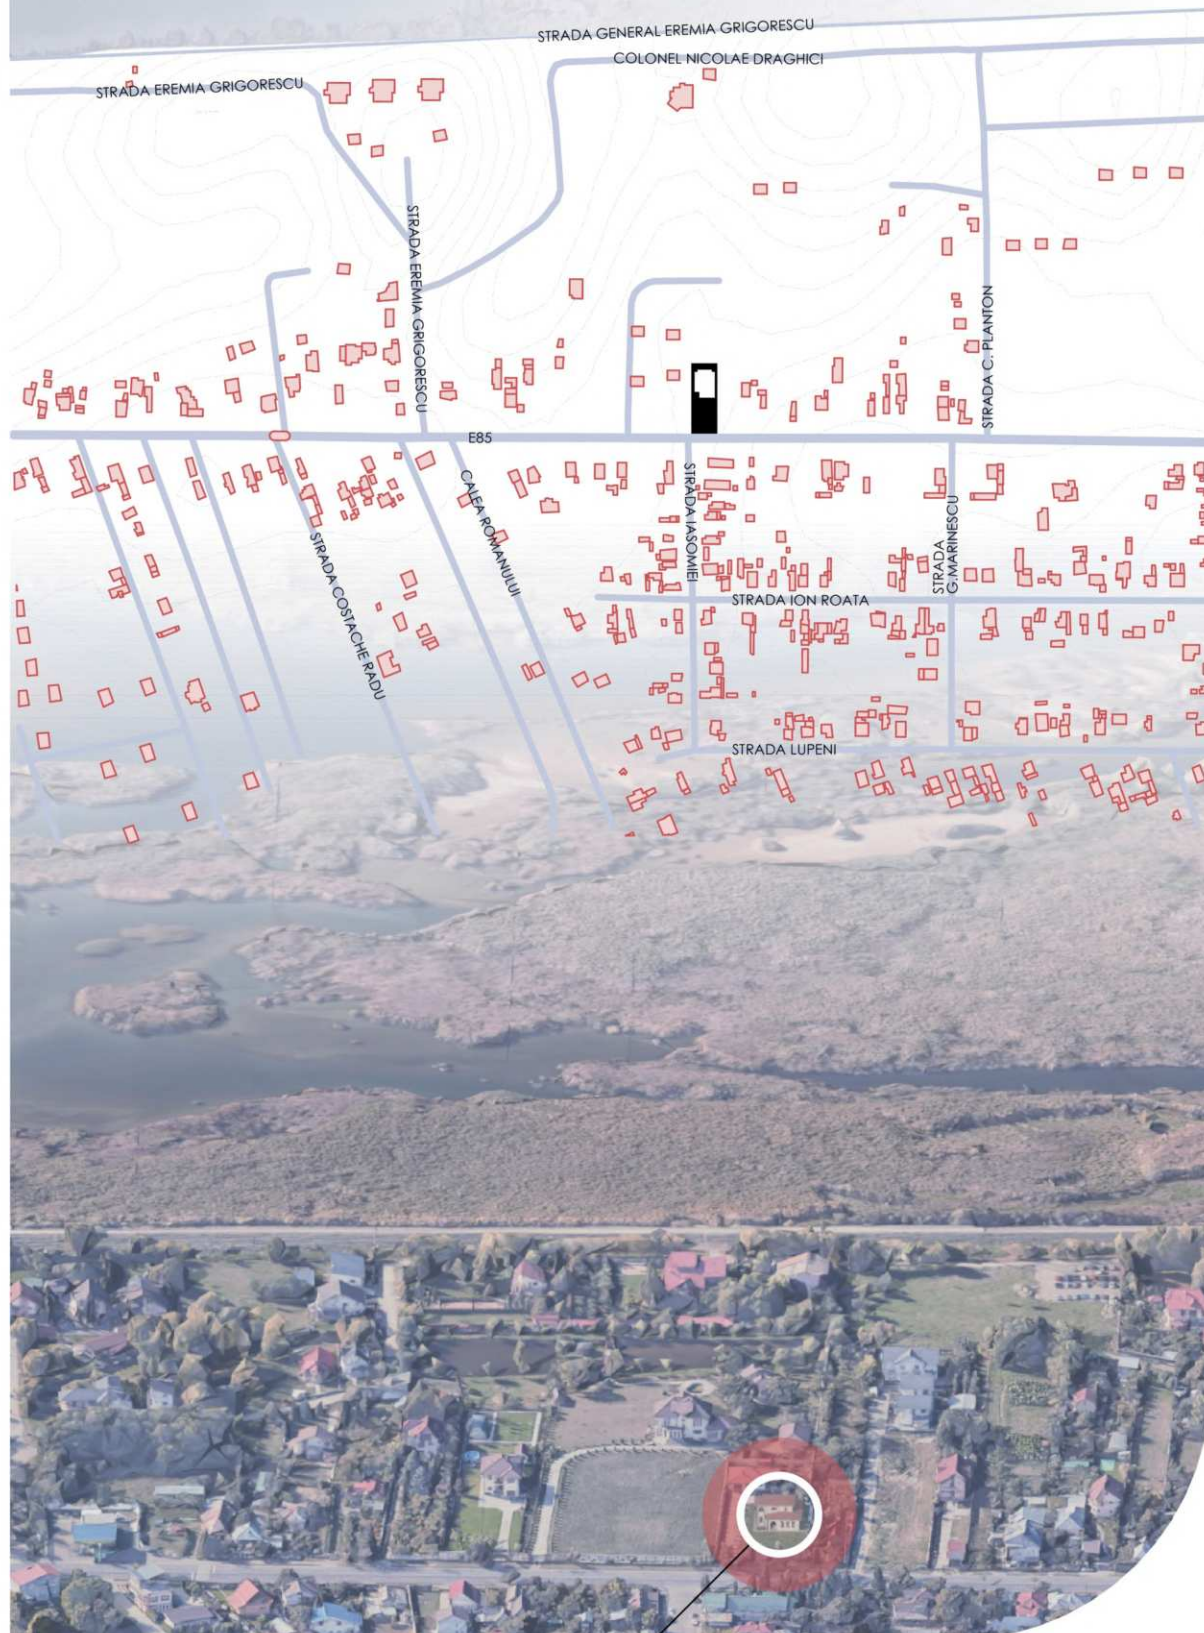




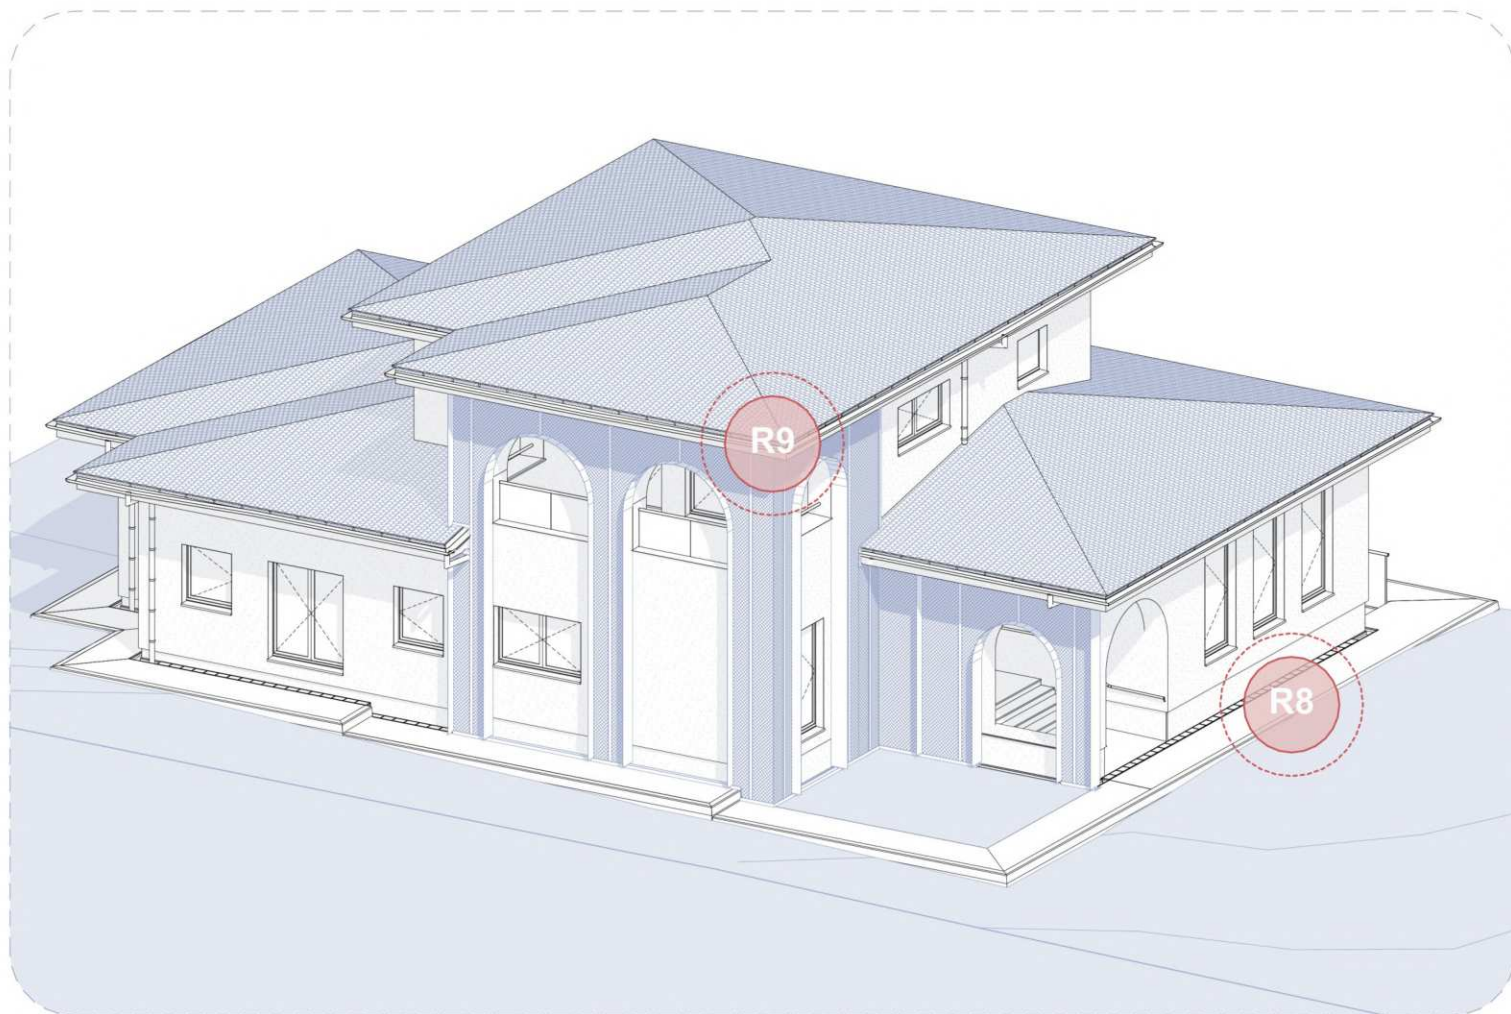


R8 - FATADA INTRARE




R9 - PERETE VERDE

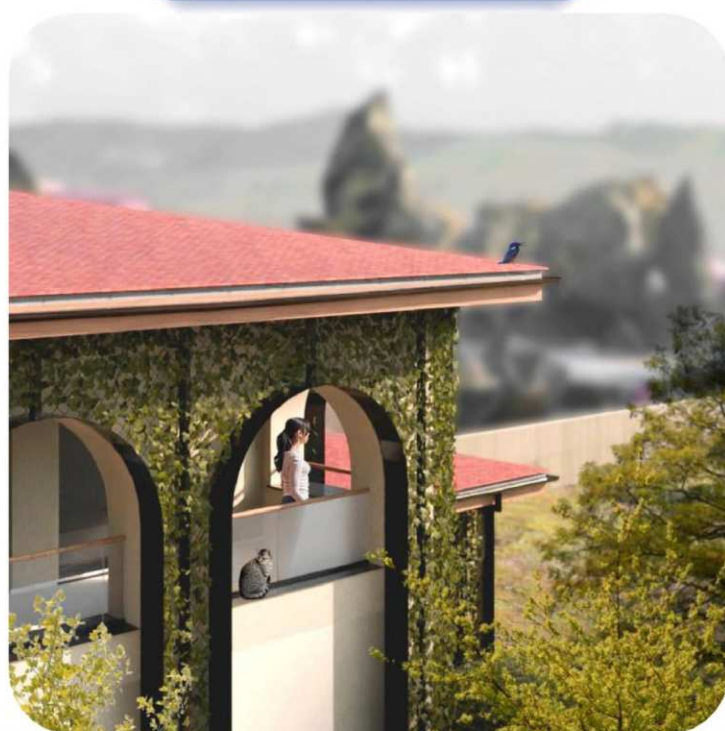


AXO SECTIUNE A 1:50

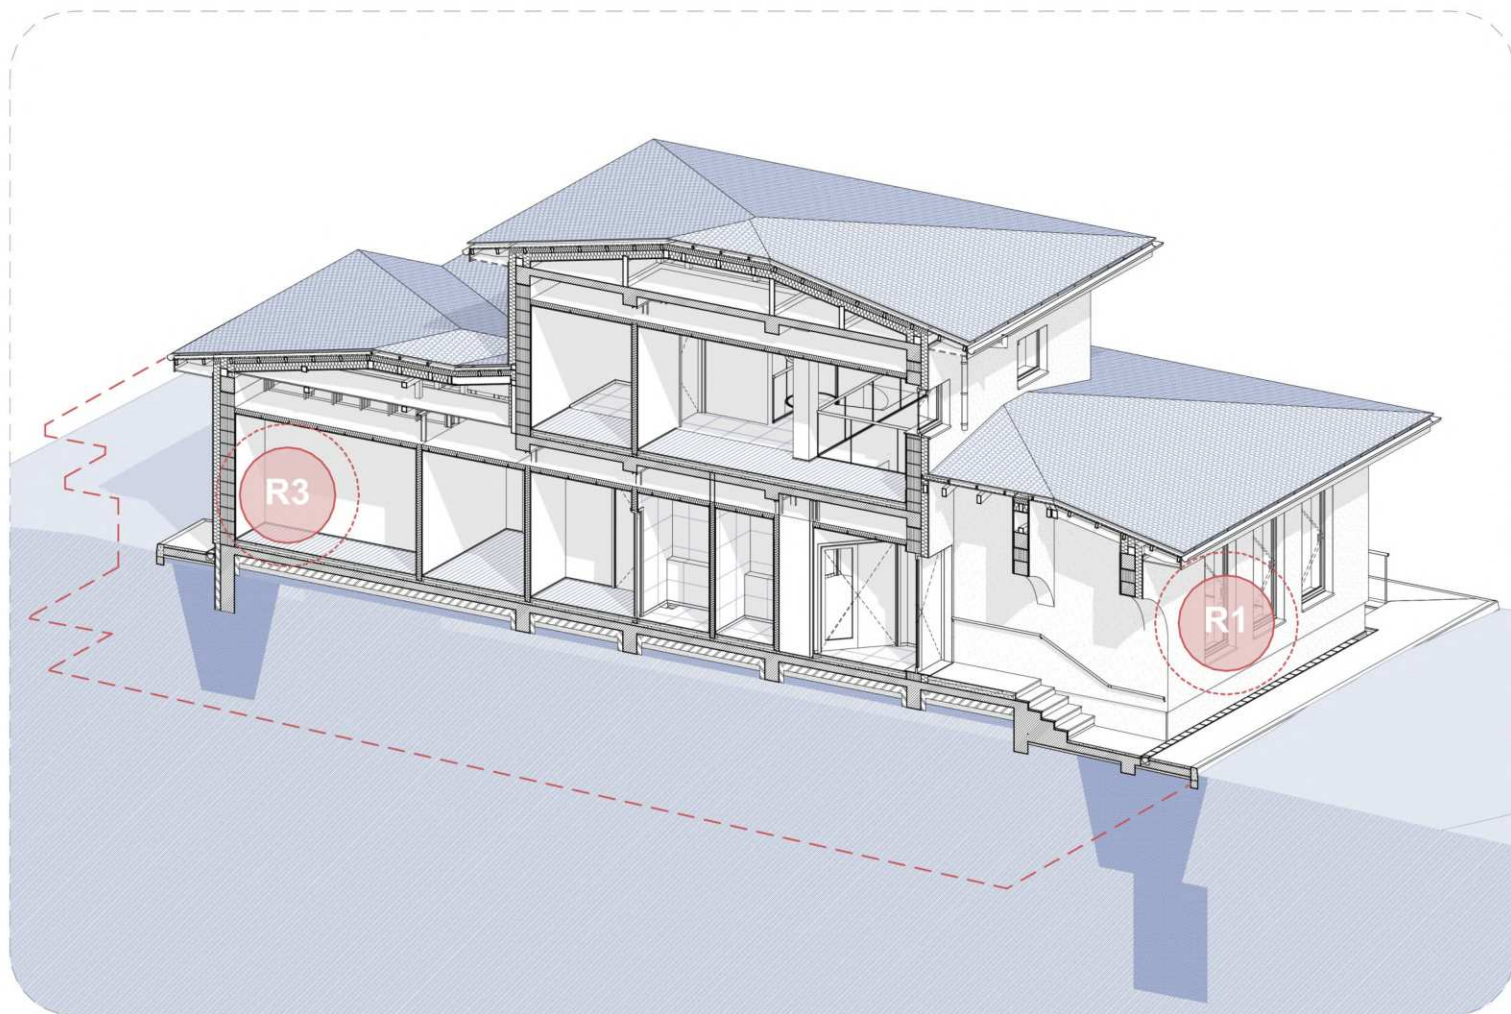


R1 - SUFRAGERIE

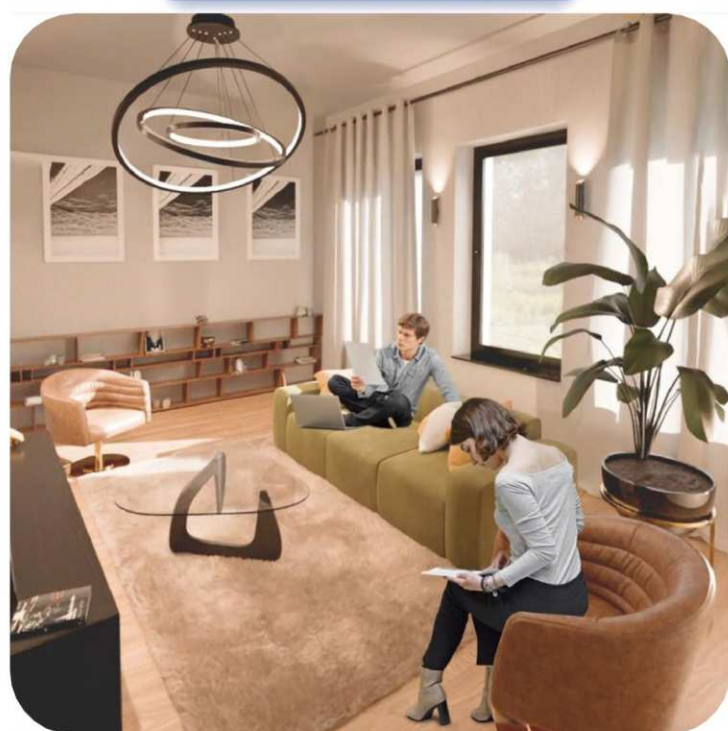


R3 - DORMITOR

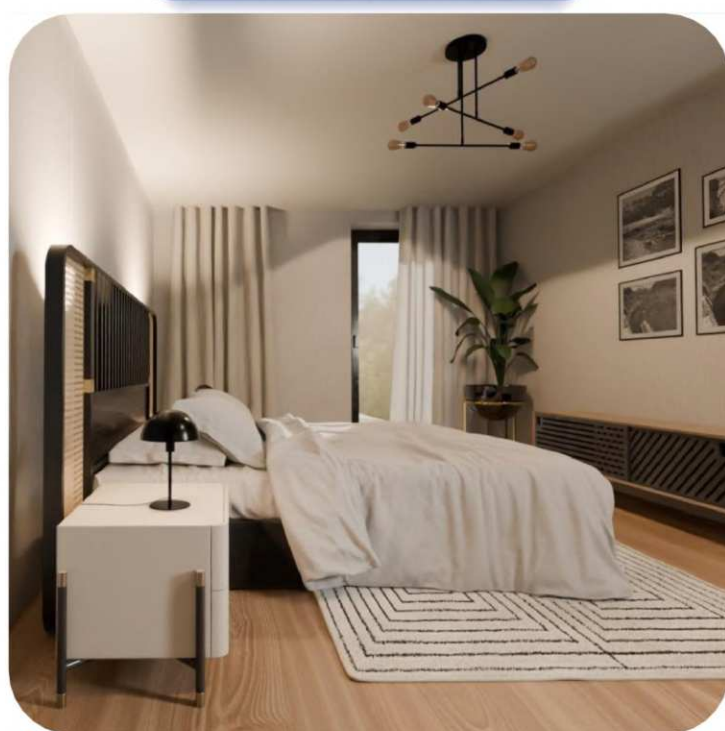

AXO SECTIUNE B 1:50

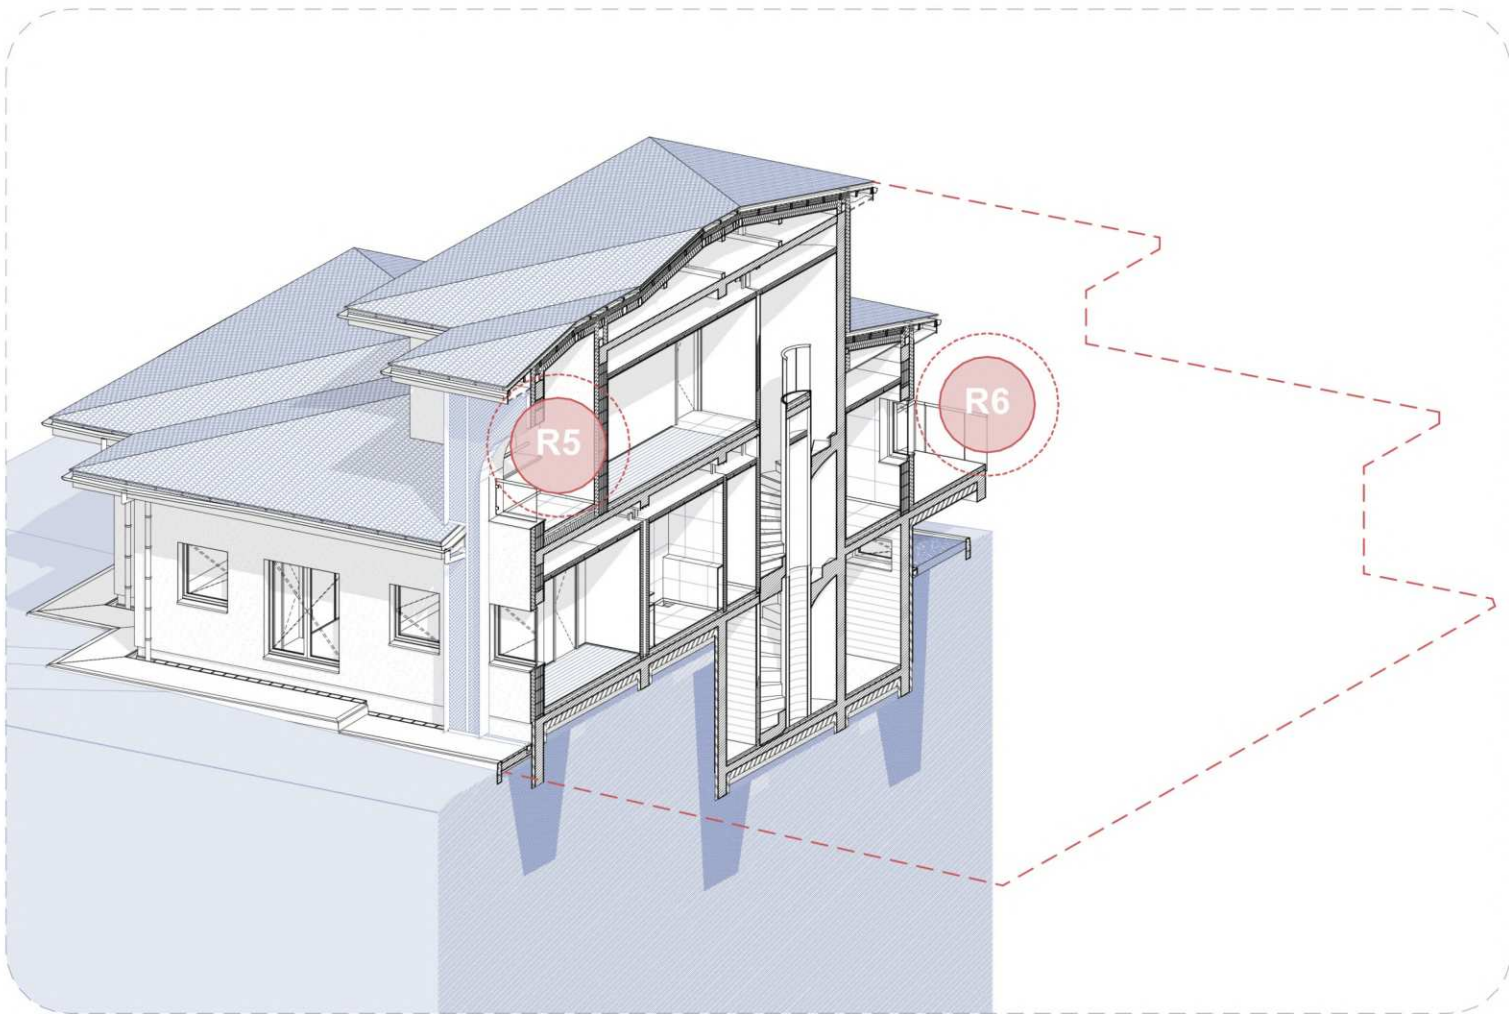


R5 - BALCON

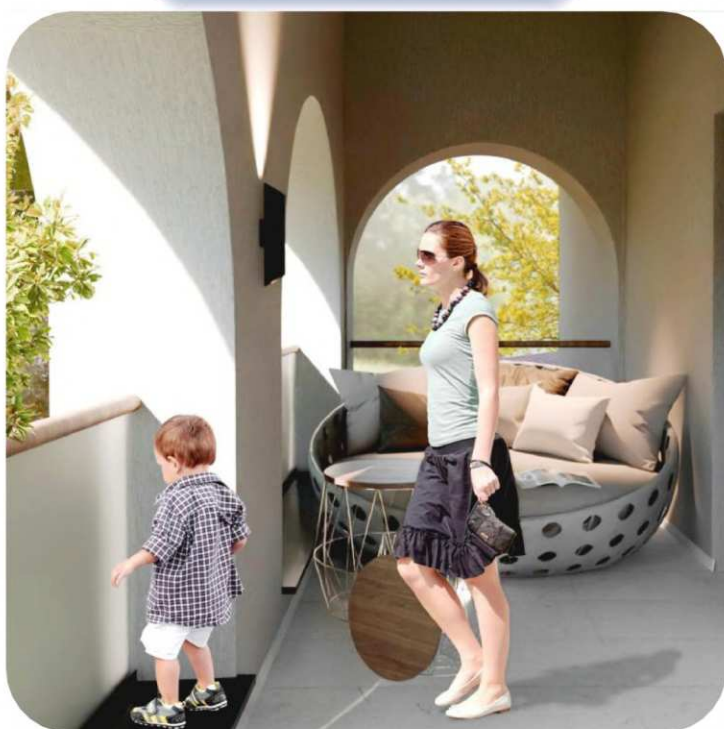


R6 - TERASA




AXO SECTIUNE C 1:50




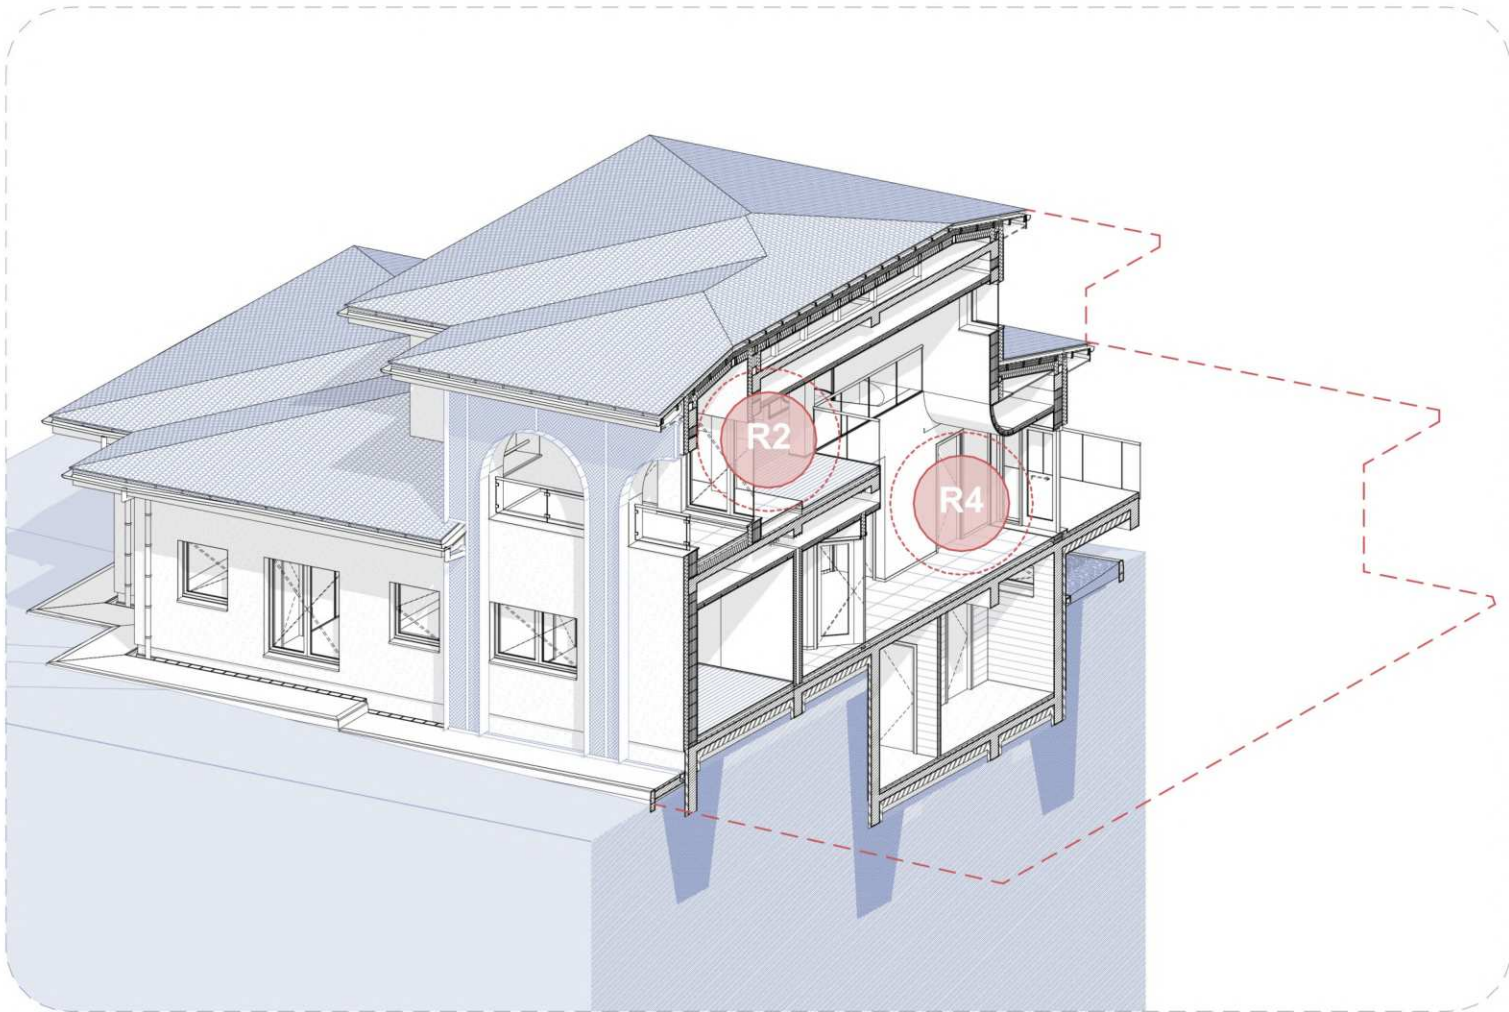


R2 - BIROU

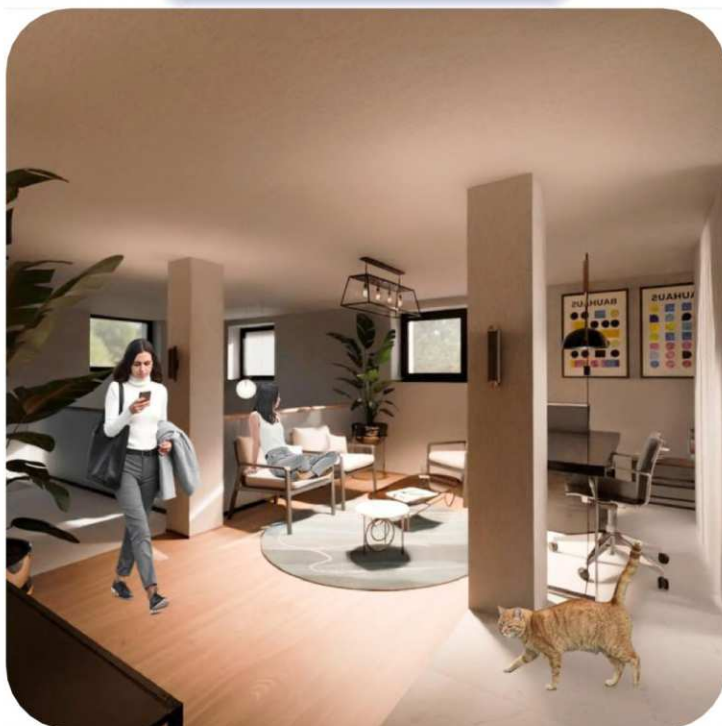


R4 - DINING

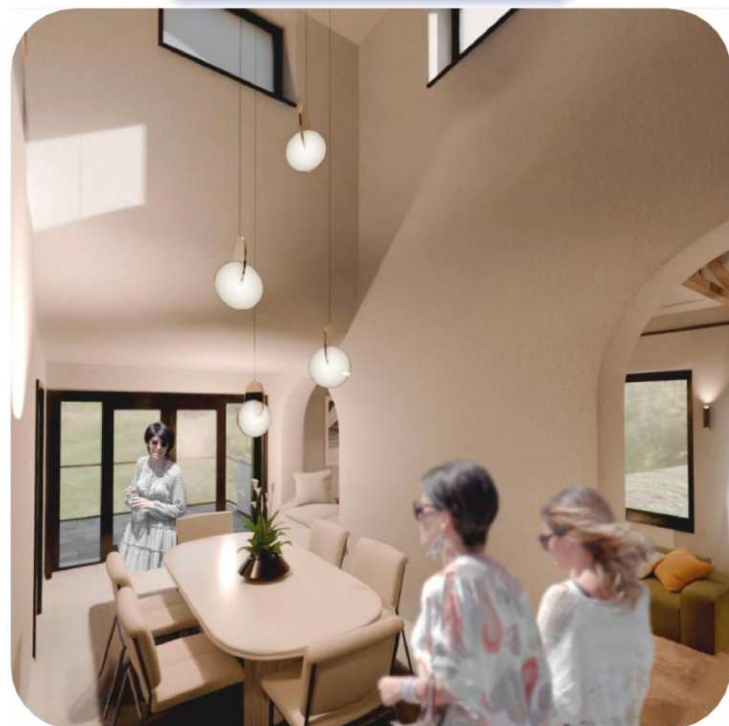


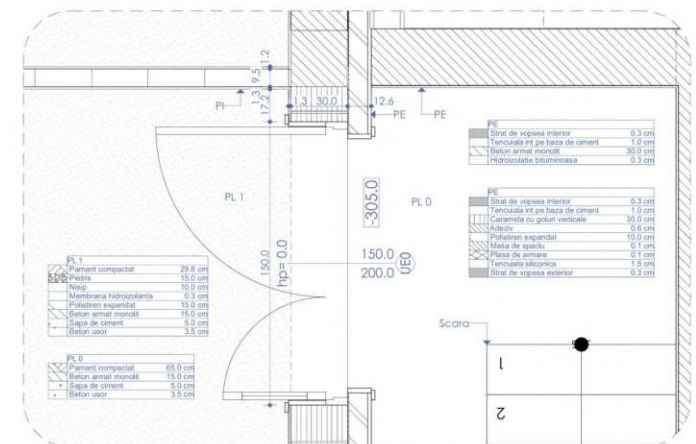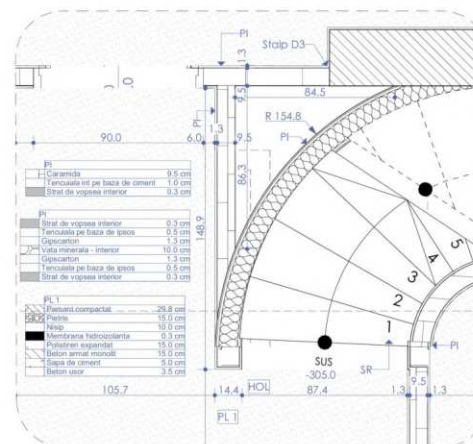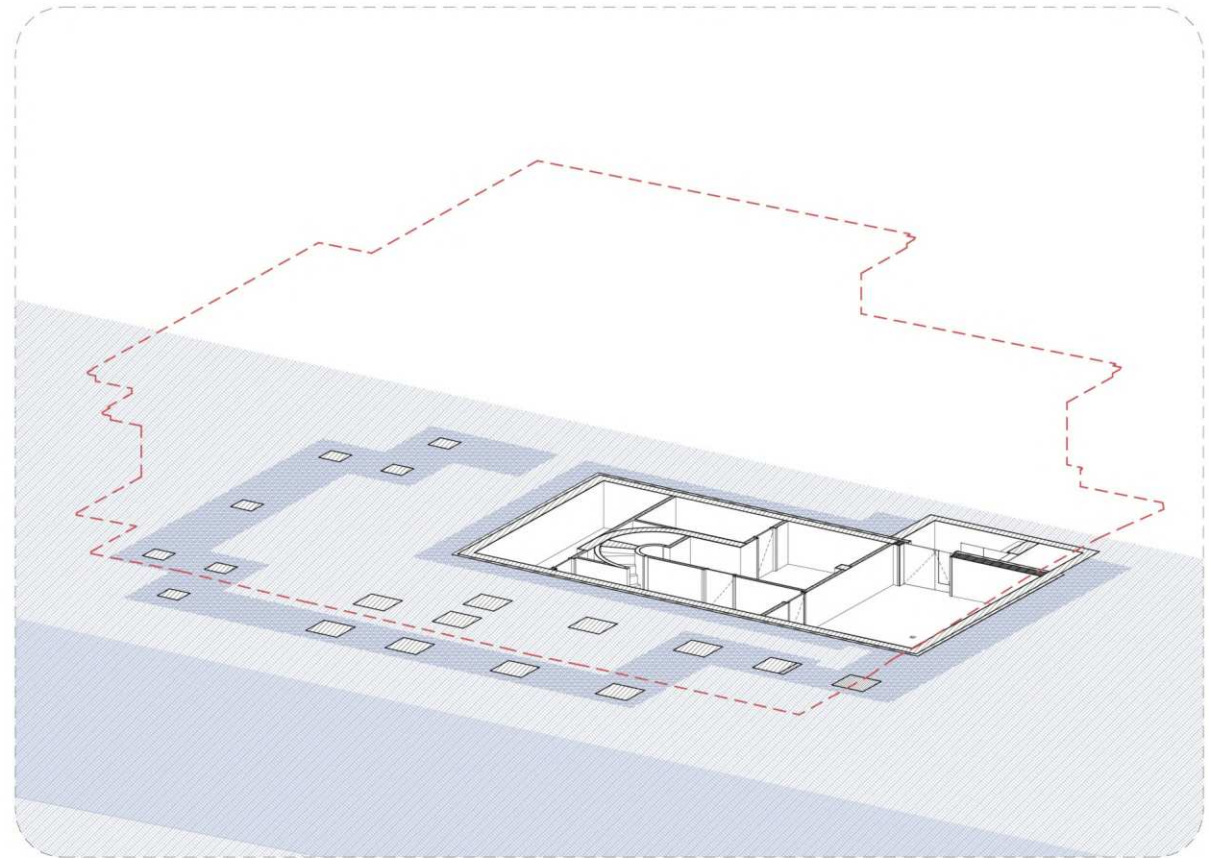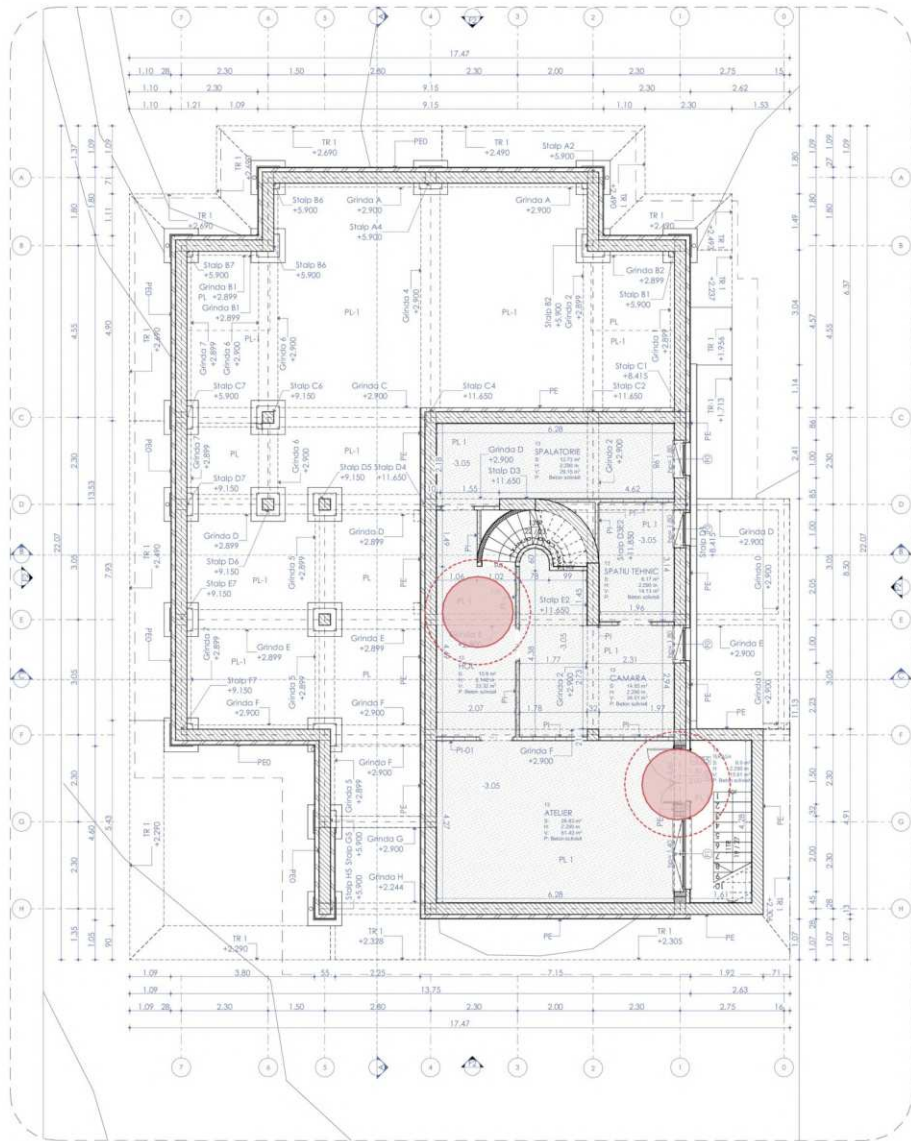


PLAN ETAJ 1:50

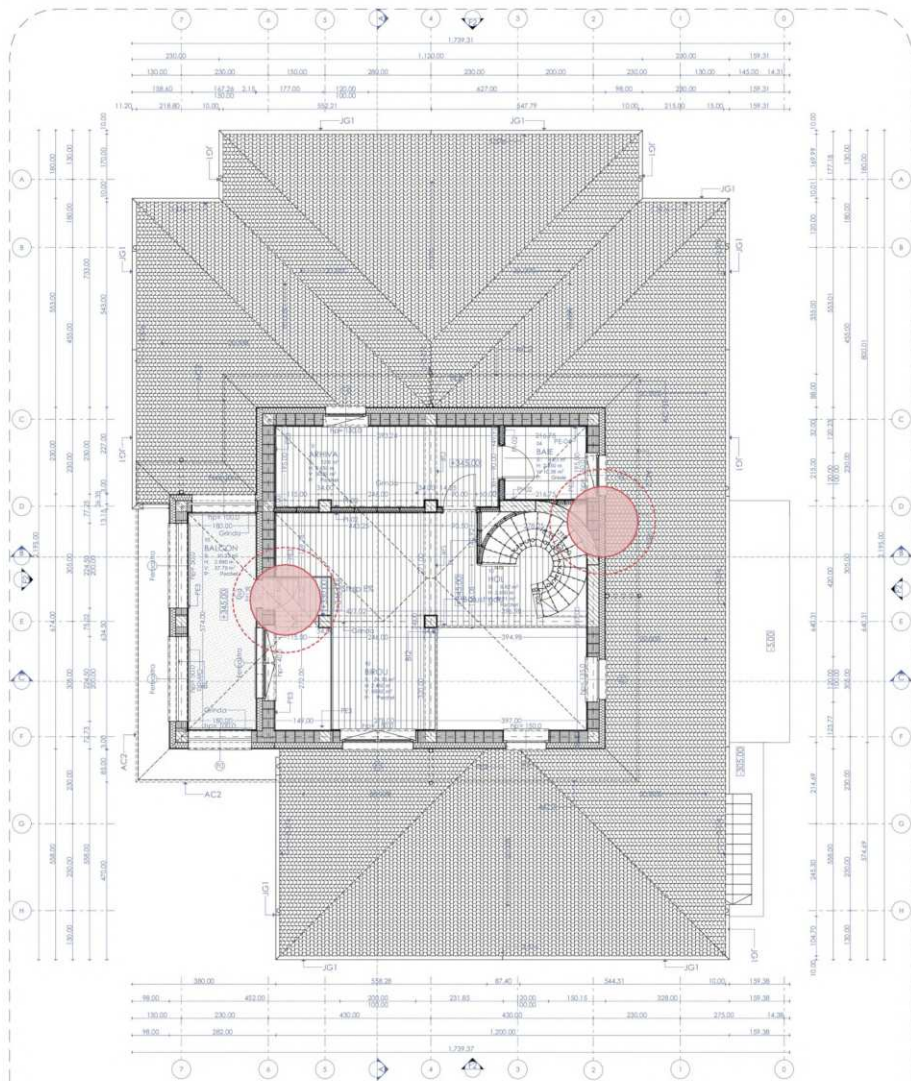


AXO ETAJ 1:50

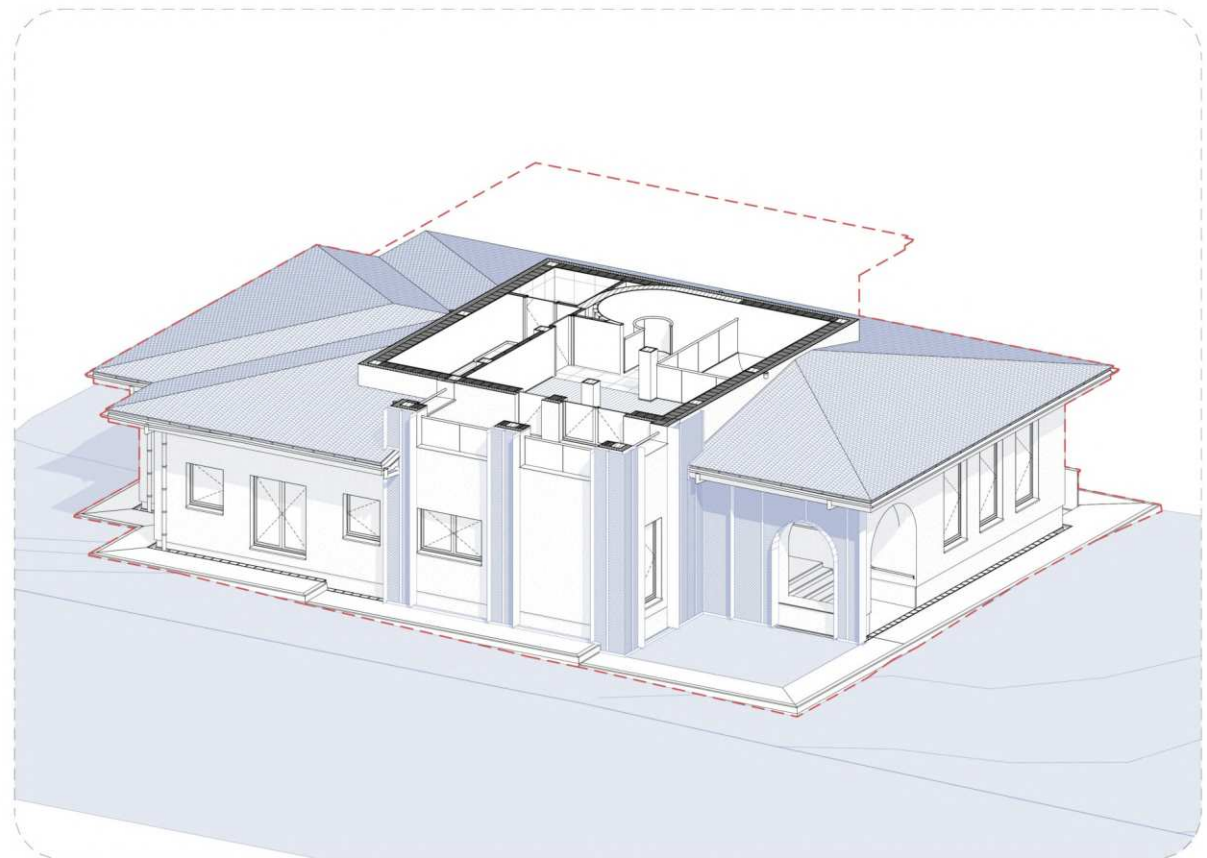


D.E.01 DETALIU 1:10

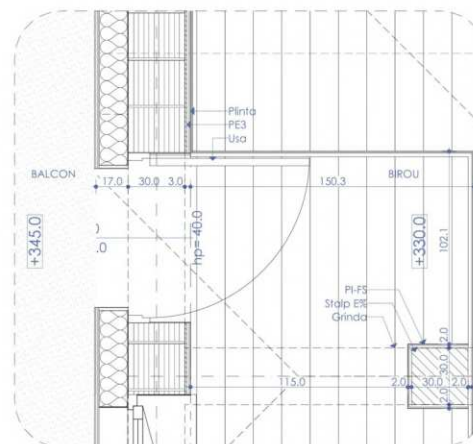


D.E.02 DETALIU 1:10

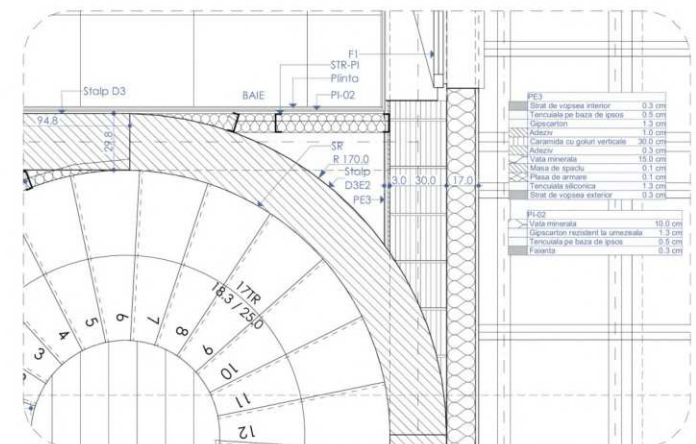


PLAN ACOPERIS 1:50

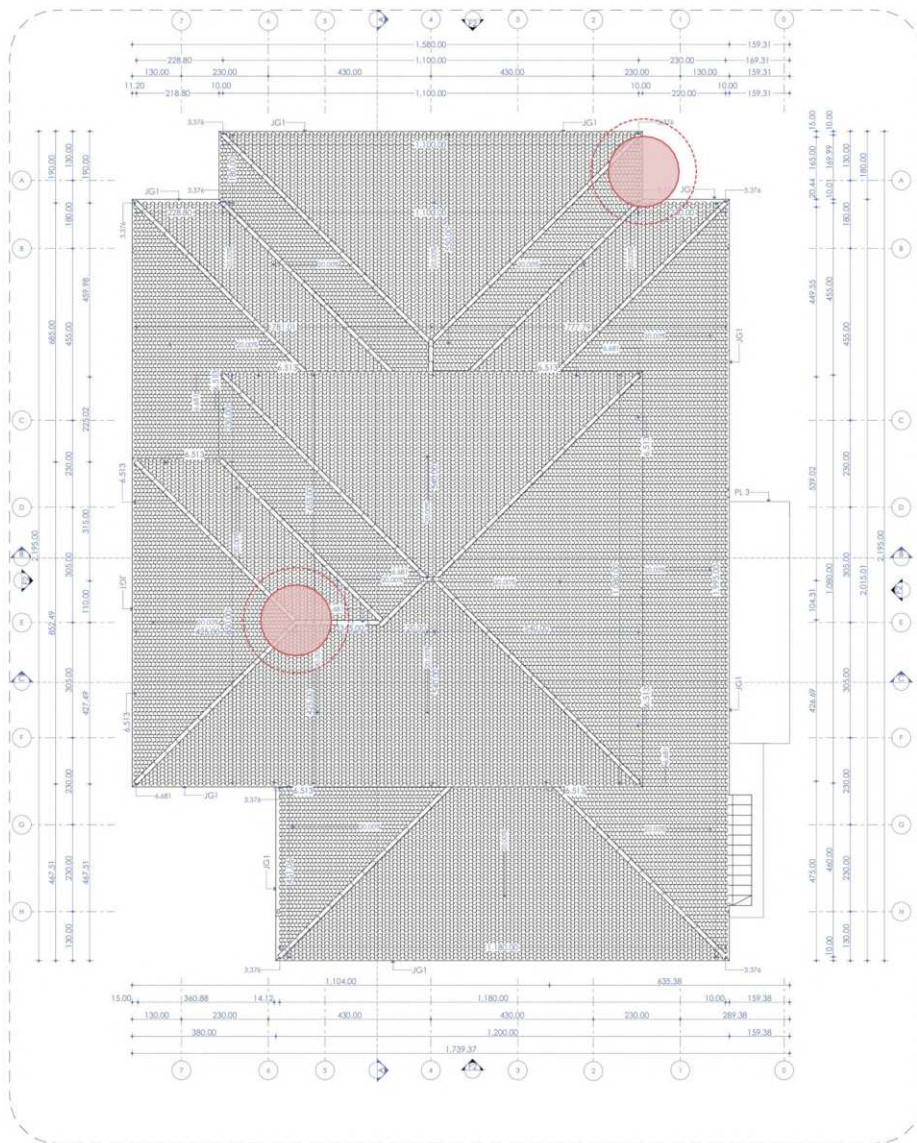


AXO ACOPERIS 1:50

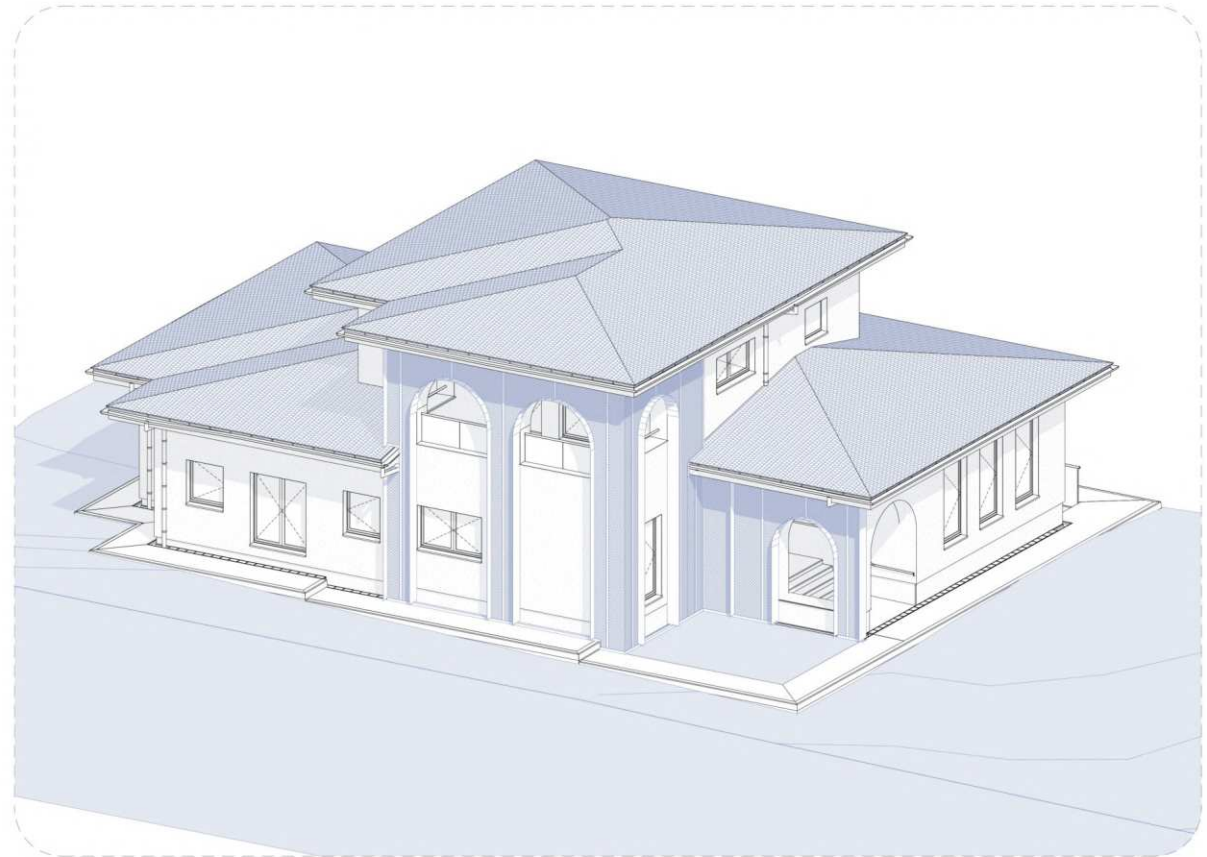

D.A.01 DETALIU 1:10


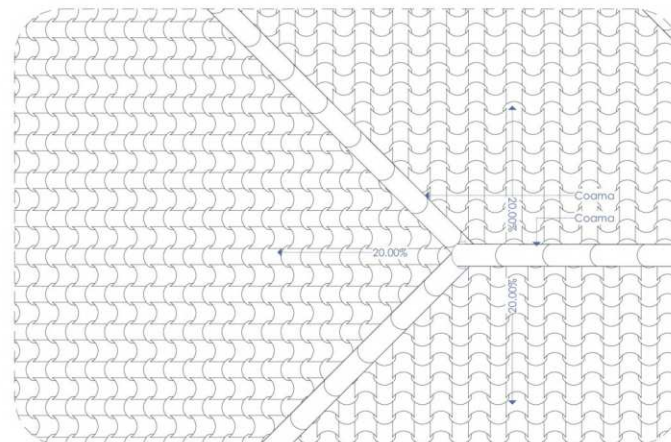


D.A.02 DETALIU 1:10

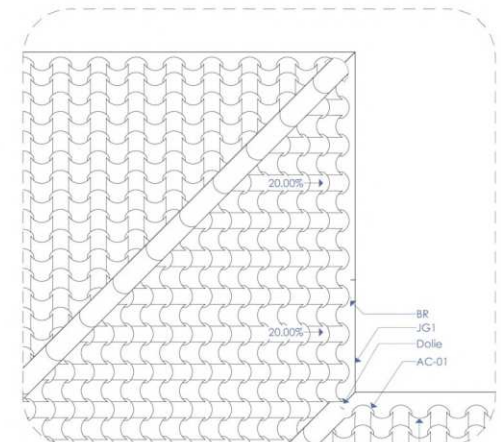

SECTIUNE A

1:50

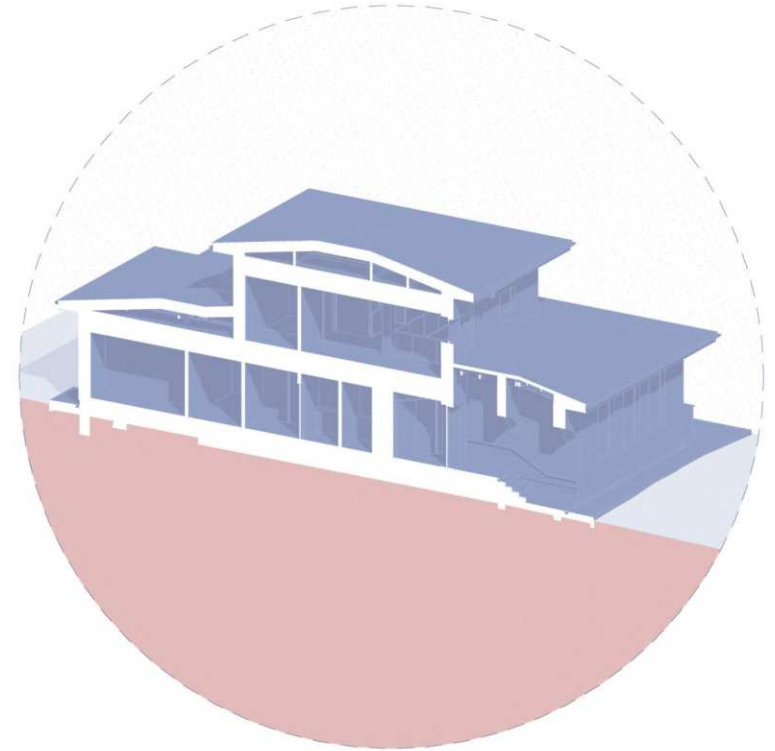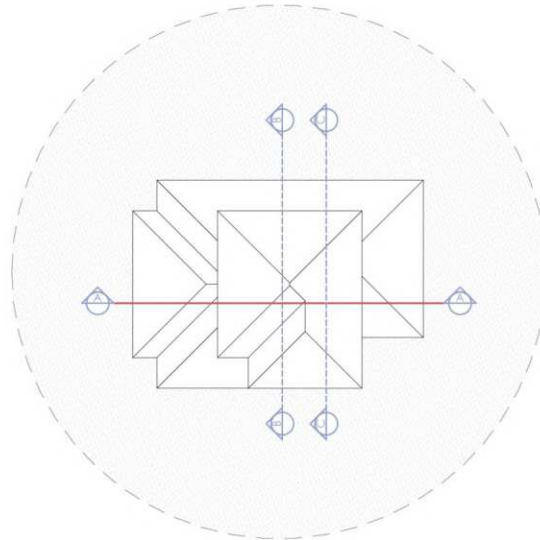

PL-4	
Tencuiala pe baza de ipsos	0.50 cm
Gips carton	1.25 cm
Vata minerala	10.00 cm
Strat aer neventilat	67.50 cm
Lemn de inchidere pod	2.50 cm

PL-1	
Pământ compactat	25.00 cm
Pietris	15.00 cm
Nisip	10.00 cm
Membrana hidroizolanta	0.25 cm
Poliiziren expandat	15.00 cm
Beton armat monolit	15.00 cm
Sapa de ciment	5.00 cm
Strat aer neventilat	5.00 cm
Beton usor	3.50 cm
Parchet lamelar	1.50 cm


PI	
Strat de vopsea interior	0.25 cm
Tencuiala pe baza de ipsos	0.50 cm
Gips carton	1.25 cm
Vata minerala - interior	10.00 cm
Strat aer neventilat	10.00 cm
Vata minerala - interior	10.00 cm
Gips carton	1.25 cm
Tencuiala pe baza de ipsos	0.50 cm
Strat de vopsea interior	0.25 cm

PE3	
Strat de vopsea interior	0.25 cm
Tencuiala pe baza de ipsos	0.50 cm
Gips carton	1.25 cm
Adeziv	1.00 cm
Caramida cu goluri verticale	30.00 cm
Adeziv	0.30 cm
Vata minerala	15.00 cm
Masa de spatu	0.10 cm
Plasa de armare	0.10 cm
Tencuiala silconica	1.25 cm
Strat de vopsea exterior	0.25 cm

AC1	
Folie anticondens	0.25 cm
Placaj OSB	1.25 cm
Vata minerala	15.00 cm
Vata minerala	10.00 cm
Astereala	2.00 cm
Membrana hidroizolanta	0.25 cm
Spatiu sipci	5.00 cm
Spatiu sipci	3.00 cm

TR 1	
Pietris	10.00 cm
Nisip	5.00 cm
Beton armat monolit	15.00 cm
Sapa de ciment	5.00 cm

PL1	
Tencuiala pe baza de ipsos	0.50 cm
Gips carton	1.25 cm
Vata minerala	10.00 cm
Strat aer neventilat	46.50 cm
Beton armat monolit	15.00 cm

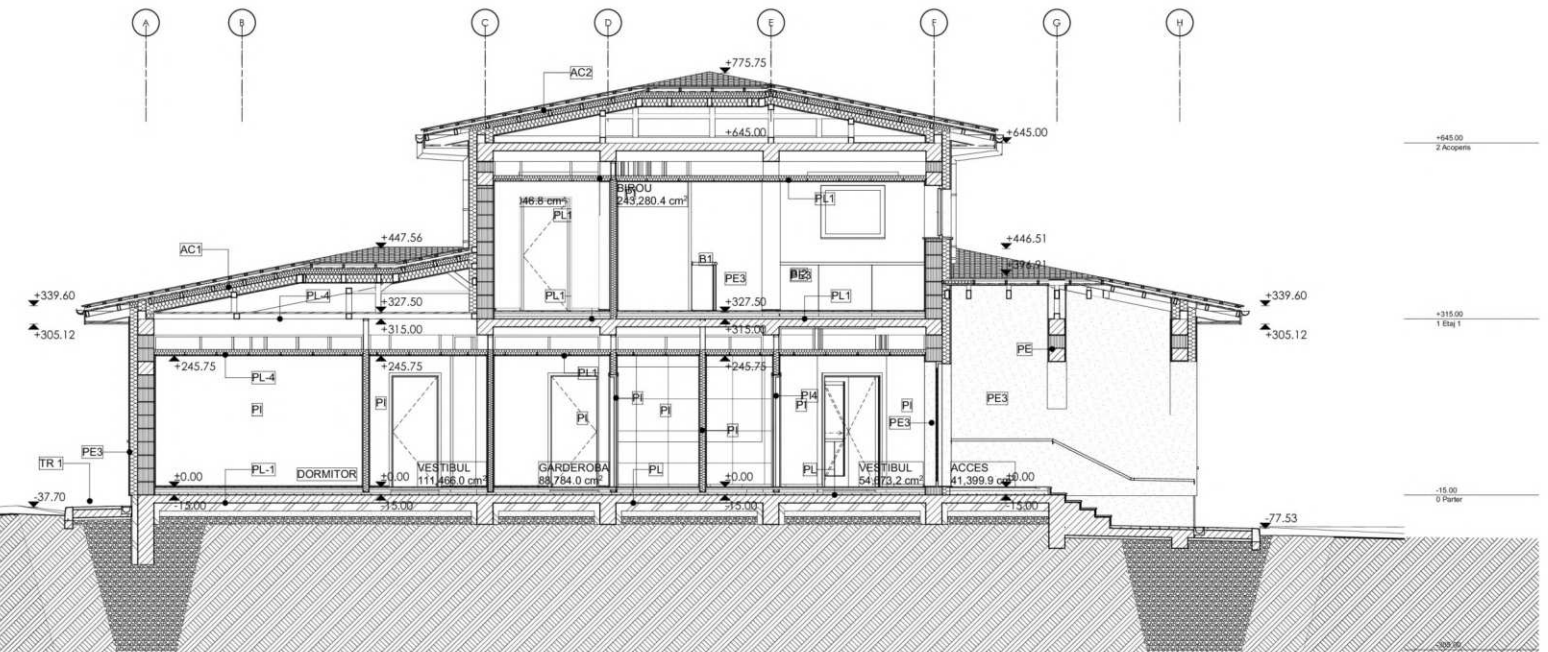

EXTERIOR

AC1	
Spatiu sipci	3.0 cm
Spatiu contrasipci	5.0 cm
Membrana hidroizolanta	0.3 cm
Astereala	2.0 cm

CO, Cosoroaba, Cherestea,
0.150x0.150

PA1, Pana, Lemn, 0.100x0.050

CR, Caprior, Cherestea
Nerindelut, 0.636x0.080

JG1, Jgheab,
0.075x0.150

+339.6, +384.6

+321.9, +366.9

+305.1, +350.1

PZ, Pazie, Lemn, 0.250x0.020

SG1, Sageac, Lemn, 0.020

GR, Grinda, Beton armat monolit
0.300x0.300




BU, Buiandrug, Beton armat monolit,
1.250x0.300

UI2, Gol cu arcada, 3.500x2.230



PE3

Strat de vopsea exterior	0.3 cm
Tencuiala siliconica	1.3 cm
Plasa de armare	0.1 cm
Masa de spaclu	0.1 cm
Vata minerala	15.0 cm
Adeziv	0.3 cm
Caramida cu goluri verticale	30.0 cm
Adeziv	0.3 cm
Gipscarton	1.3 cm
Plasa de armare	0.1 cm
Tencuiala siliconica	1.3 cm
Strat de vopsea exterior	0.2 cm

DETALIU A-0 1:10

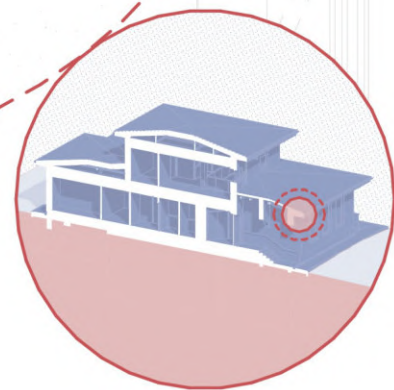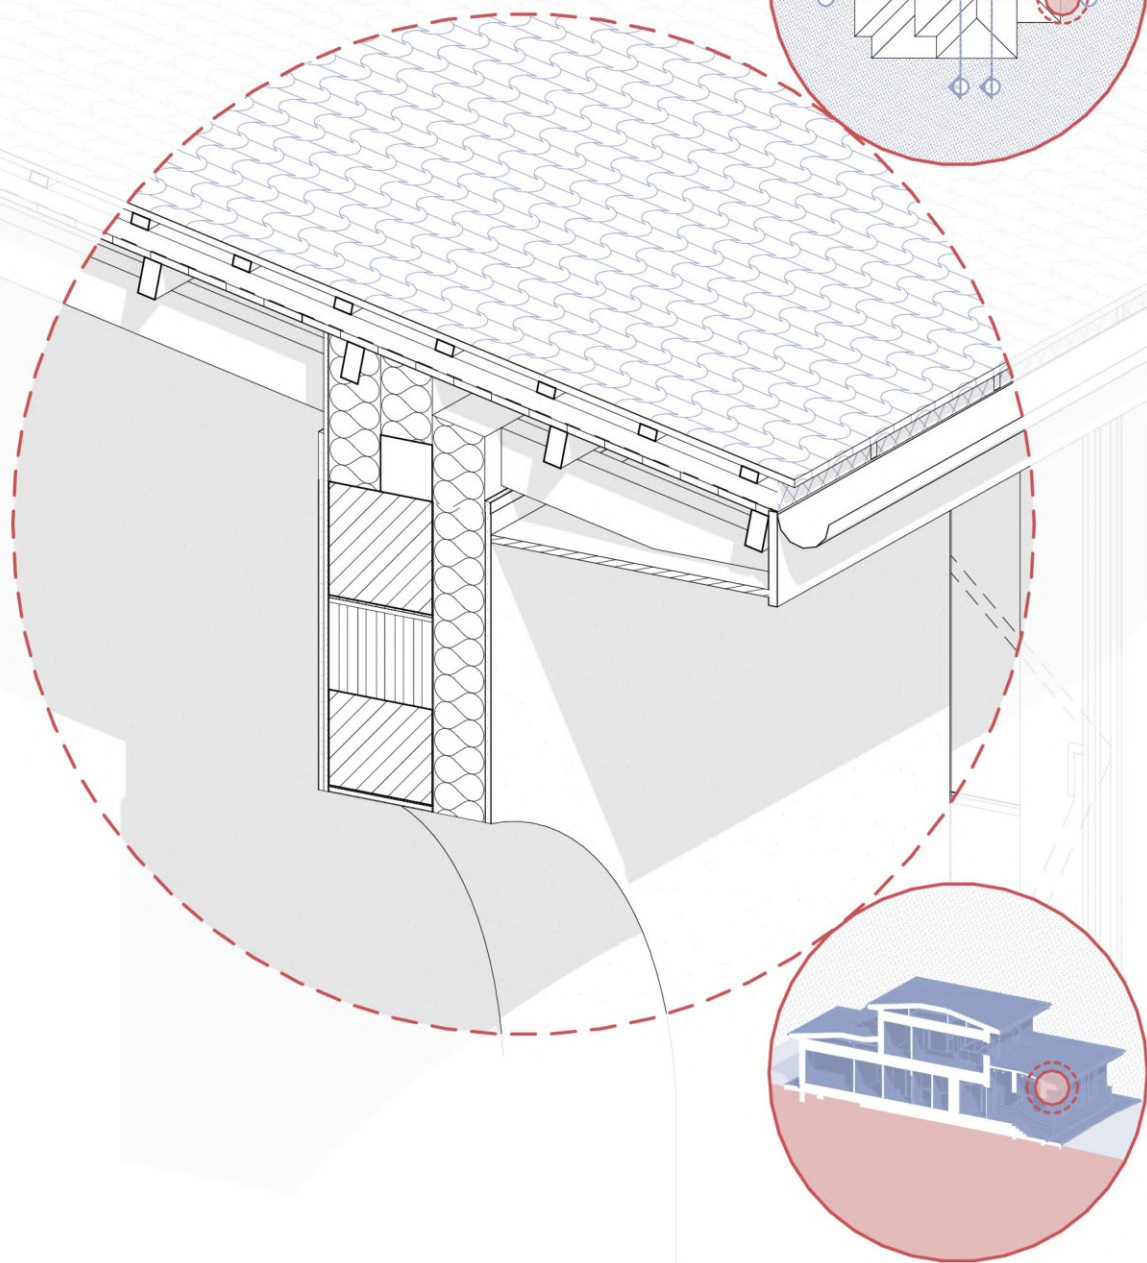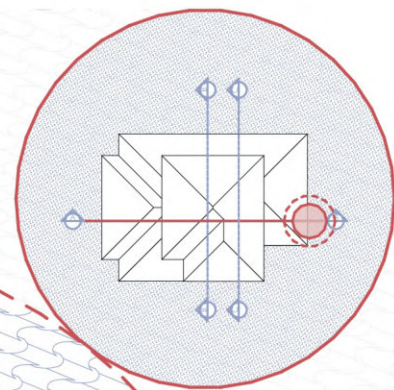

DETALIU A-1 1:10

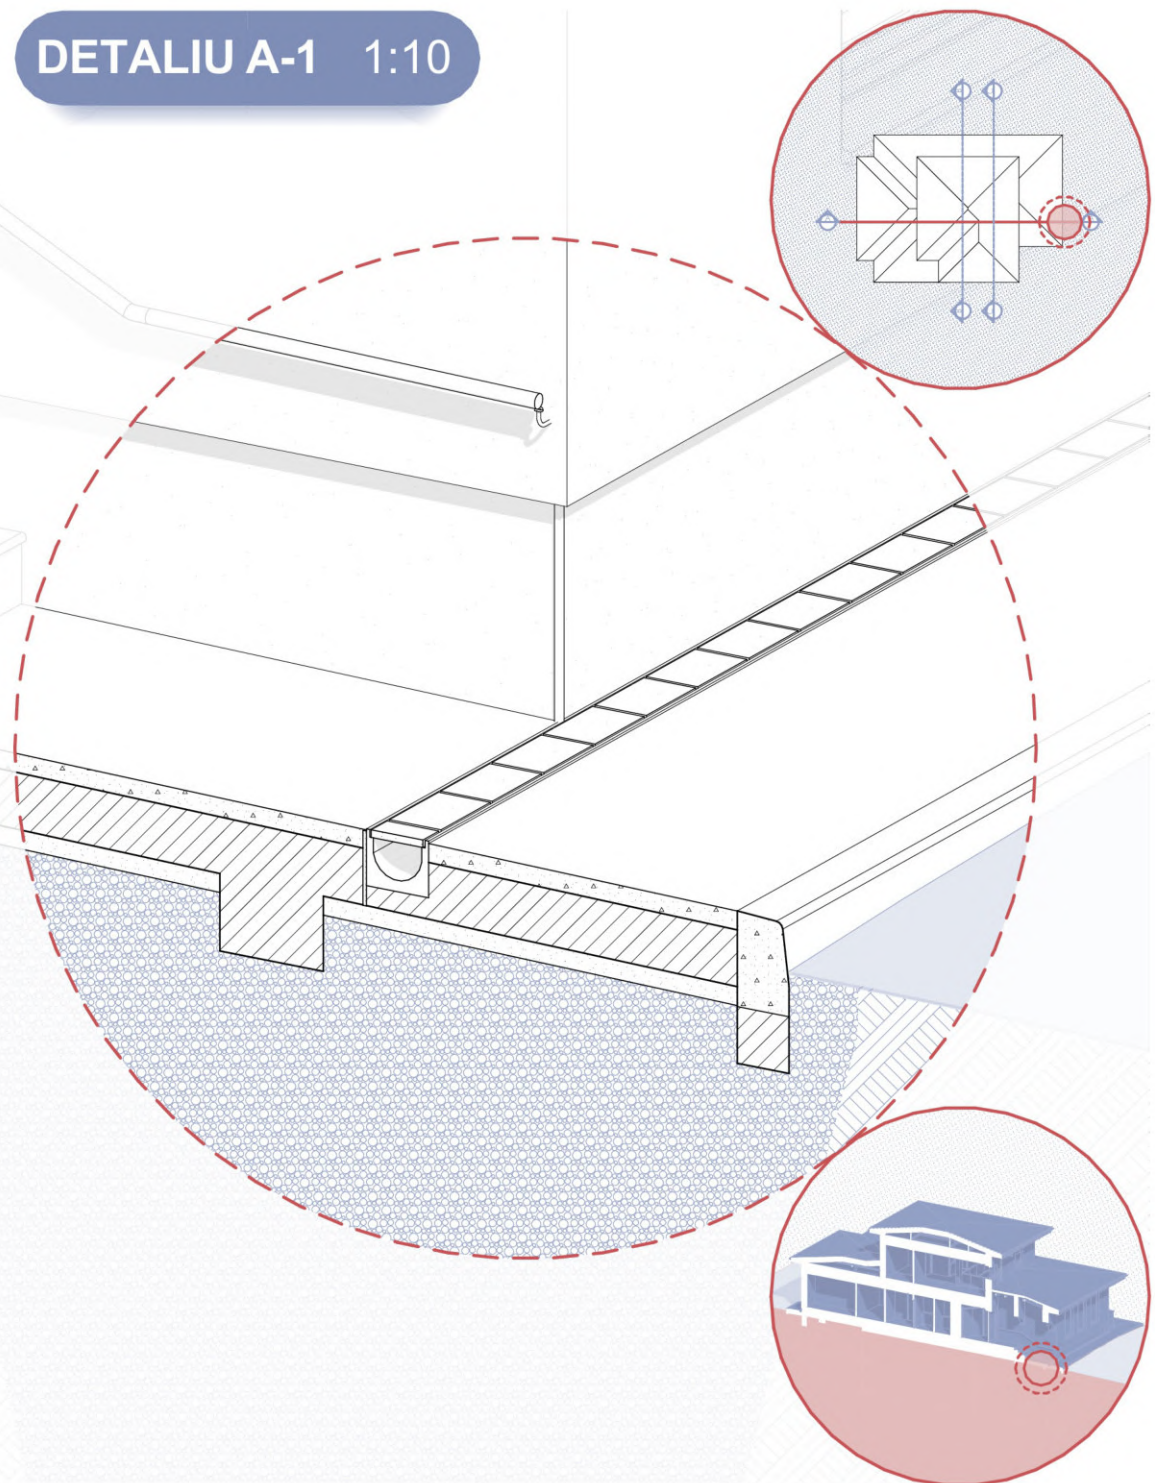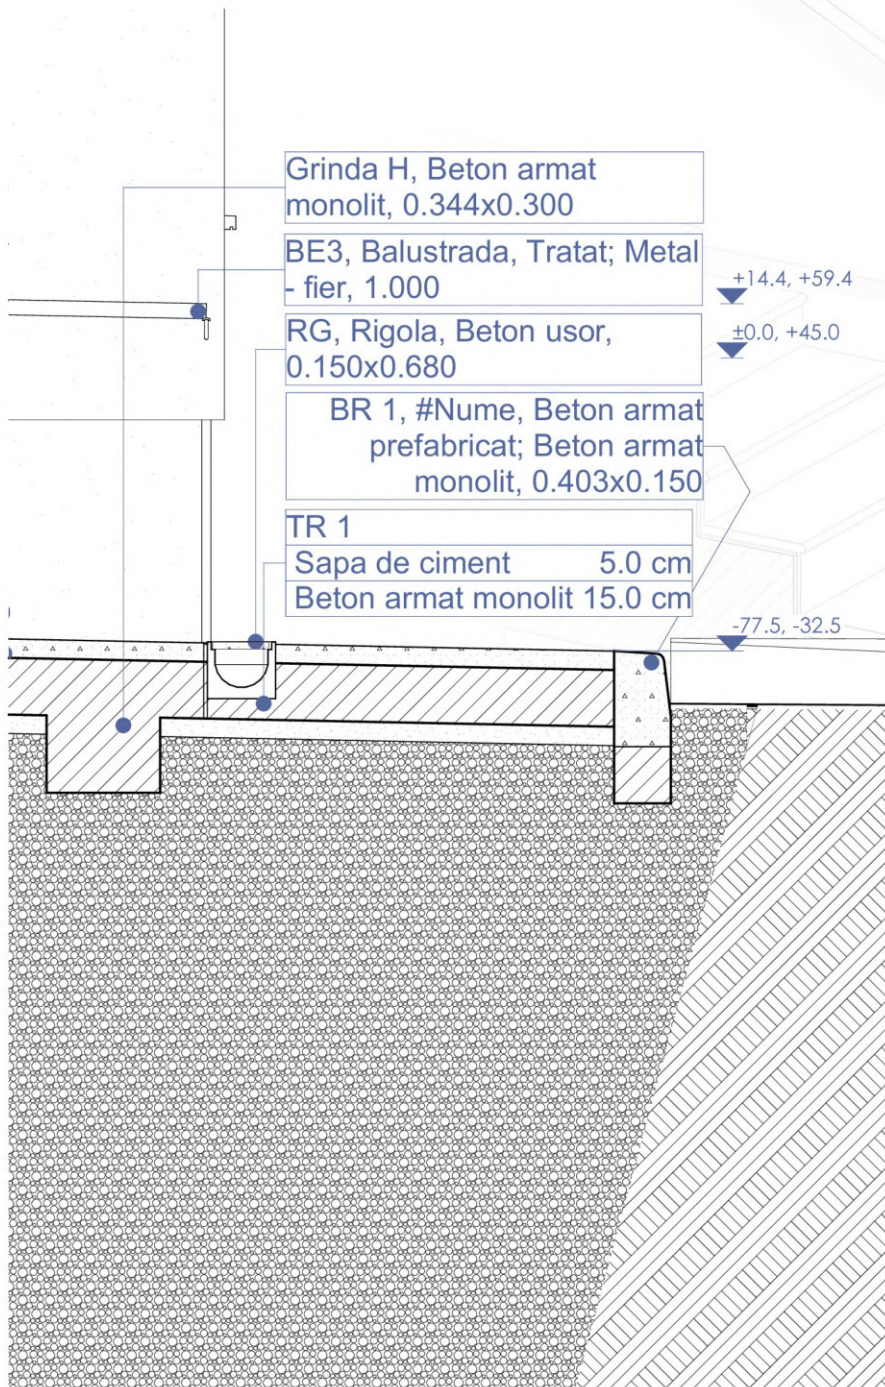

EXTERIOR

DETALIU A-2 1:10

AC1

Spatiu sipci	3.0 cm
Spatiu contrasipci	5.0 cm
Membrana hidroizolanta	0.3 cm
Astereala	2.0 cm

PA1, Pana, Lemn 0.100x0.050

CS, Contrasipca, Lemn 0.050x0.030

CR, Caprior, Cherestea 0.786x0.080

GR, Grinda, Beton armat monolit 0.300x0.300

PP, Pop, Lemn 0.450x0.100

CO, Cosoroaba, Cherestea
Nerindelut 0.100x0.100


BU, Buiandrug, Beton armat monolit,
1.250x0.300


PE

Strat de vopsea exterior	0.2 cm
Tencuiala siliconica	1.3 cm
Plasa de armare	0.1 cm
Gipscarton	1.3 cm
Adeziv	0.3 cm
Caramida cu goluri verticale 30.0 cm	
Adeziv	0.3 cm
Gipscarton	1.3 cm
Plasa de armare	0.1 cm
Tencuiala siliconica	1.3 cm
Strat de vopsea exterior	0.2 cm


UI2, Gol cu arcada, 2.650x2.250

BE3, Balustrada, Tratata; Metal - fier,
1.000

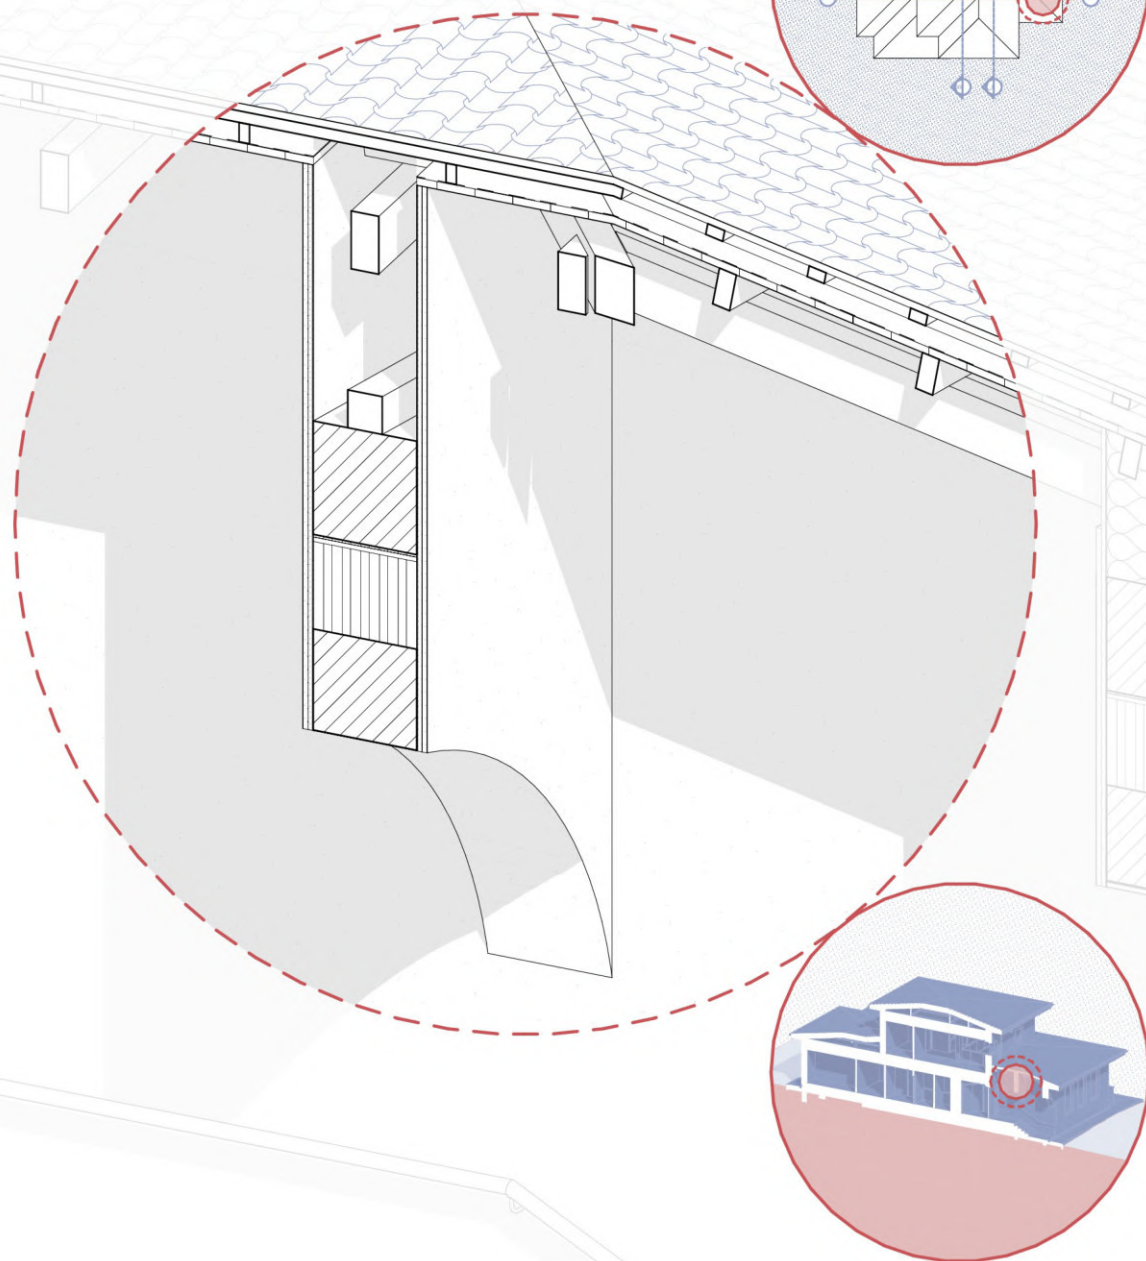

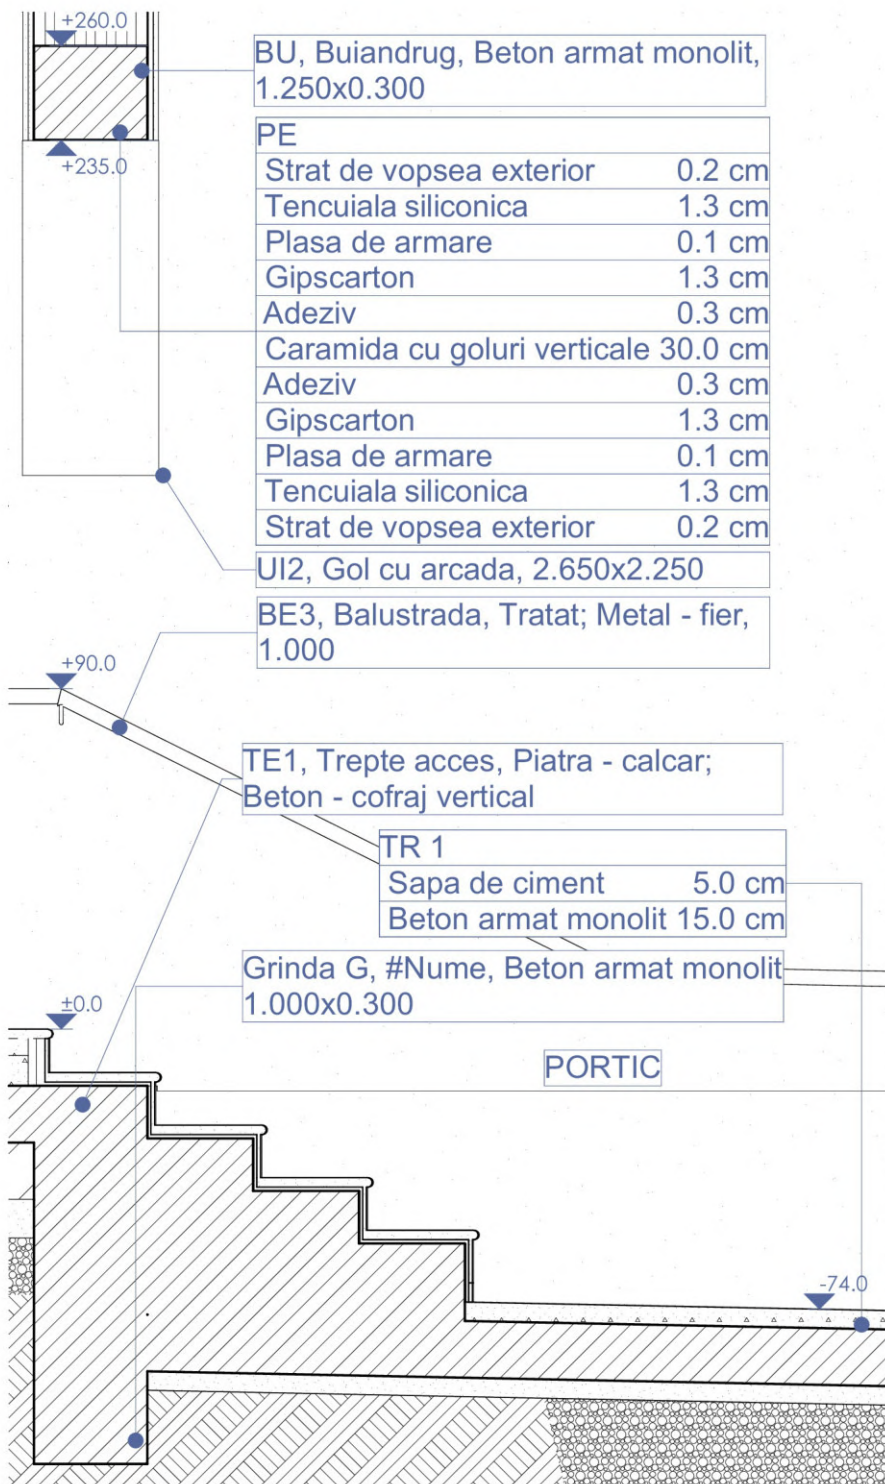

DETALIU A-3 1:10

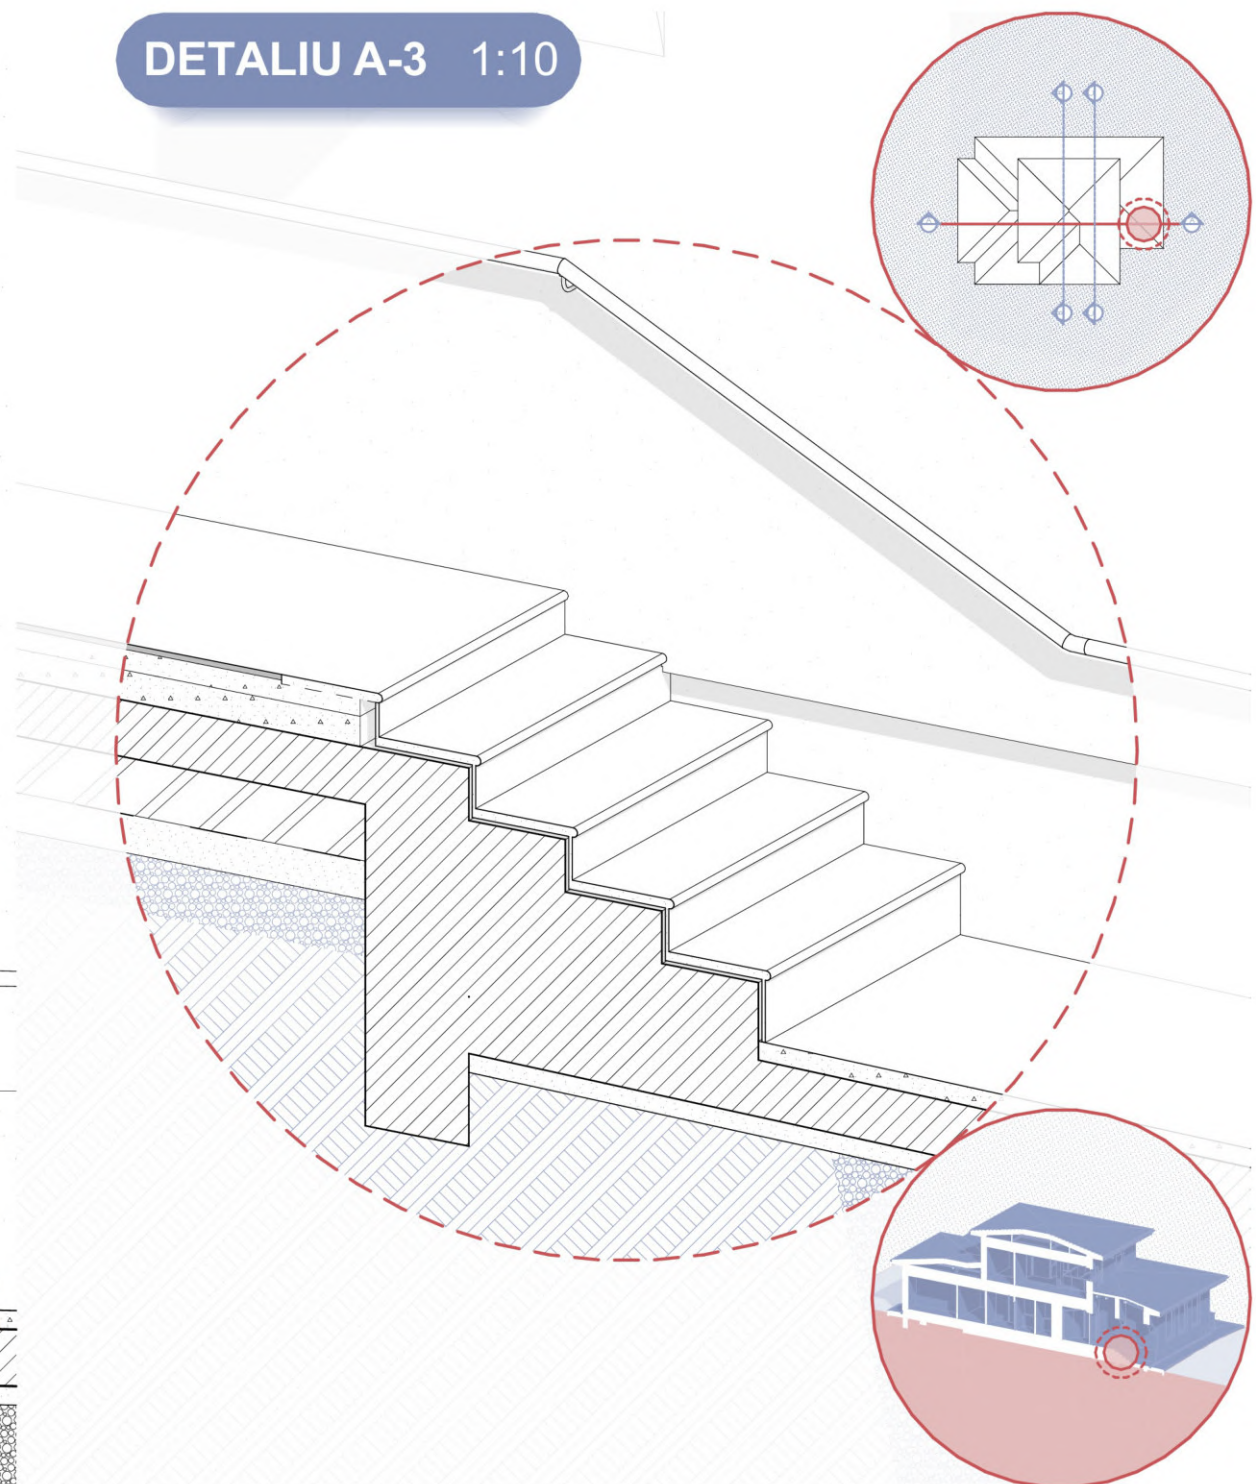

EXTERIOR

CS-1,
Contrasipca,
0.050x0.030

AC2

Spatiu sipci	3.0 cm
Spatiu sipci	5.0 cm
Membrana hidroizolanta	0.3 cm
Astereala	2.0 cm
Vata minerala	10.0 cm
Vata minerala	15.0 cm
Placaj OSB	1.3 cm
Folie anticondens	0.3 cm

CR1, Caprior,
0.913x0.080

PA1, Pana,
0.100x0.050

JG1, Jgheab,
0.075x0.150

BL4, Burlan,
1.988x0.100

PZ5, Pазie, Lemn,
0.250x0.020

CO1, Cosoroaba, #Building
Material, 0.150x0.150

Grinda, #Nume, Beton armat
monolit 0.350x0.300

Buiandrug, #Nume, Beton armat
monolit, 0.250x0.300

F5, Fereastrа, 2.000x1.000x0.500

PE3

Strat de vopsea exterior	0.3 cm
Tencuiala siliconica	1.3 cm
Plasa de armare	0.1 cm
Masa de spaclu	0.1 cm
Vata minerala	15.0 cm
Adeziv	0.3 cm
Caramida cu goluri verticale	30.0 cm
Adeziv	1.0 cm
Gips carton	1.3 cm
Tencuiala pe baza de ipsos	0.5 cm
Strat de vopsea interior	0.3 cm

+467.5

+610.9

+622.1




+634.7

+644.9



+665.7

BIROU SP. TEHNIC


DETALIU A-4 1:10

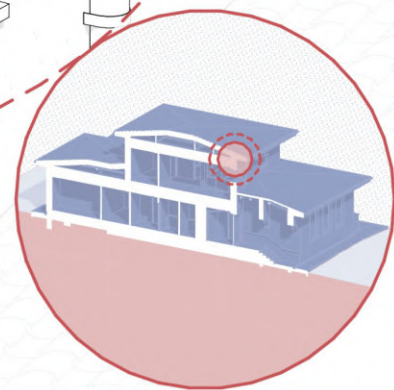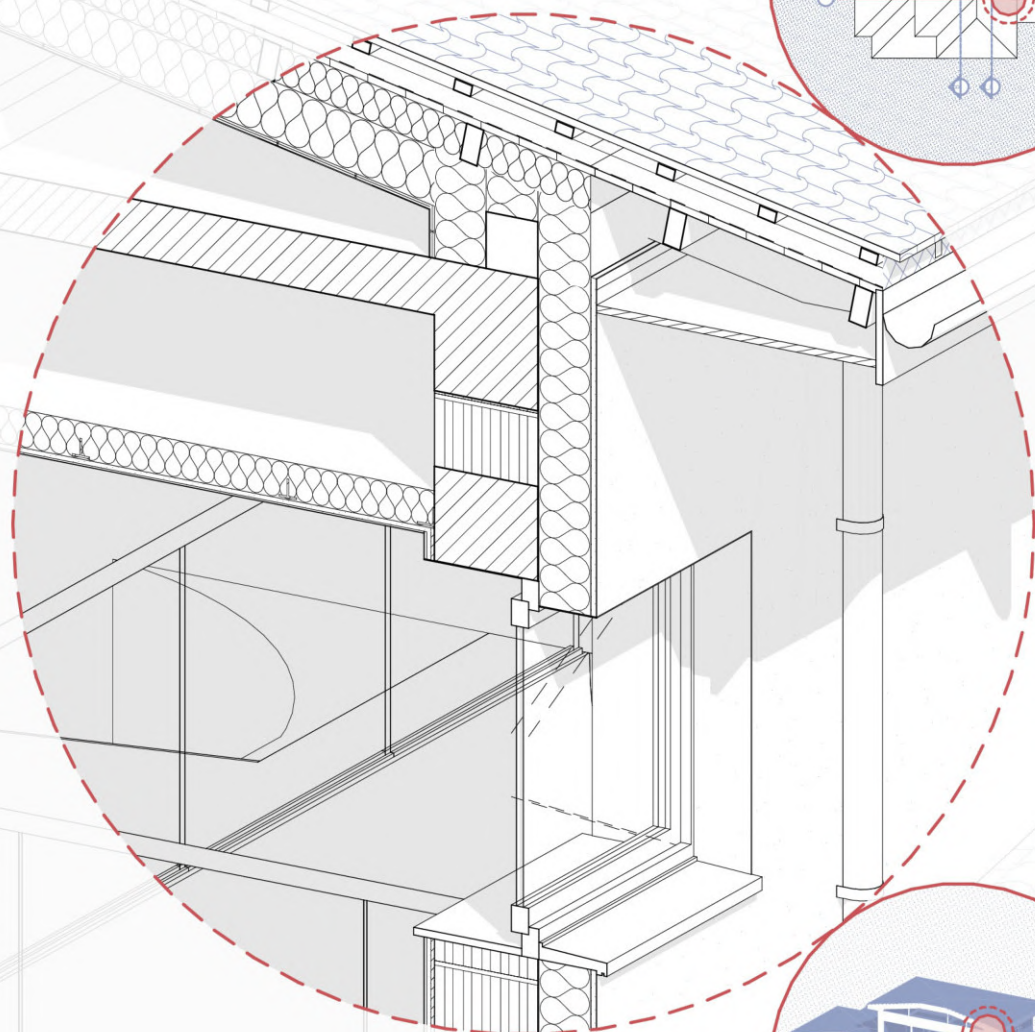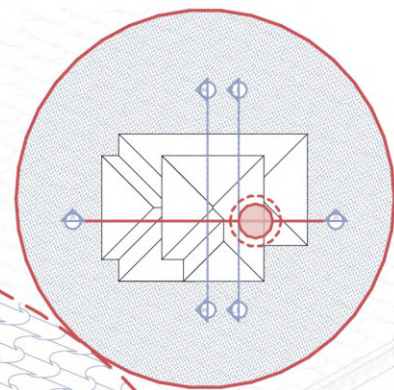



DETALIU A-5 1:10

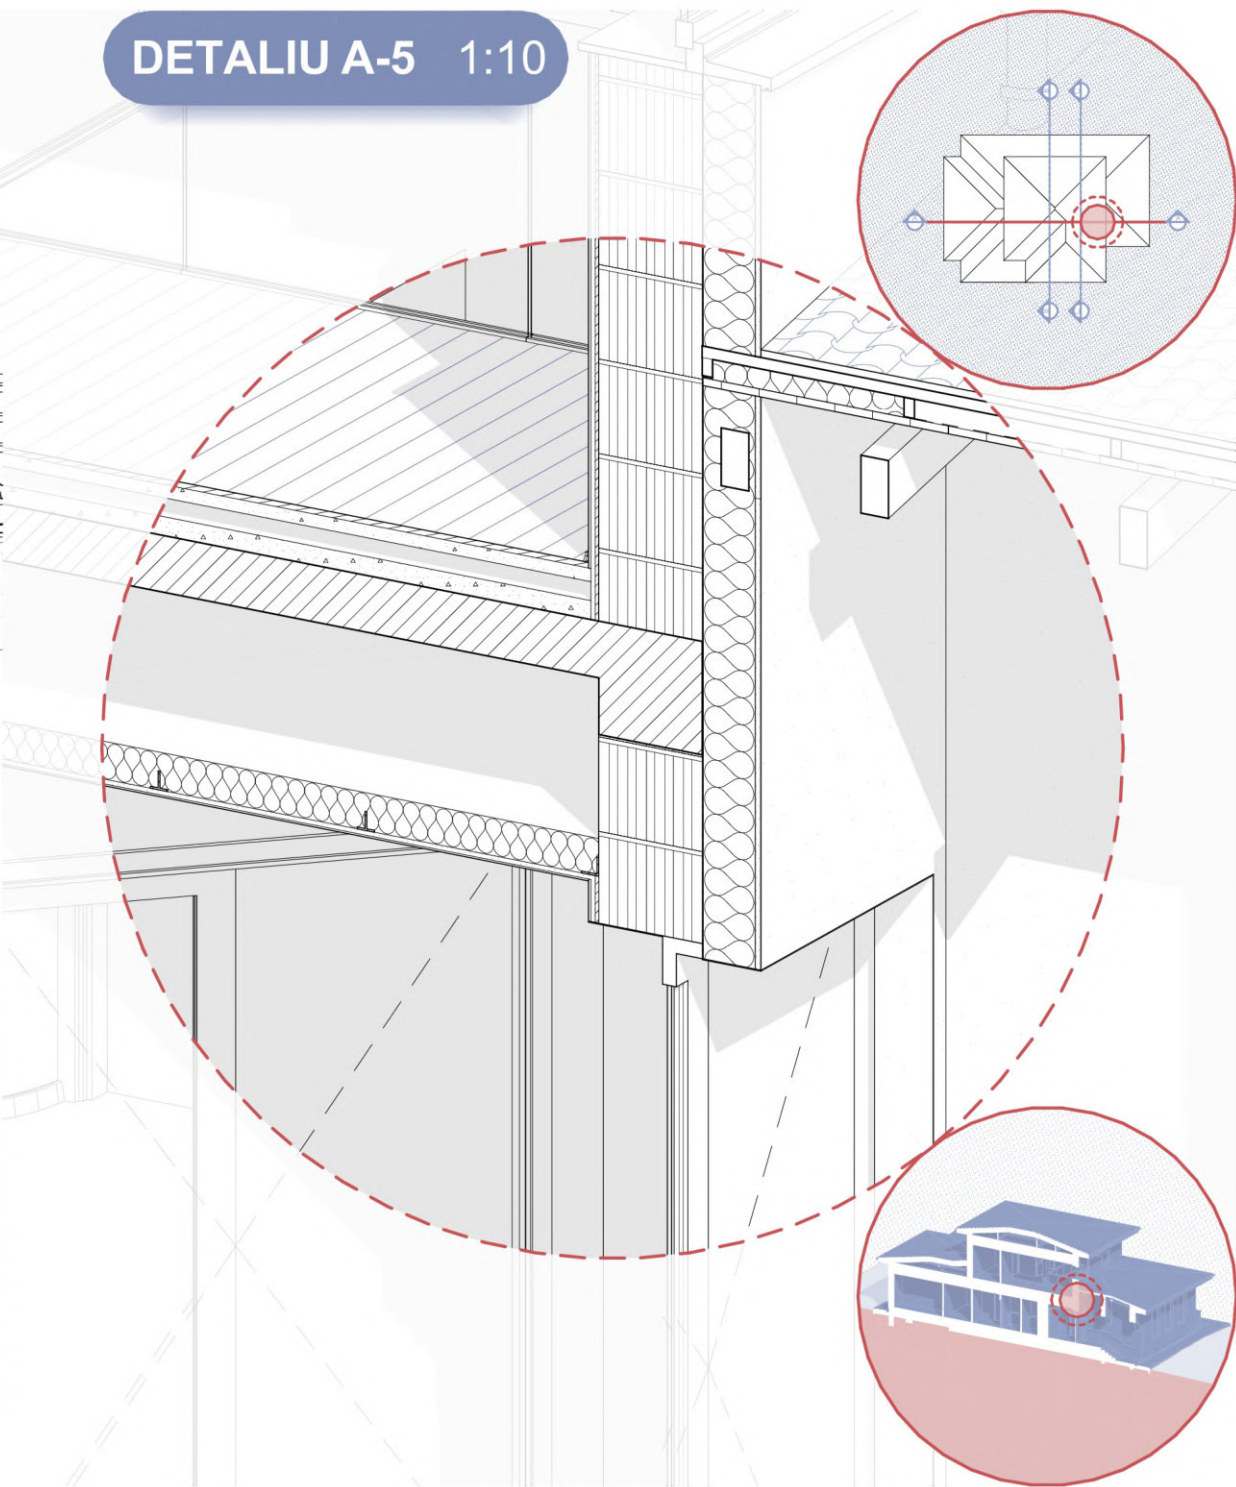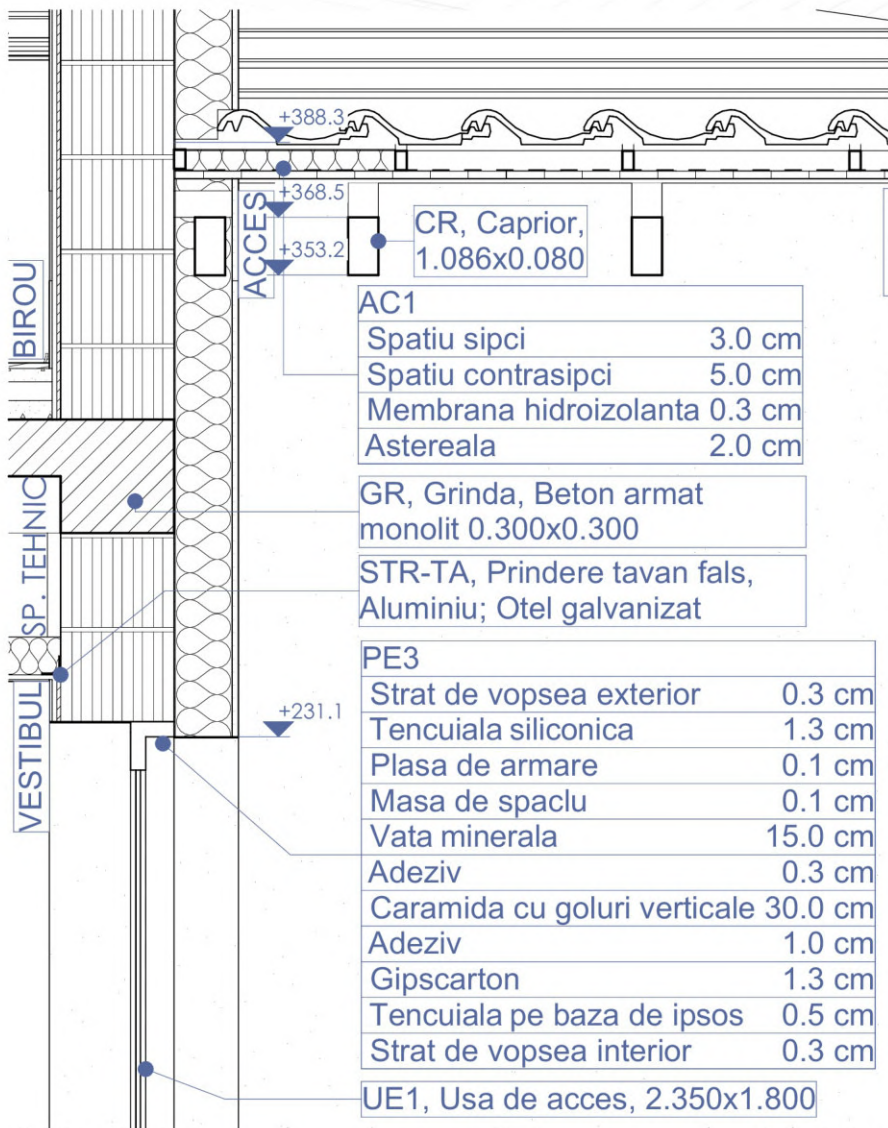

DETALIU A-6 1:10

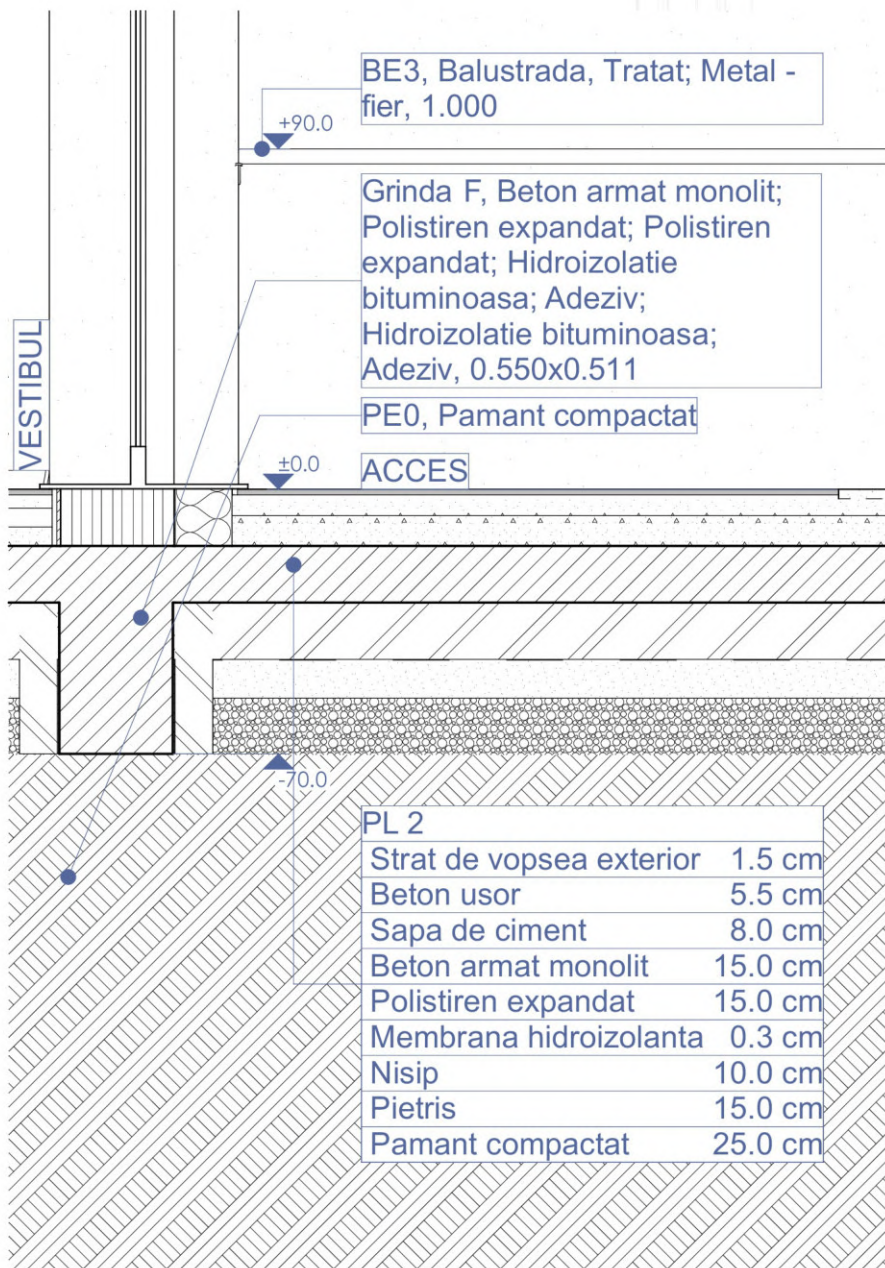

DETALIU A-7 1:10

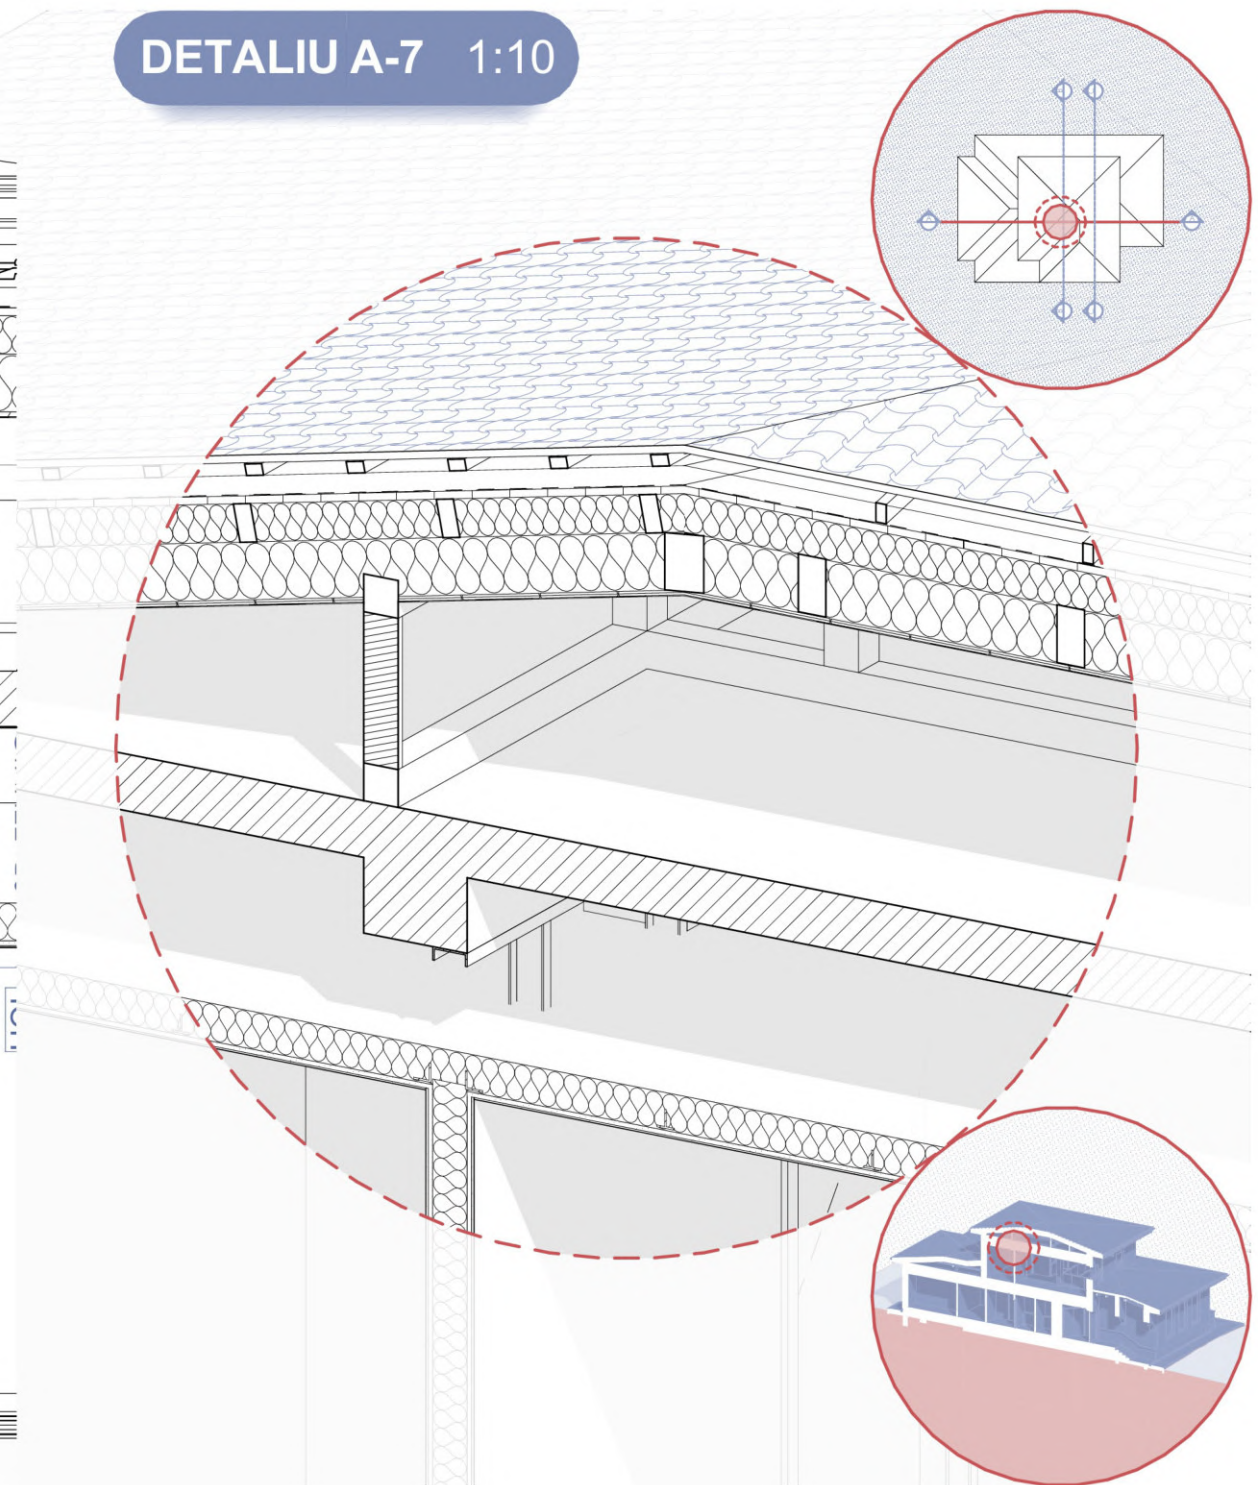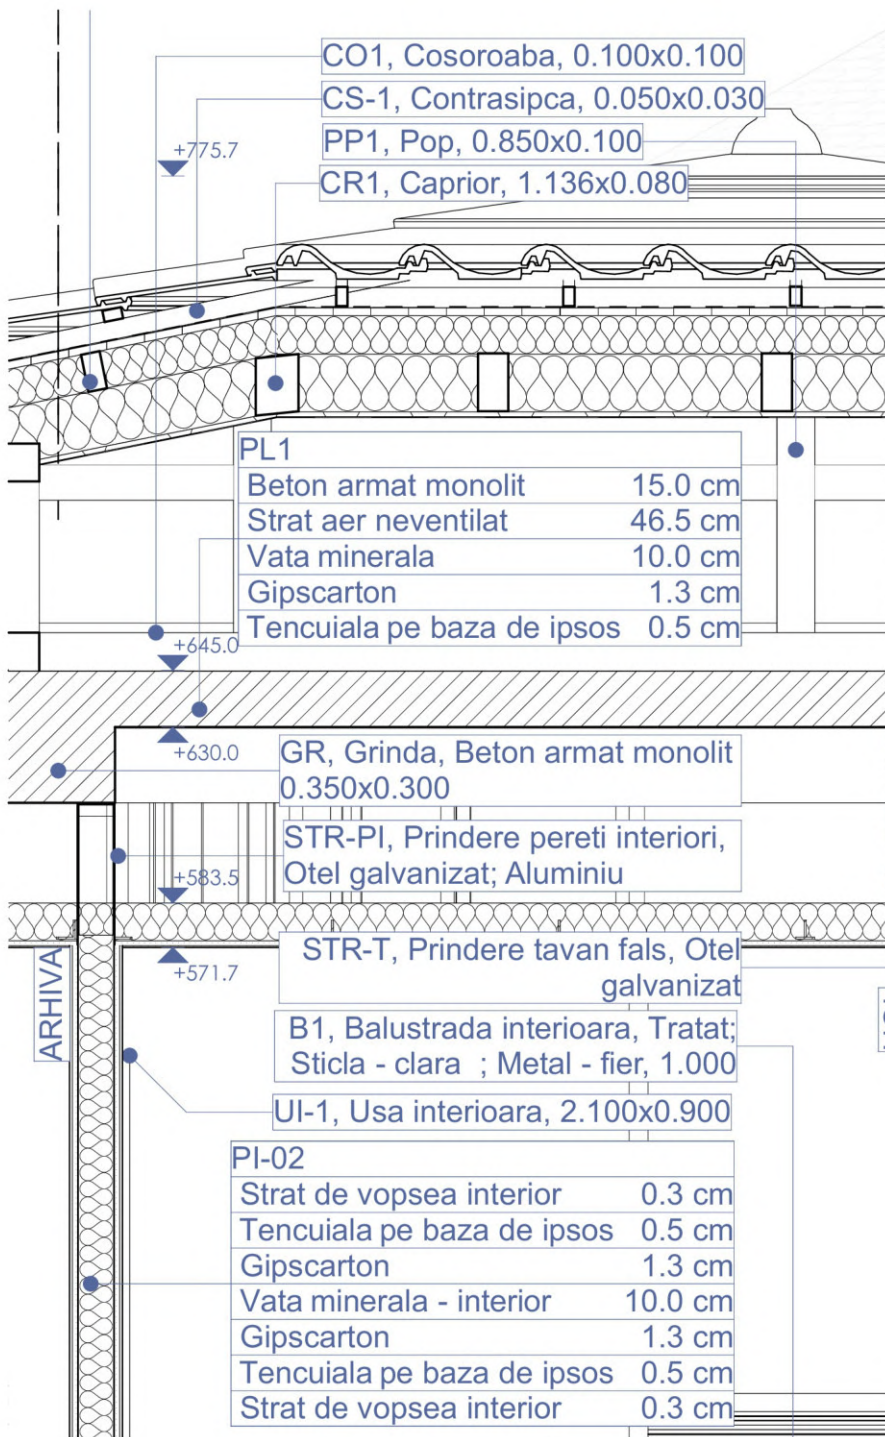

DETALIU A-8 1:10

PI-02

Strat de vopsea interior	0.3 cm
Tencuiala pe baza de ipsos	0.5 cm
Gipscarton	1.3 cm
Vata minerala - interior	10.0 cm
Gipscarton	1.3 cm
Tencuiala pe baza de ipsos	0.5 cm
Strat de vopsea interior	0.3 cm

PL1

Parchet lamelar	1.5 cm
Beton usor	3.5 cm
Strat aer neventilat	5.0 cm
Sapa de ciment	5.0 cm
Beton armat monolit	15.0 cm
Strat aer ventilat	42.5 cm
Vata minerala	10.0 cm
Gipscarton	1.3 cm
Tencuiala pe baza de ipsos	0.5 cm

+327.5

+315.0

+300.0

STR-TA, Prindere tavan
fals, Otel galvanizat

+257.5

+245.8

PL1



Parchet lamelar	1.5 cm
Beton usor	3.5 cm
Strat aer neventilat	5.0 cm
Sapa de ciment	5.0 cm
Beton armat monolit	15.0 cm
Strat aer ventilat	42.5 cm
Vata minerala	10.0 cm
Gipscarton	1.3 cm
Tencuiala pe baza de ipsos	0.5 cm

ARHIVA

GARDEROBA

SP

BAIE

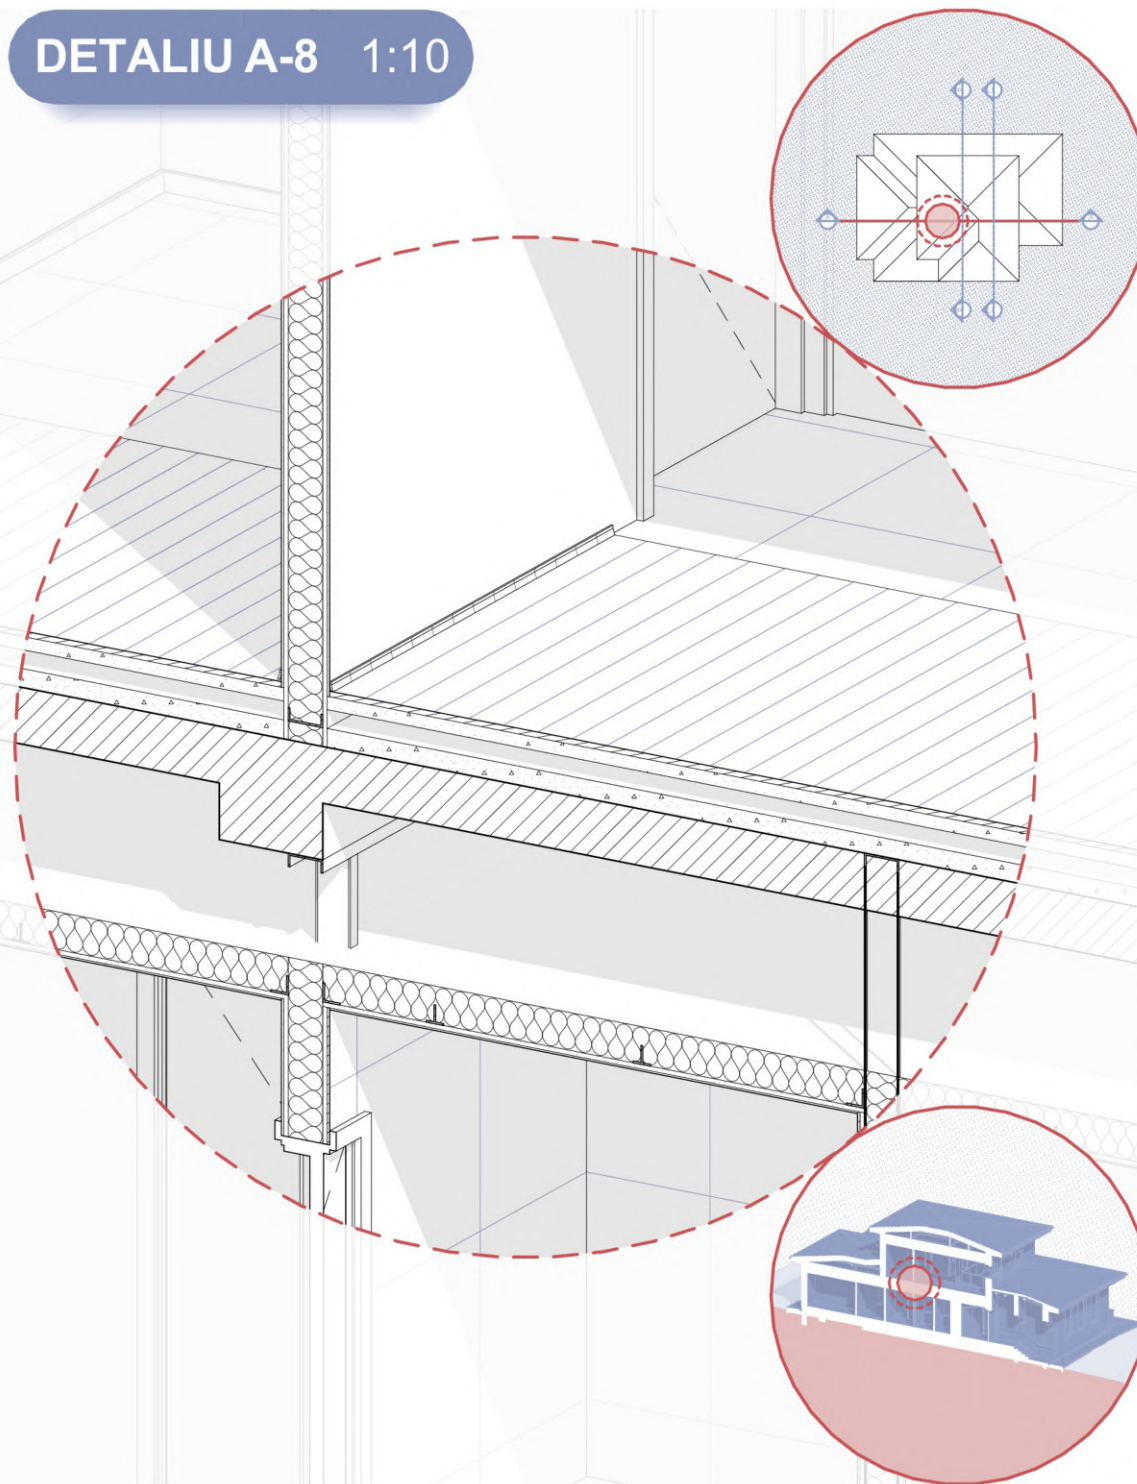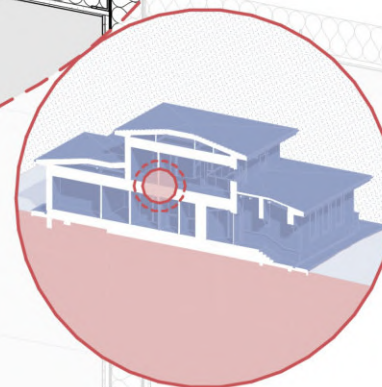


The drawing shows a cross-section of a building facade with three main vertical sections: **GARDEROBA** (left), **PL1** (middle), and **PI** (right). The **PL1** section is the central focus, showing a multi-layered wall structure. The **PI** section is to its right, and the **GARDEROBA** section is to its left. The drawing includes elevation markers: **+245.8** at the top, **+0.0** at the base of the main wall, and **-15.0** at the base of the foundation. The **PL1** section is labeled with **UI4, Usa interioara, 2.100x0.800**. The **PI** section is labeled with **STR-PI, #Nume, Otel galvanizat; Aluminiu**. The **GARDEROBA** section is labeled with **PL, Plinta de gresie, Aluminiu**. The drawing also shows a **BAIE** (window) on the right side of the **PI** section.

Material	Thickness
Parchet lamelar	1.5 cm
Beton usor	3.5 cm
Strat aer neventilat	5.0 cm
Sapa de ciment	5.0 cm
Beton armat monolit	15.0 cm
Strat aer ventilat	42.5 cm
Vata minerala	10.0 cm
Gipscarton	1.3 cm
Tencuiala pe baza de ipsos	0.5 cm




Material	Thickness
Faianta	0.3 cm
Adeziv	0.5 cm
Gipscarton rezistent la umezeala	1.3 cm
Vata minerala - interior	10.0 cm
Gipscarton rezistent la umezeala	1.3 cm
Adeziv	0.5 cm
Faianta	0.3 cm

Material	Thickness
Gresie	1.5 cm
Beton usor	3.5 cm
Strat aer neventilat	5.0 cm
Sapa de ciment	5.0 cm
Beton armat monolit	15.0 cm
Polistiren expandat	15.0 cm
Membrana hidroizolanta	0.3 cm
Nisip	10.0 cm
Pietris	15.0 cm
Pamant compactat	25.0 cm

DETALIU A-9 1:10

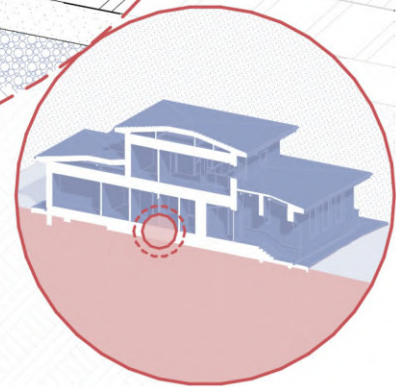

DETALIU A-10 1:10

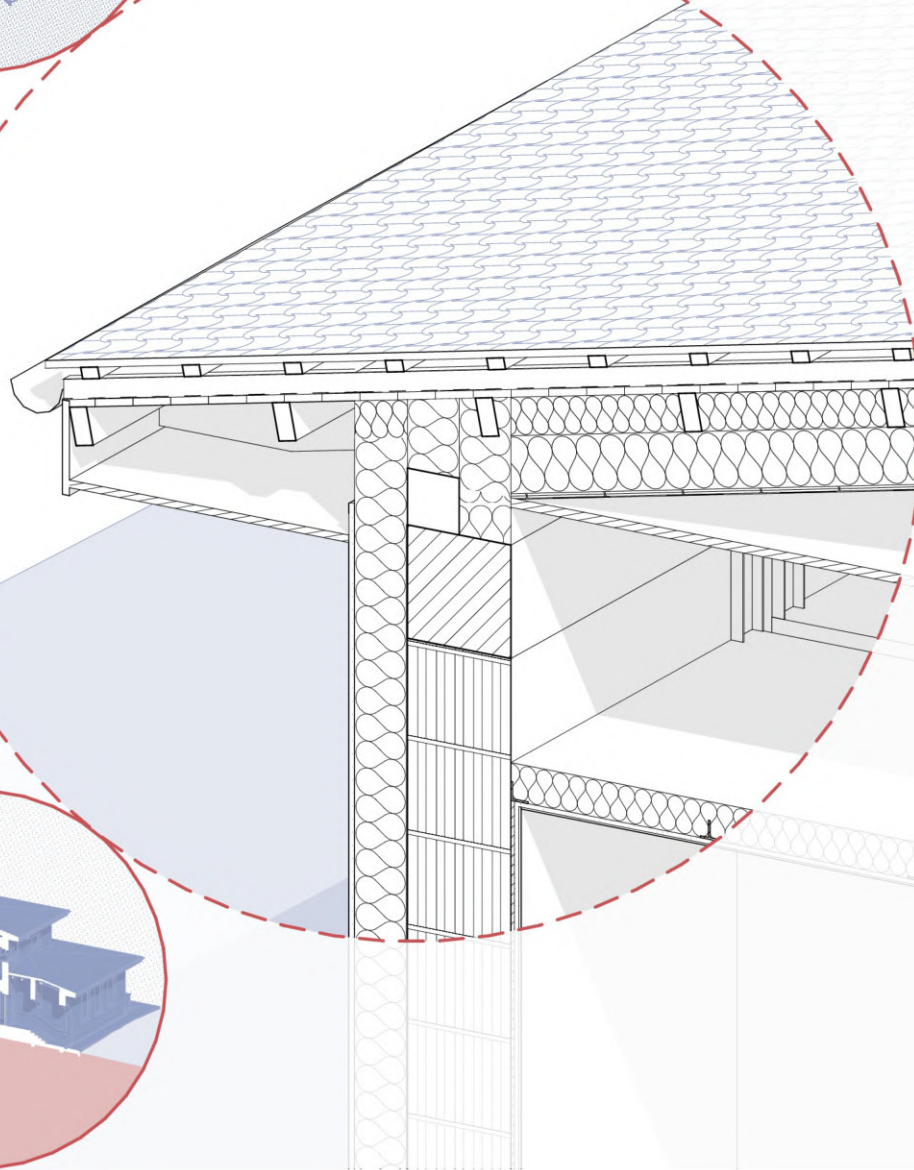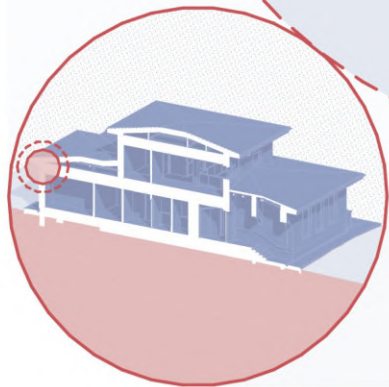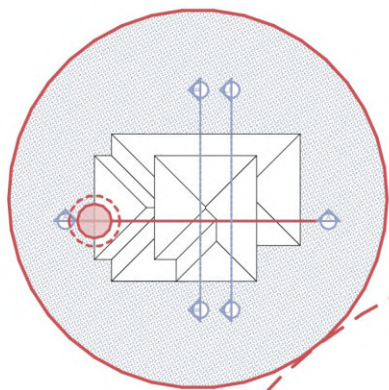

PA1, Pana, Lemn,
0.100x0.050

JG1, Jgheab, 0.075
SG1, Sageac, Lemn,
0.020

AC1	
Spatiu sipci	3.0 cm
Spatiu contrasipci	5.0 cm
Membrana hidroizolanta	0.3 cm
Astereala	2.0 cm

PE3	
Strat de vopsea exterior	0.3 cm
Tencuiala siliconica	1.3 cm
Plasa de armare	0.1 cm
Masa de spaclu	0.1 cm
Vata minerala	15.0 cm
Adeziv	0.3 cm
Caramida cu goluri verticale	30.0 cm
Adeziv	1.0 cm
Gips carton	1.3 cm

SP. TEHNIC

DORMITOR

DETALIU A-11 1:10

AC1	
Spatiu sipci	3.0 cm
Spatiu sipci	5.0 cm
Membrana hidroizolanta	0.3 cm
Astereala	2.0 cm
Vata minerala	10.0 cm
Vata minerala	15.0 cm
Placaj OSB	1.3 cm
Folie anticondens	0.3 cm

ARHIVA

PE3

Strat de vopsea exterior	0.3 cm
Tencuiala siliconica	1.3 cm
Plasa de armare	0.1 cm
Masa de spaclu	0.1 cm
Vata minerala	15.0 cm
Adeziv	0.3 cm
Caramida cu goluri verticale	30.0 cm
Adeziv	1.0 cm
Gipscarton	1.3 cm
Tencuiala pe baza de ipsos	0.5 cm
Strat de vopsea interior	0.3 cm

PL1

Parchet lamelar	1.5 cm
Beton usor	3.5 cm
Strat aer neventilat	5.0 cm
Sapa de ciment	5.0 cm
Beton armat monolit	15.0 cm
Strat aer ventilat	42.5 cm
Vata minerala	10.0 cm
Gipscarton	1.3 cm
Tencuiala pe baza de ipsos	0.5 cm


ARHIVA

SP. TEHNIC PC4


Lemn de inchidere pod	2.5 cm
Strat aer neventilat	67.5 cm
Vata minerala	10.0 cm
Gipscarton	1.3 cm
Tencuiala pe baza de ipsos	0.5 cm

SP. TEHNIC

VESTIBUL

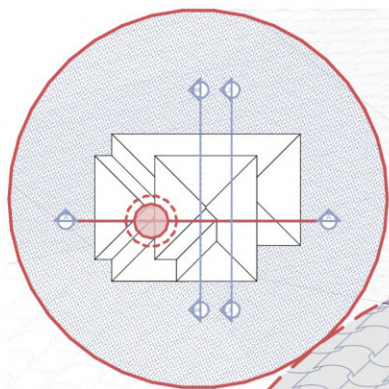

DETALIU A-12 1:10

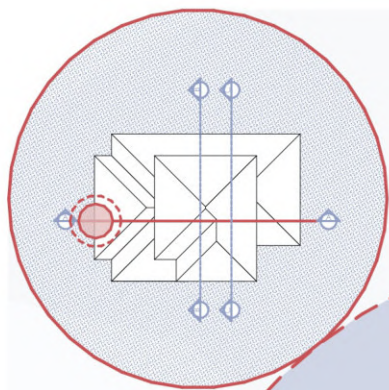


PE3	
Strat de vopsea exterior	0.3 cm
Tencuiala siliconica	1.3 cm
Plasa de armare	0.1 cm
Masa de spaclu	0.1 cm
Vata minerala	15.0 cm
Adeziv	0.3 cm
Caramida cu goluri verticale	30.0 cm
Adeziv	1.0 cm
Gipscarton	1.3 cm
Tencuiala pe baza de ipsos	0.5 cm
Strat de vopsea interior	0.3 cm

RG

TR 1	
Sapa de ciment	5.0 cm
Beton armat monolit	15.0 cm
Nisip	5.0 cm
Pietris	10.0 cm


DORMITOR

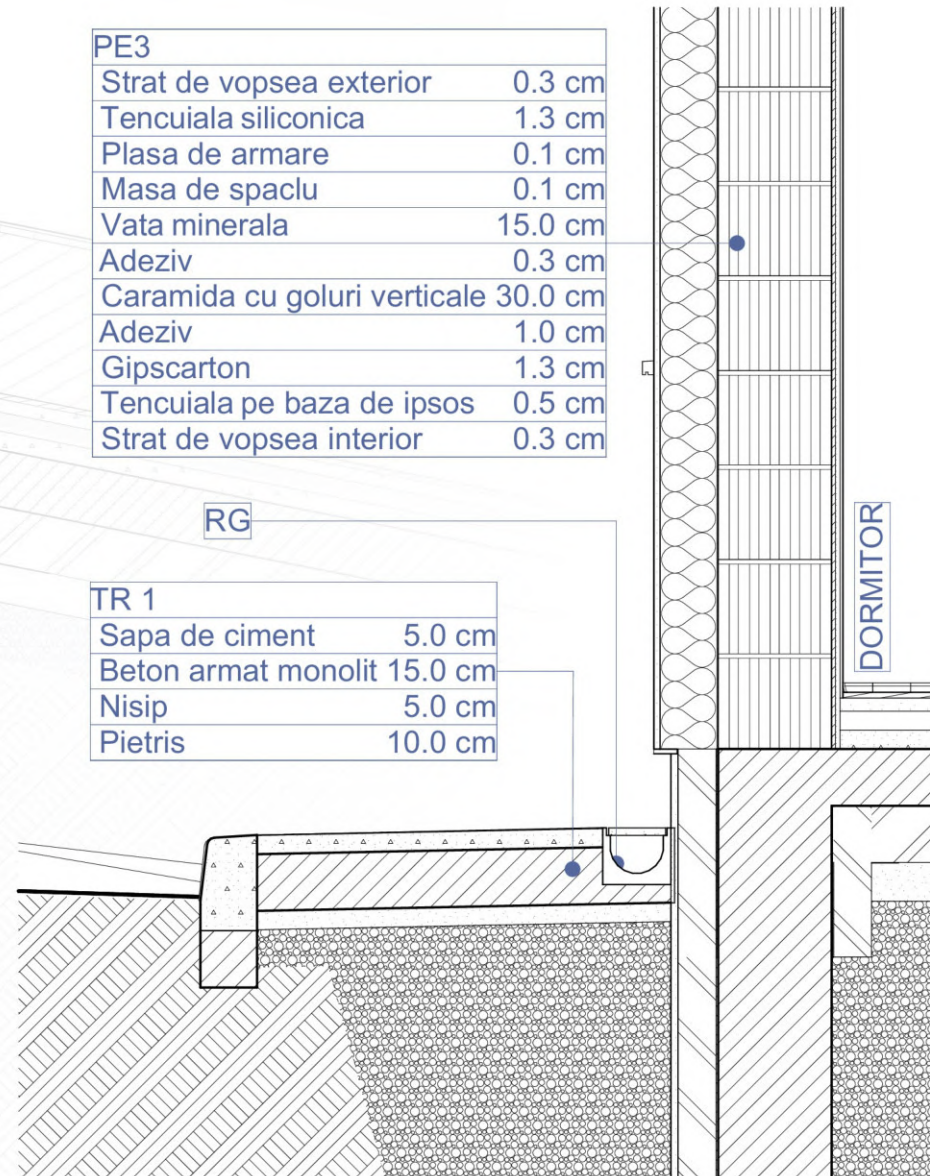





DETALIU B-4 1:10

PL 3




1.5 cm	Strat de vopsea exterior
0.3 cm	Membrana hidroizolanta
15.0 cm	Polistiren expandat
0.3 cm	Adeziv
15.0 cm	Beton armat monolit
5.0 cm	Sapa de ciment
3.5 cm	Beton usor
1.5 cm	Strat de vopsea exterior



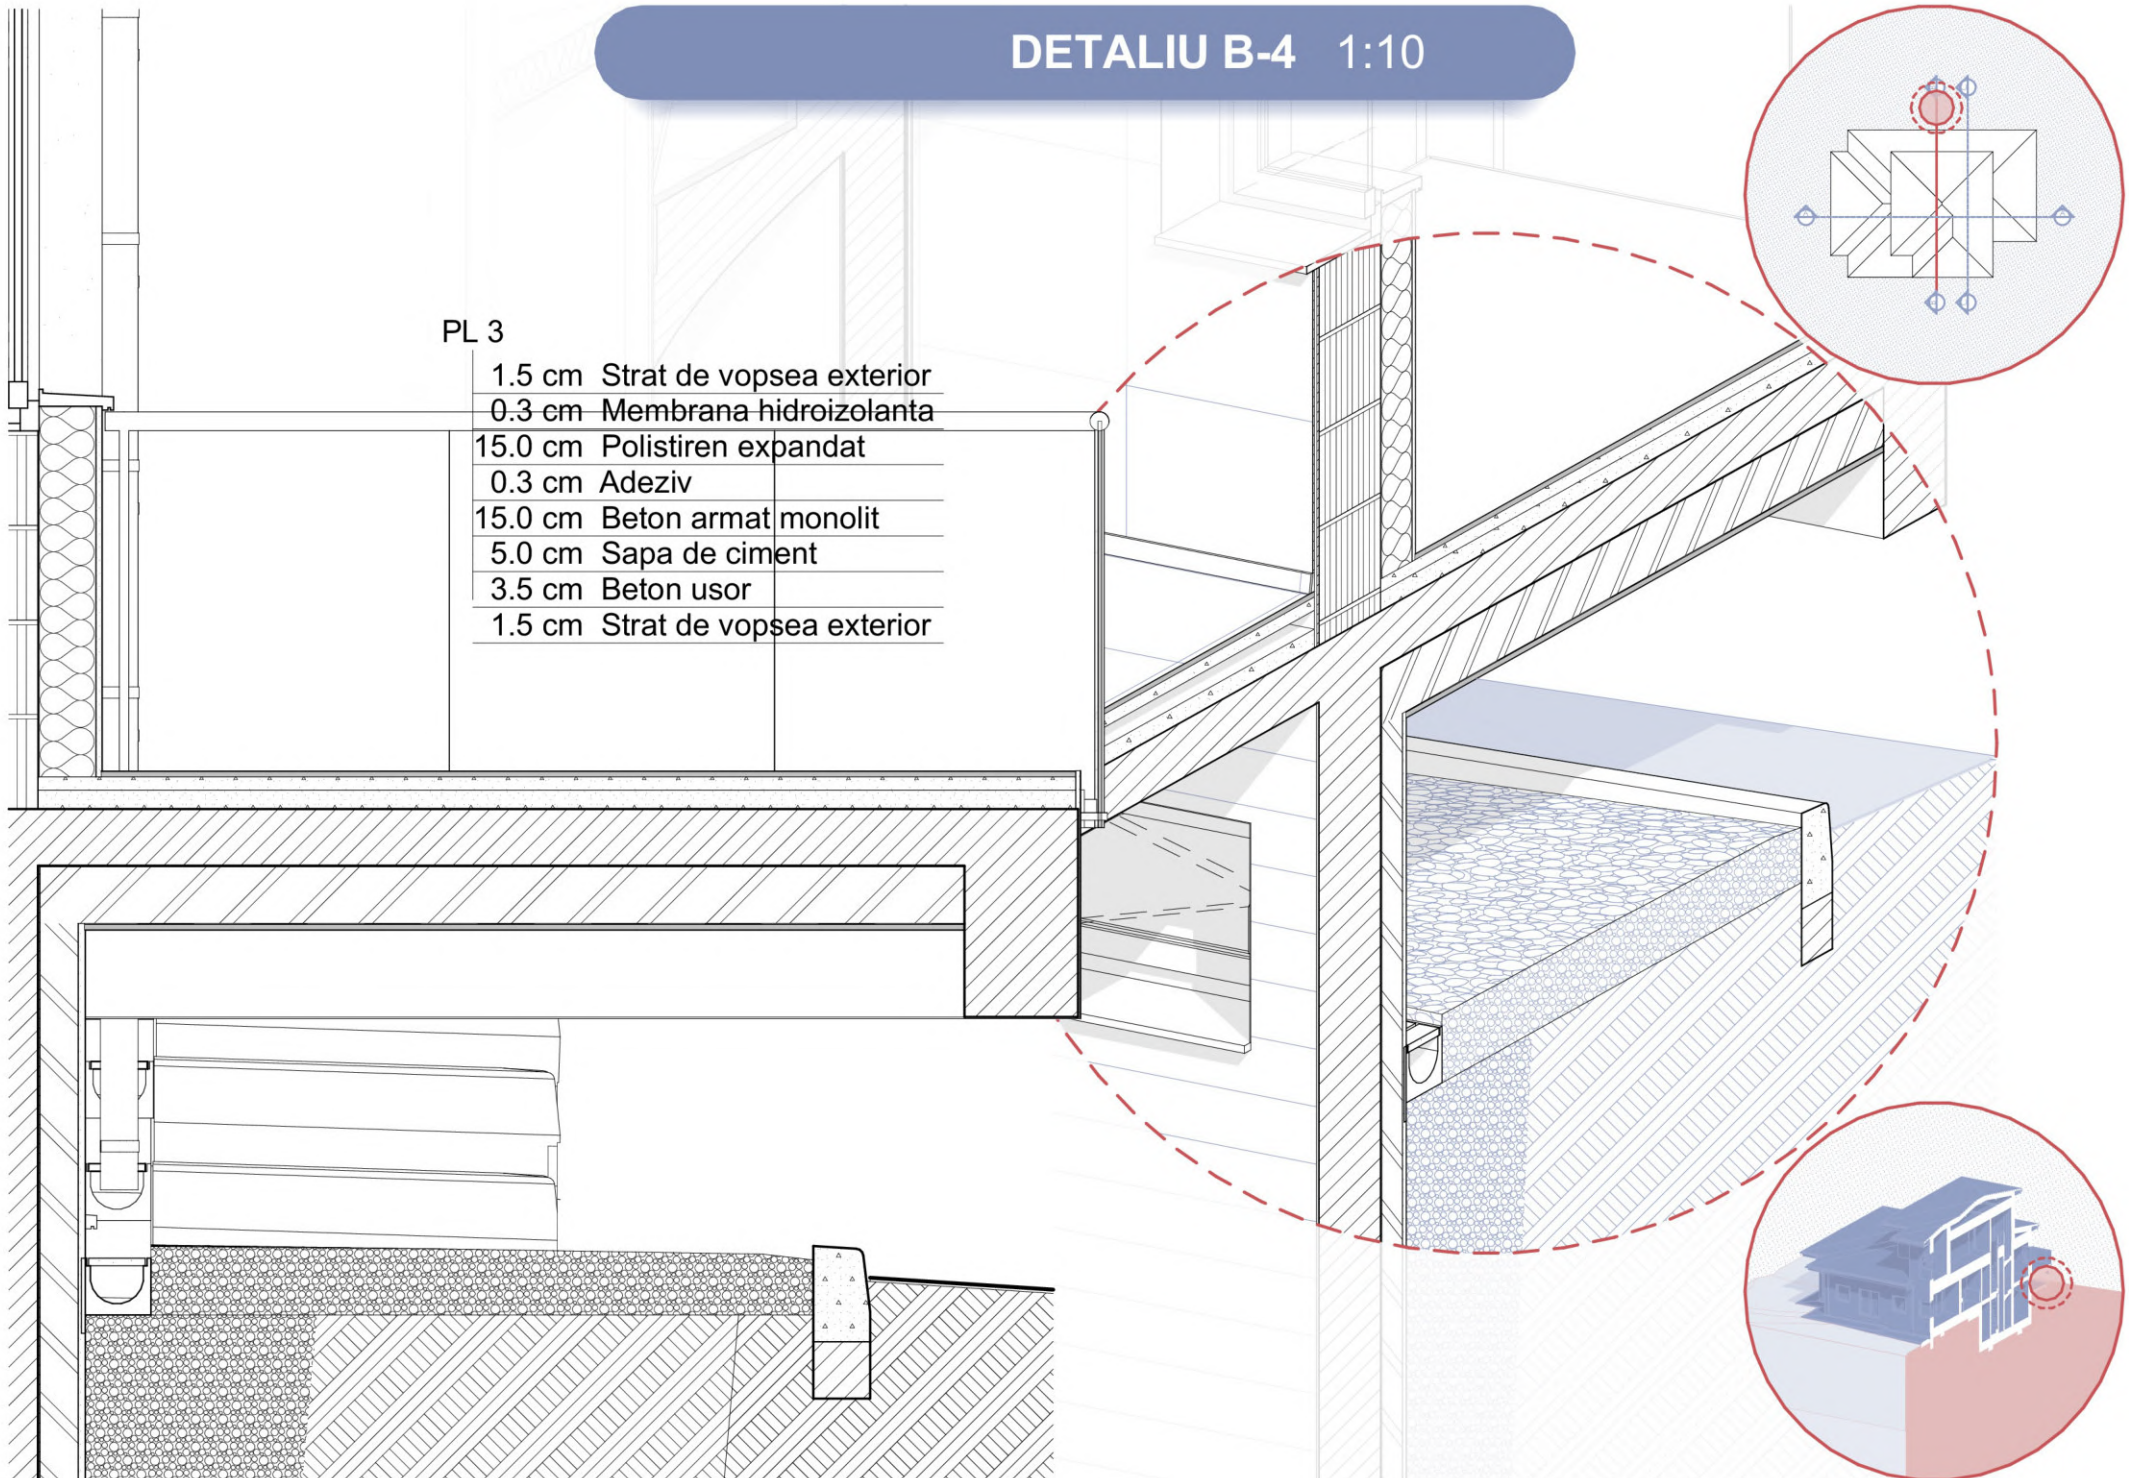


DETALIU B-6 1:10

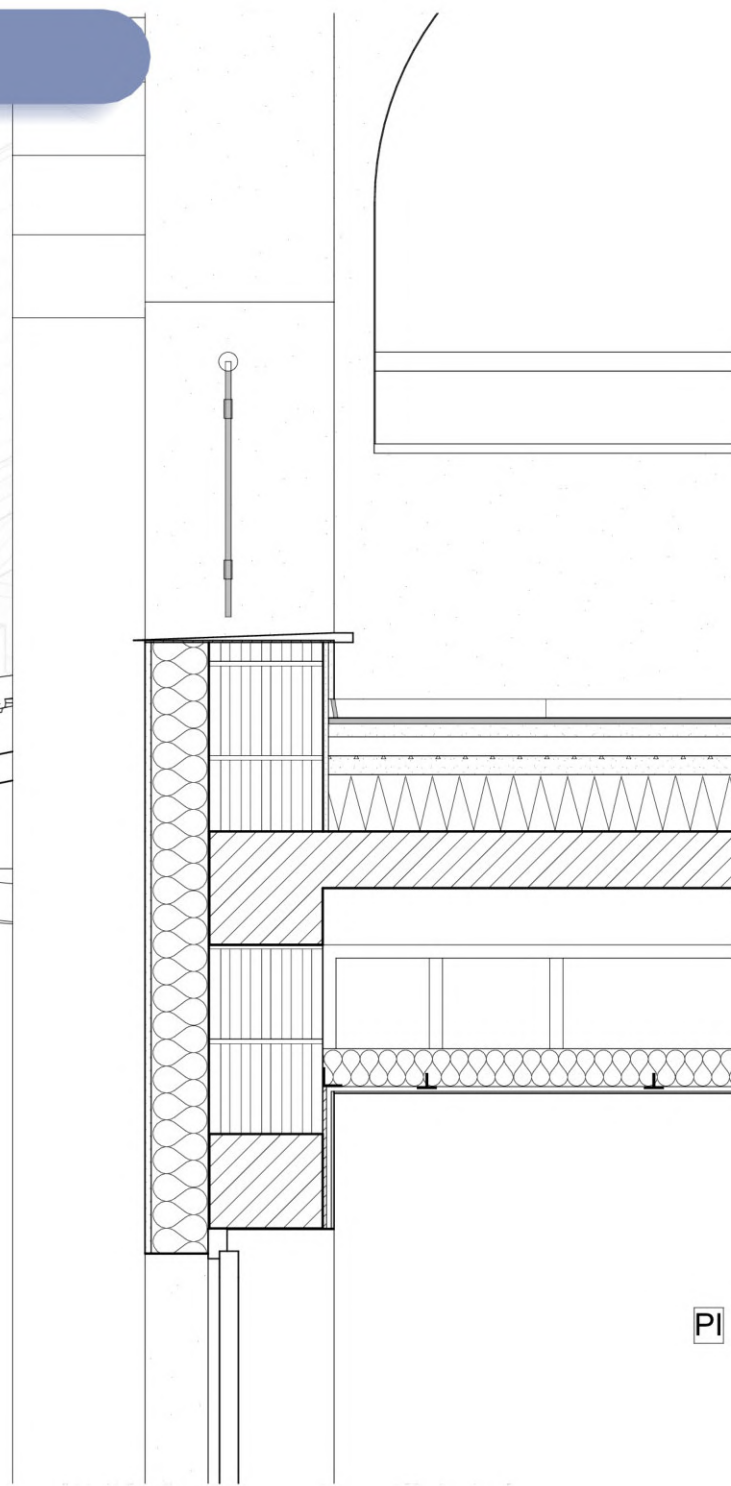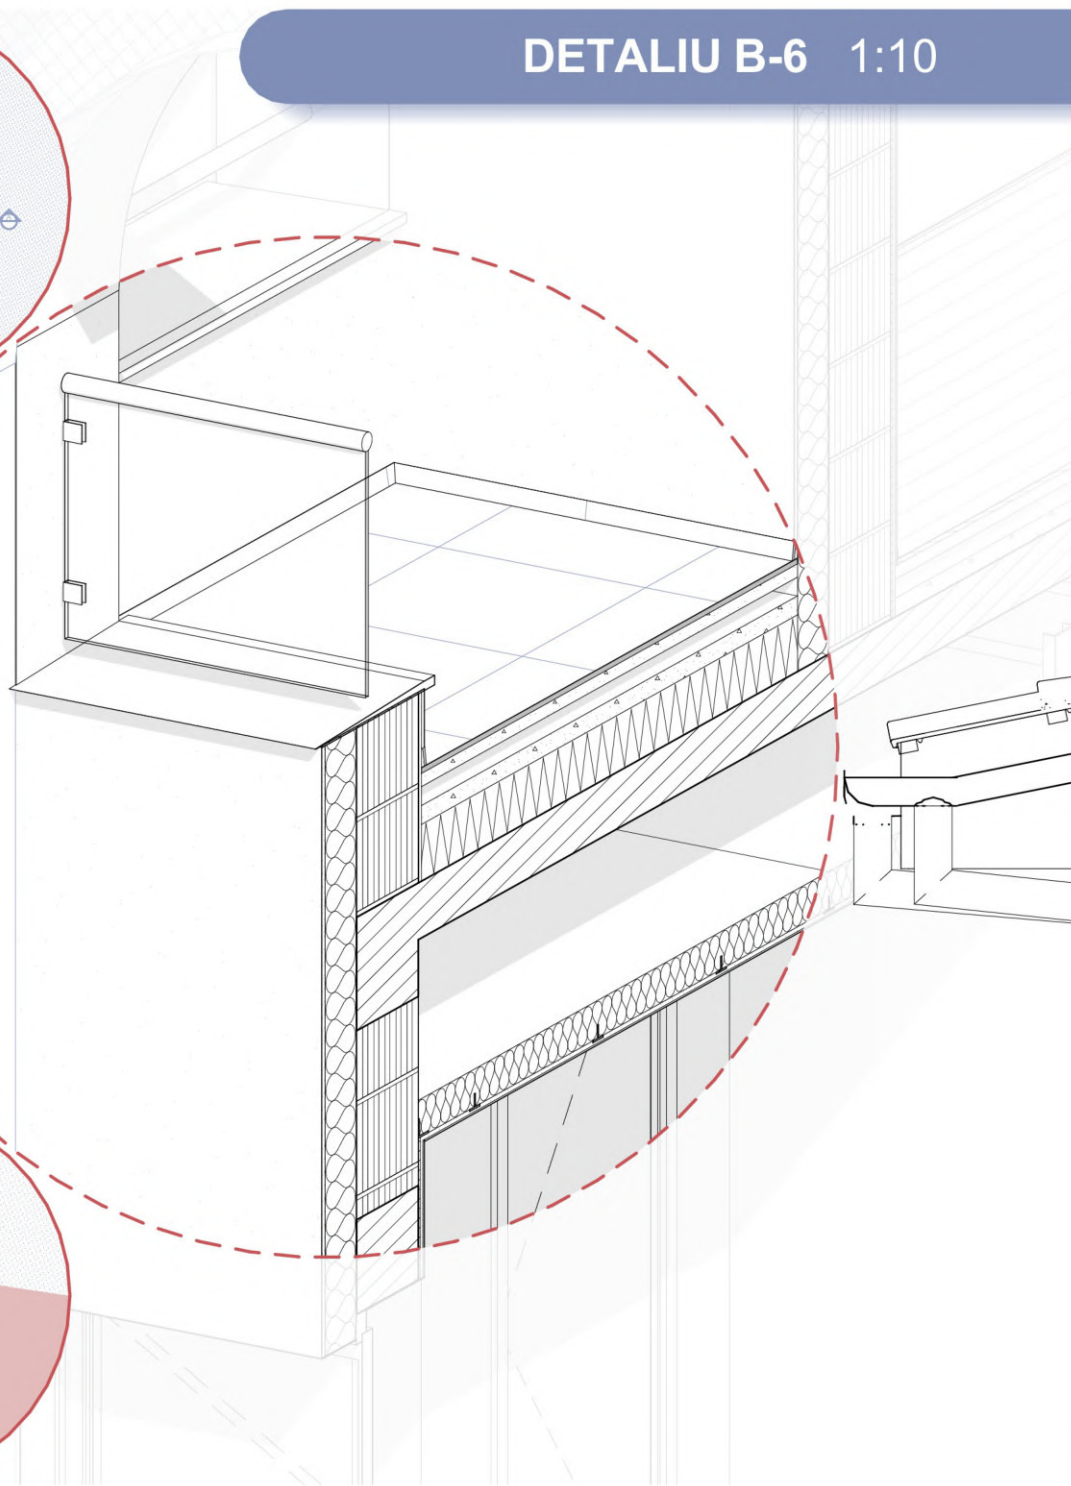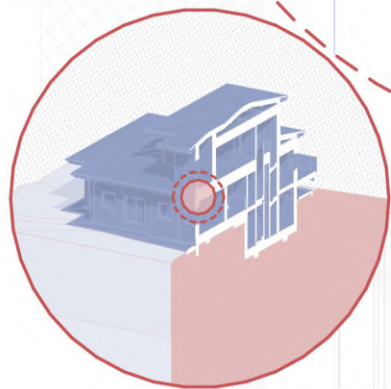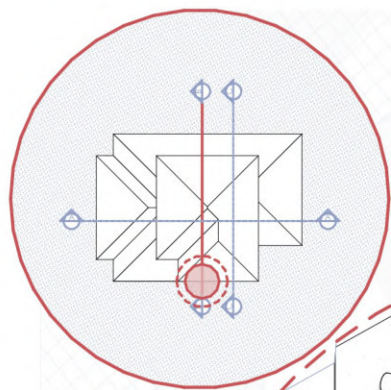


DETALIU B-7 1:10



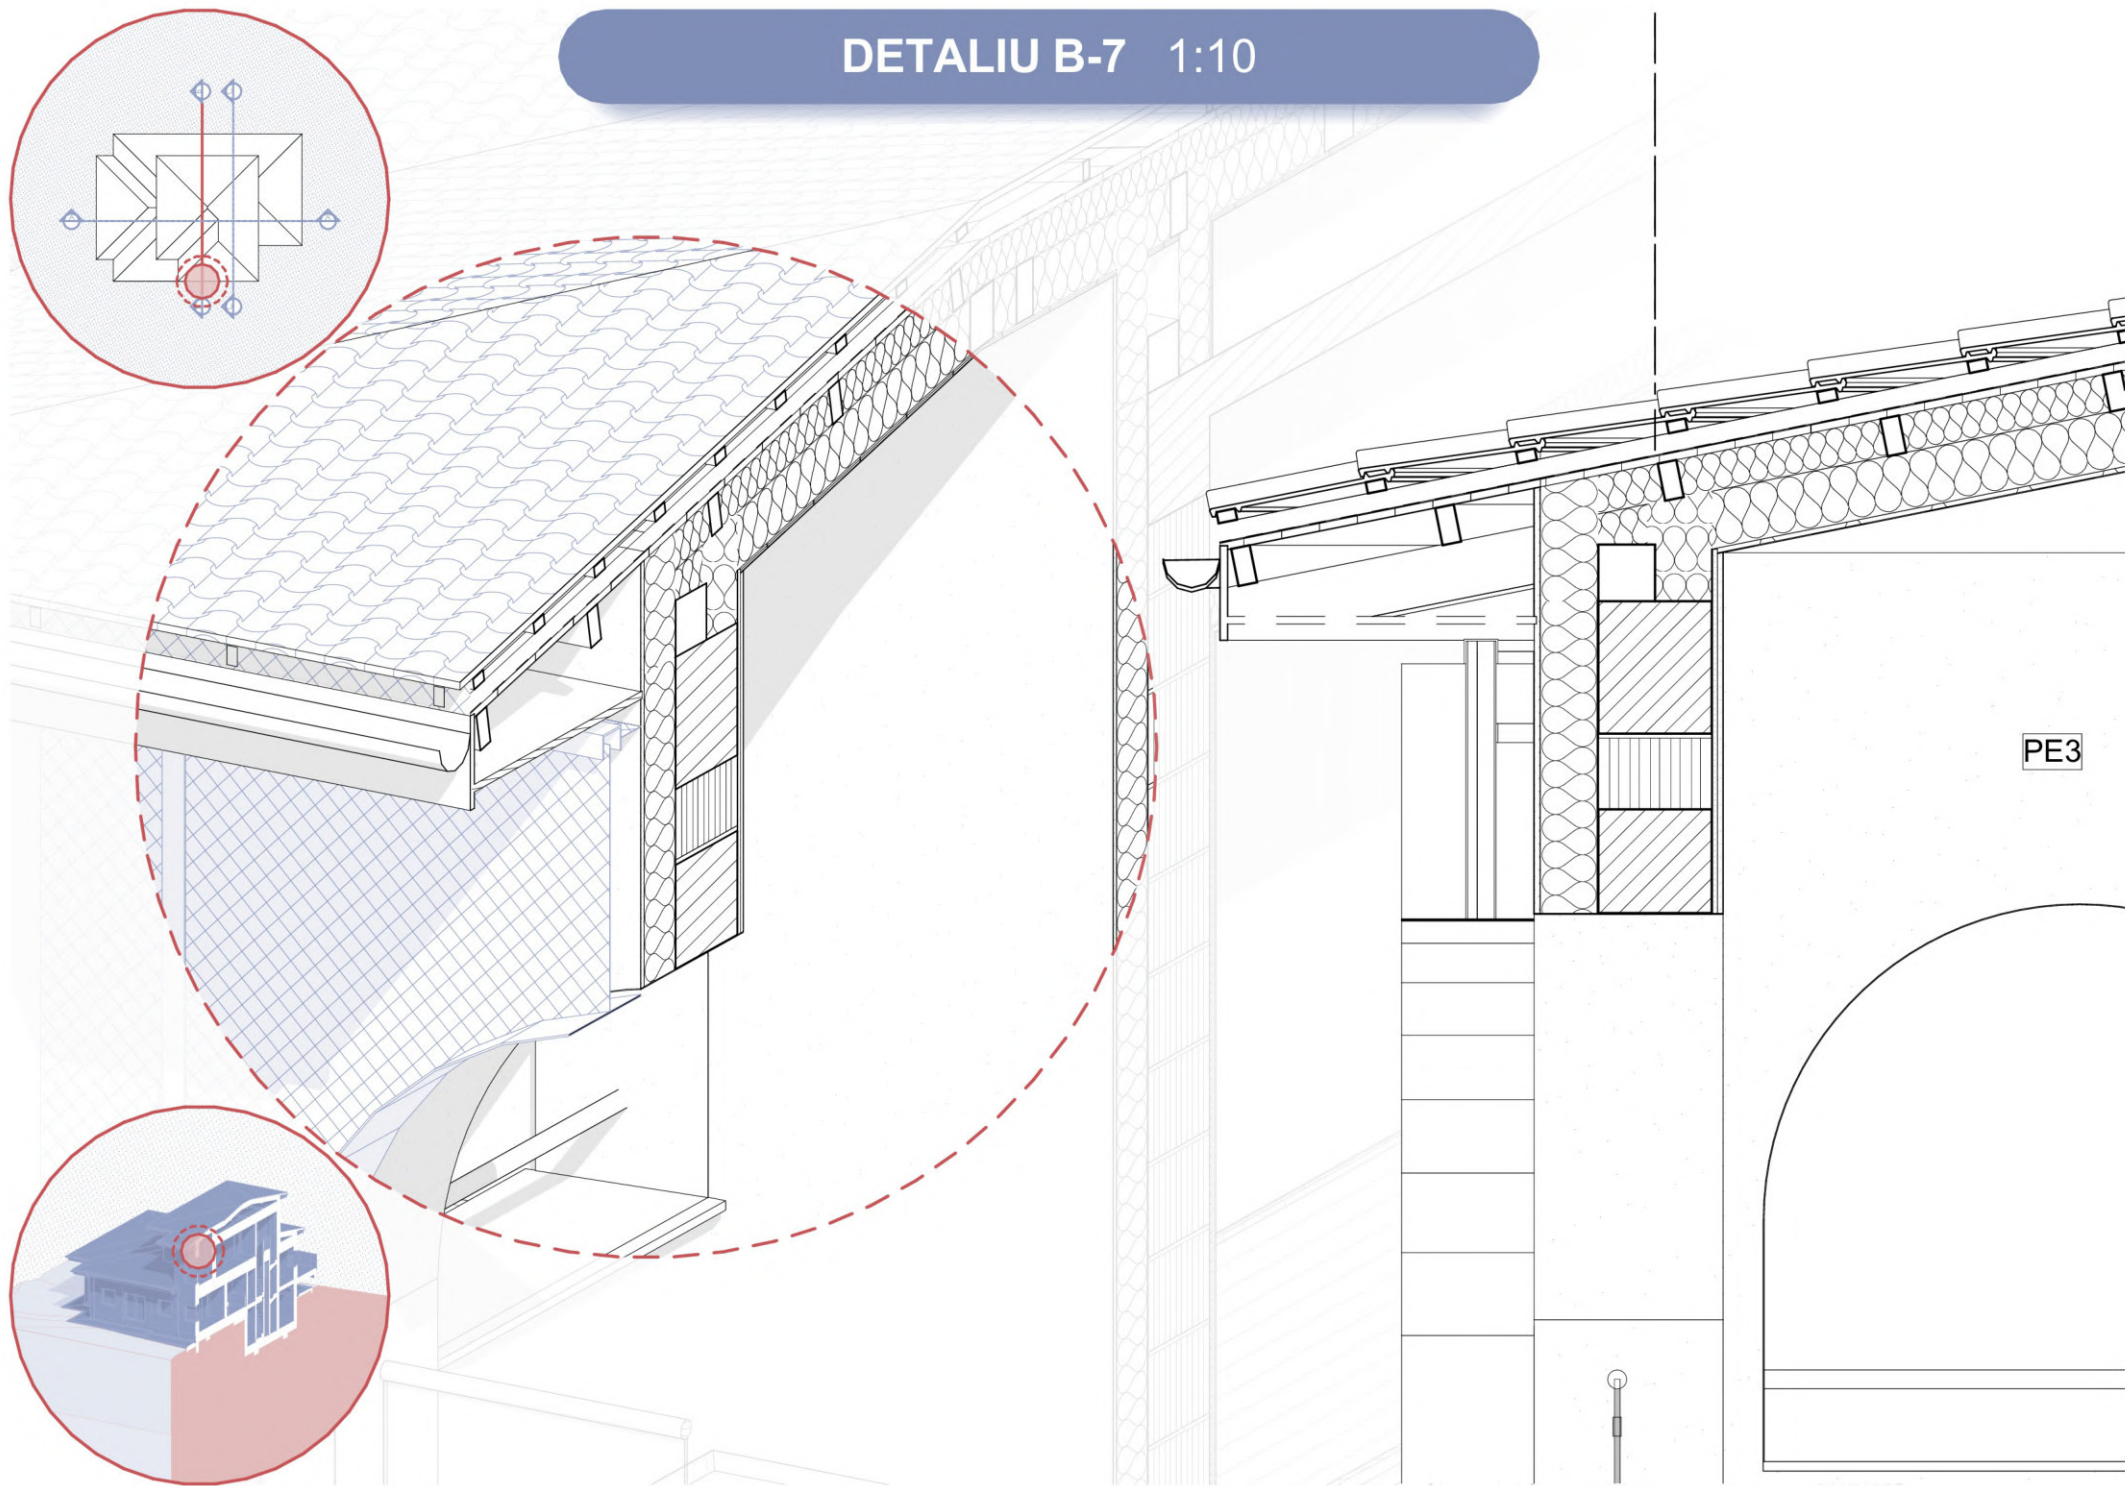
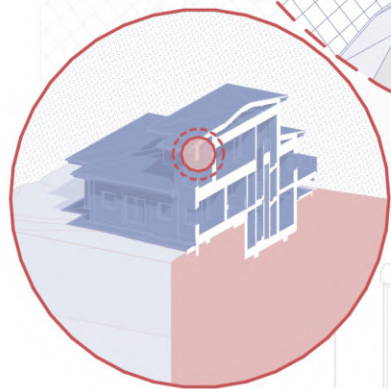
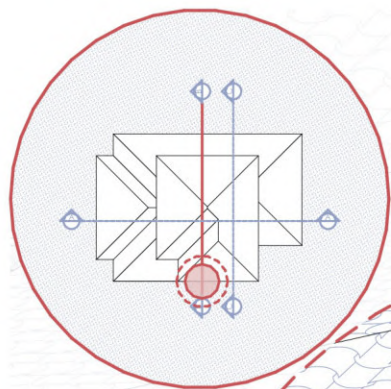


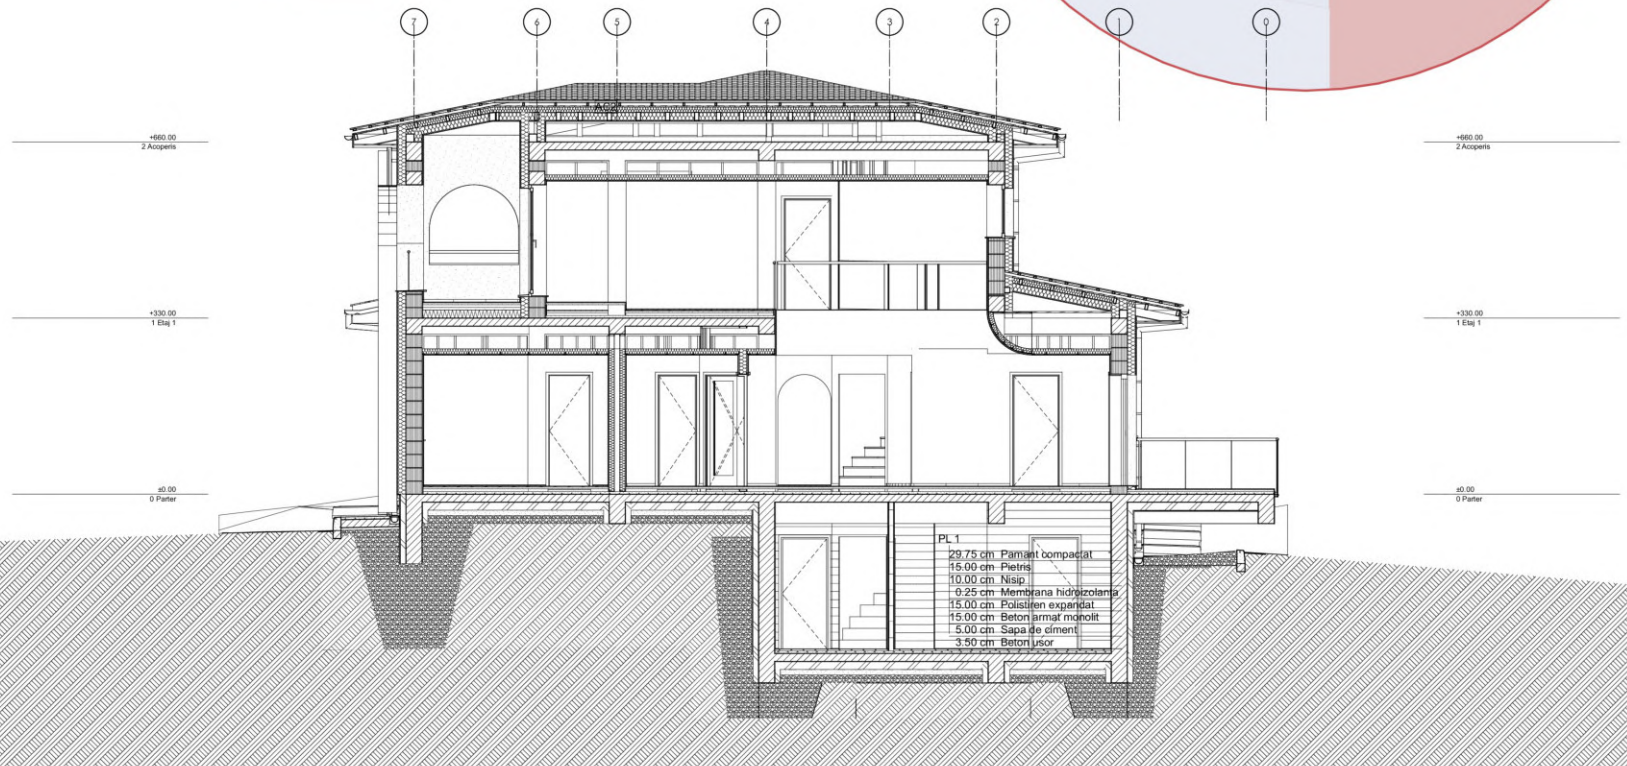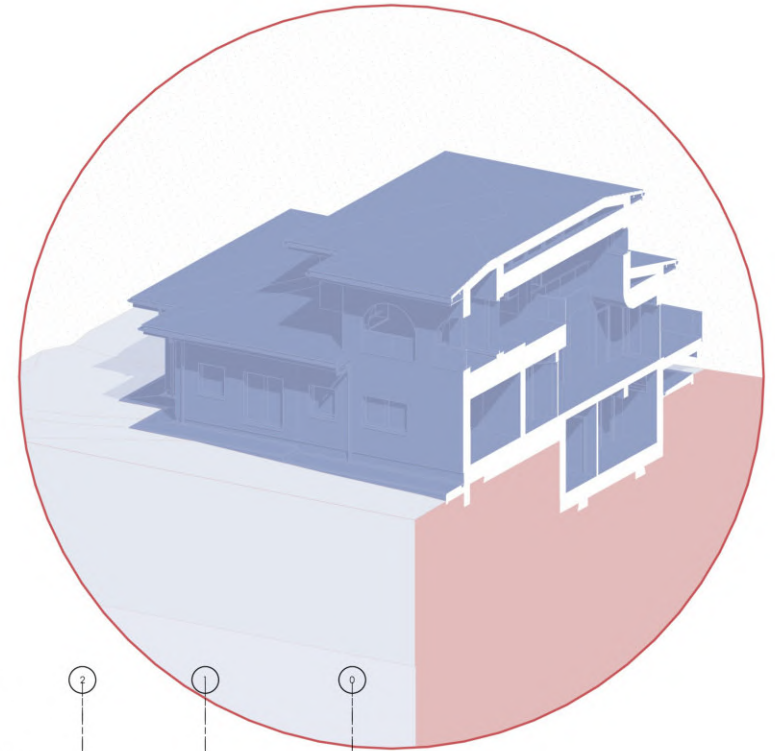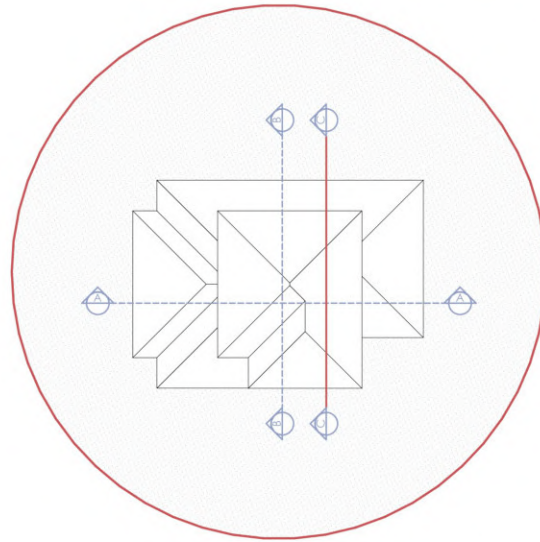





DETALIU C-1 1:10

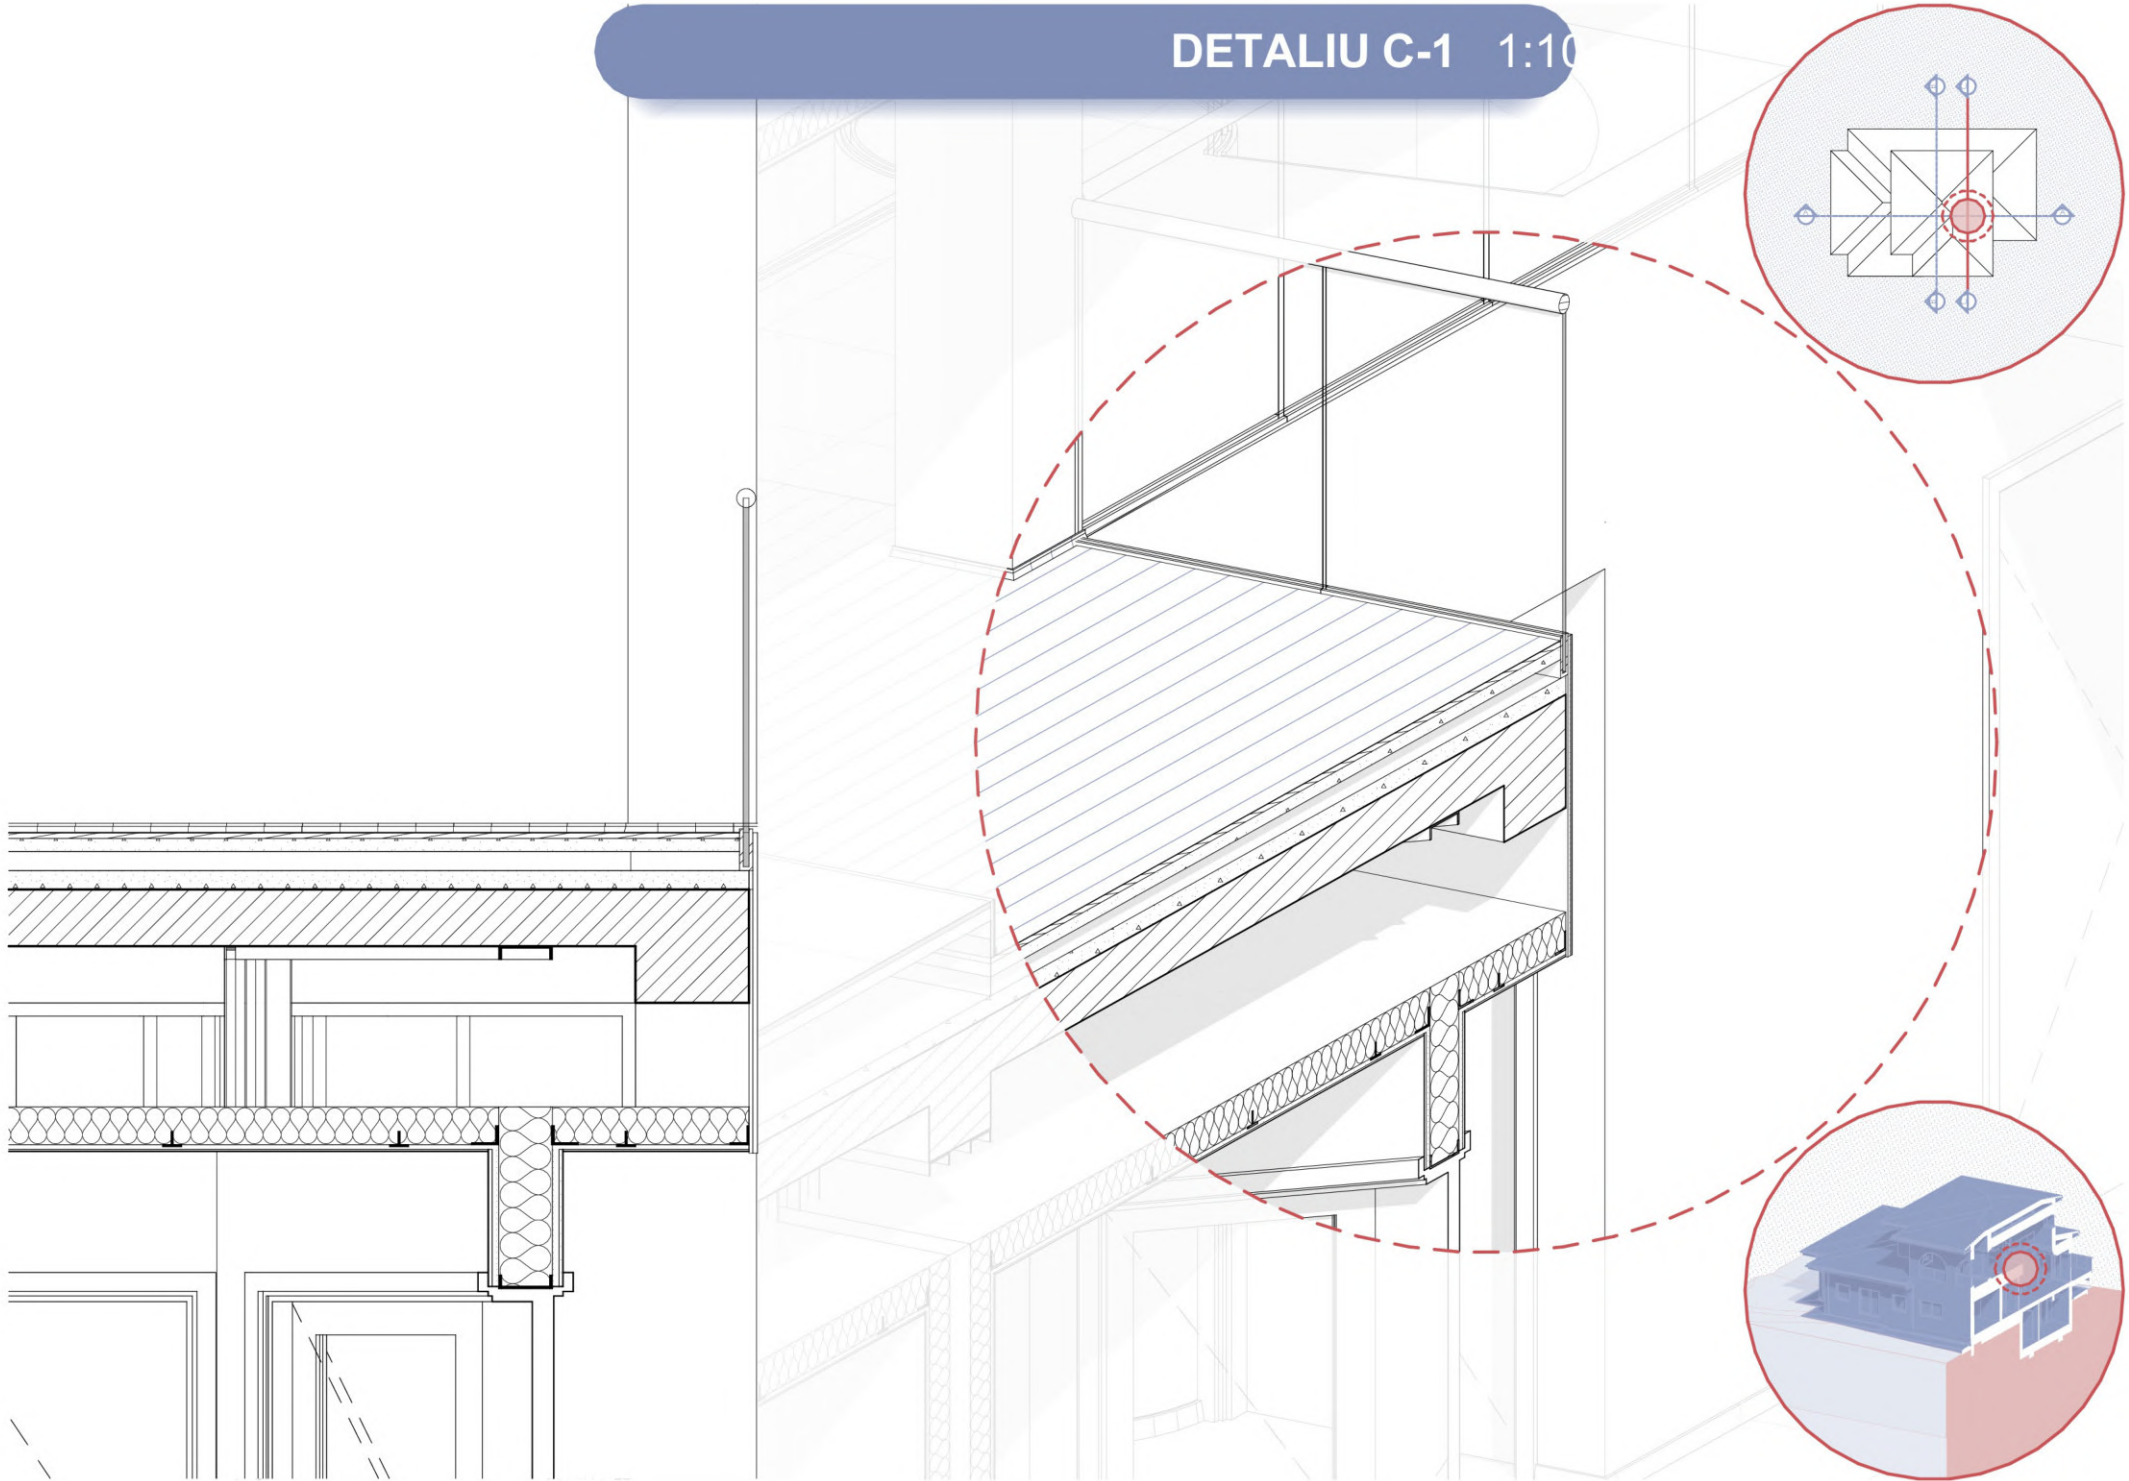

DETALIU C-2 1:10

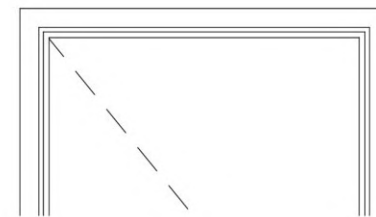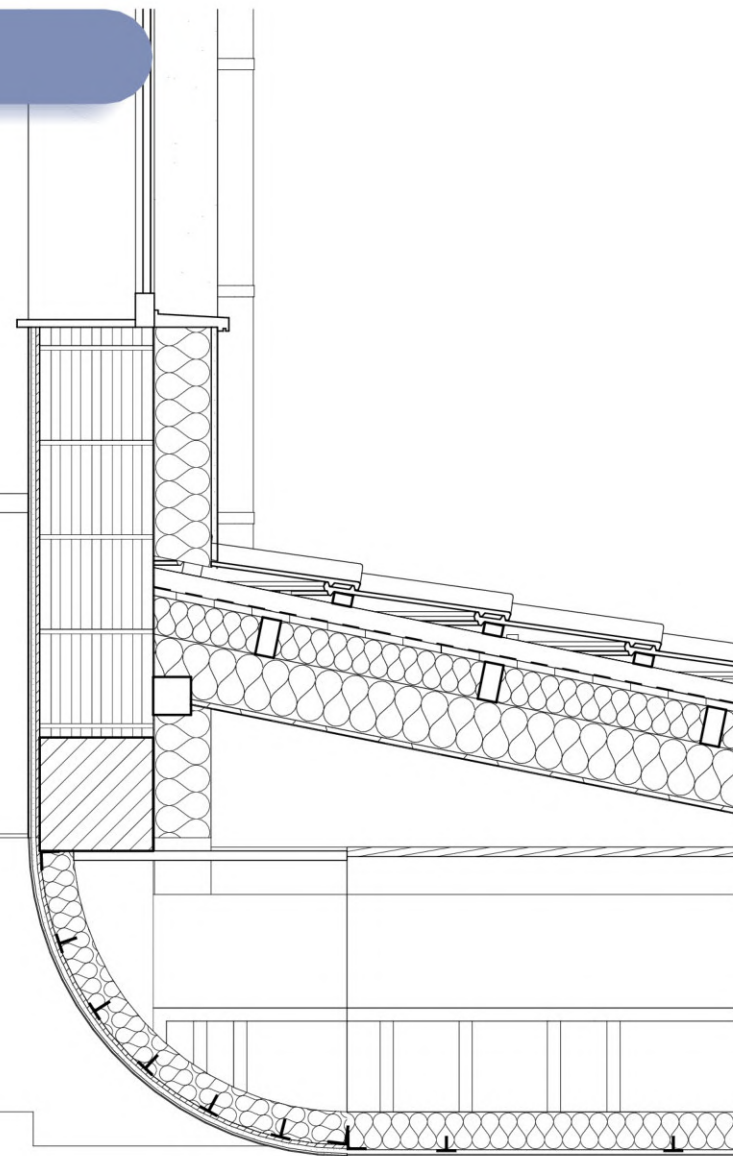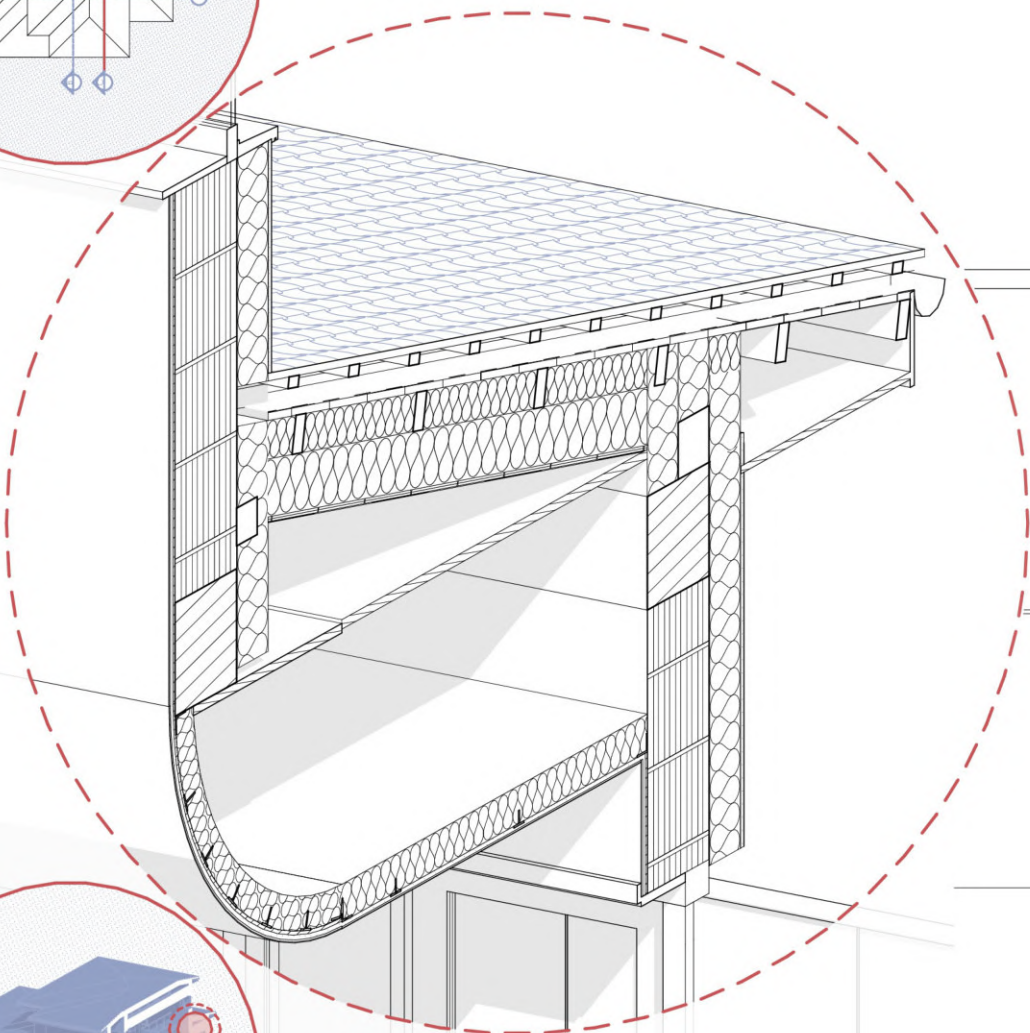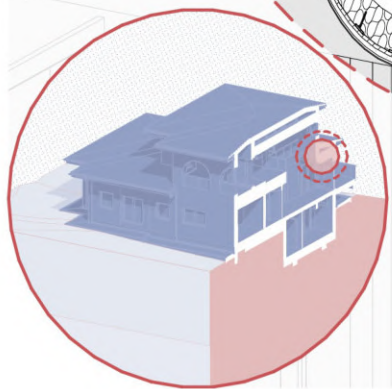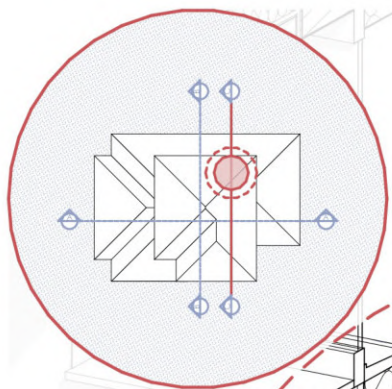


DETALIU C-3 1:10

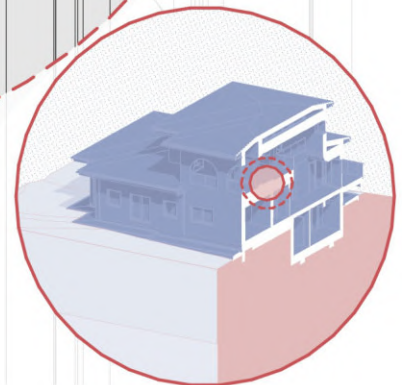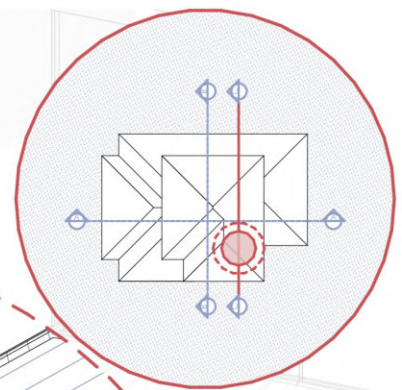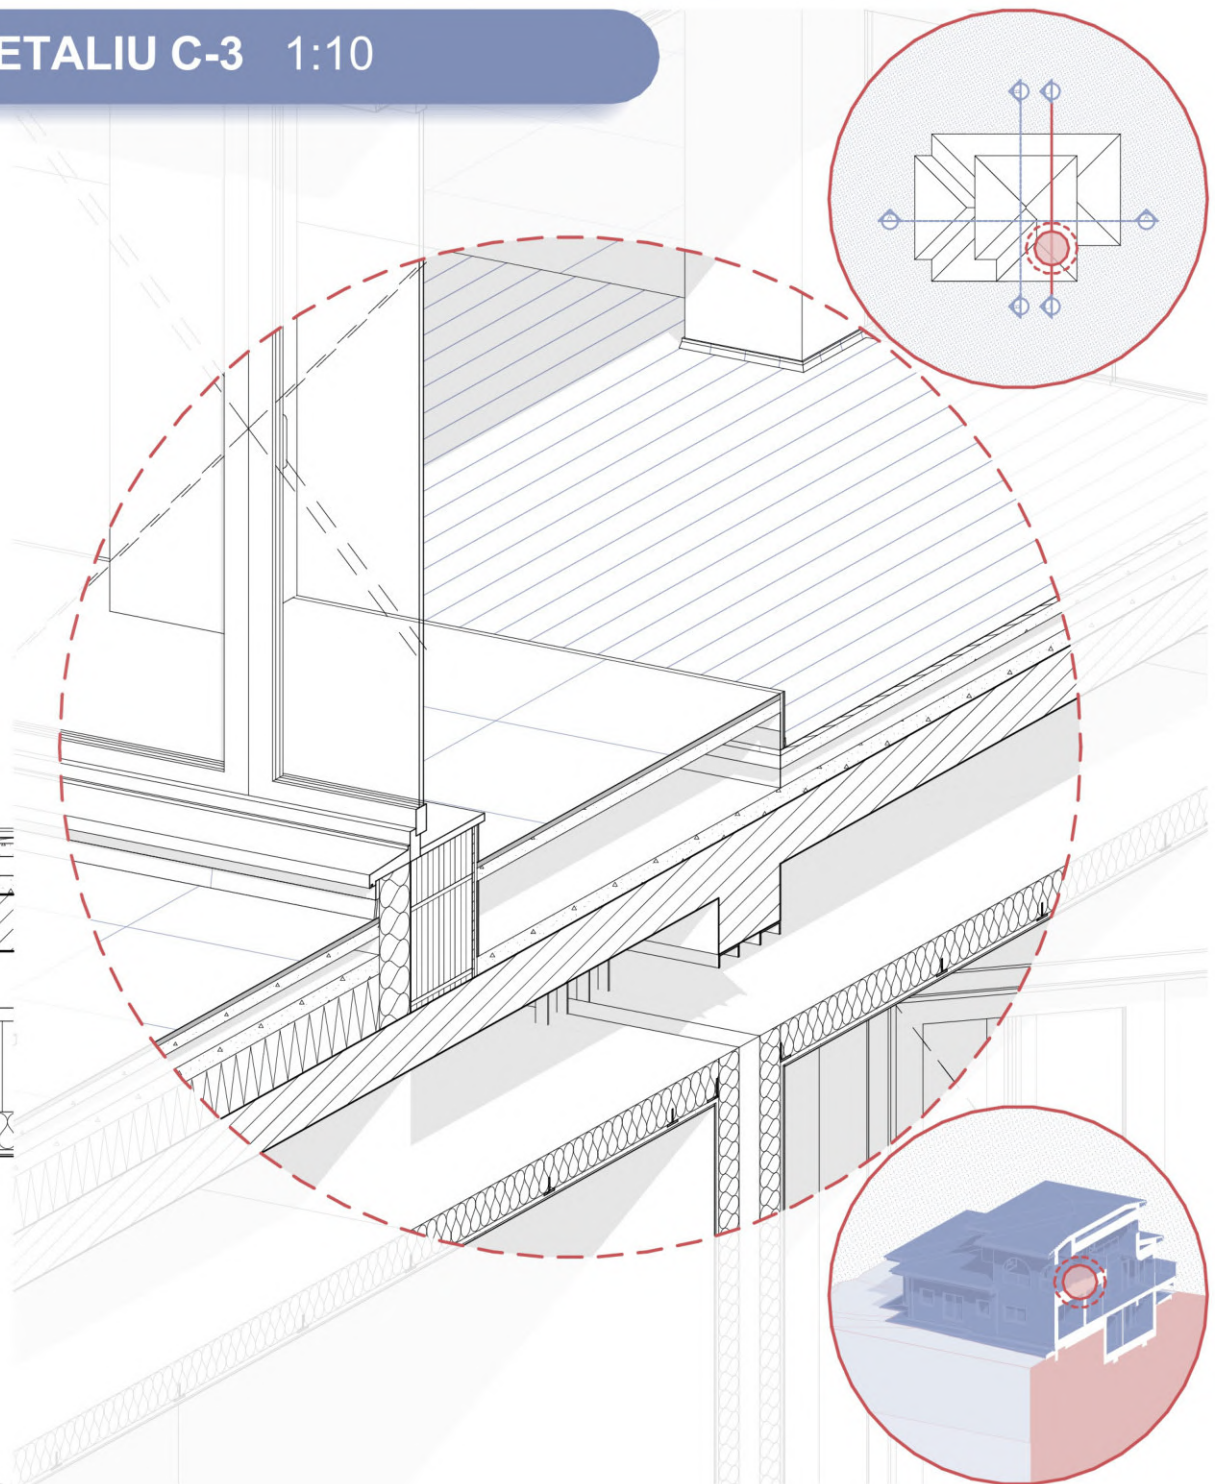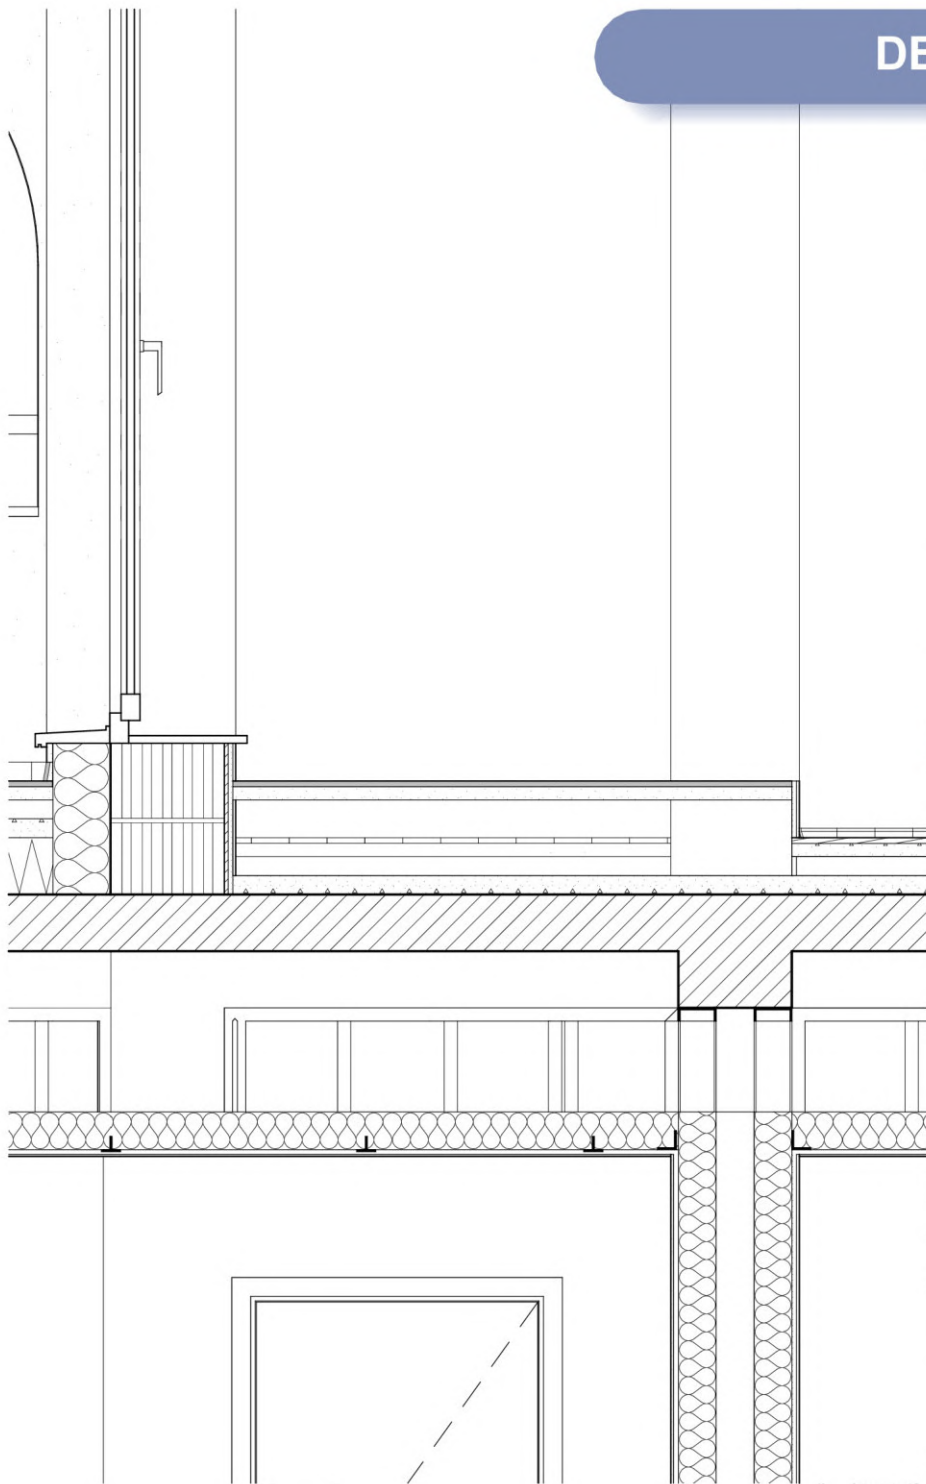

TEHNIC

FATADA EST


1:50

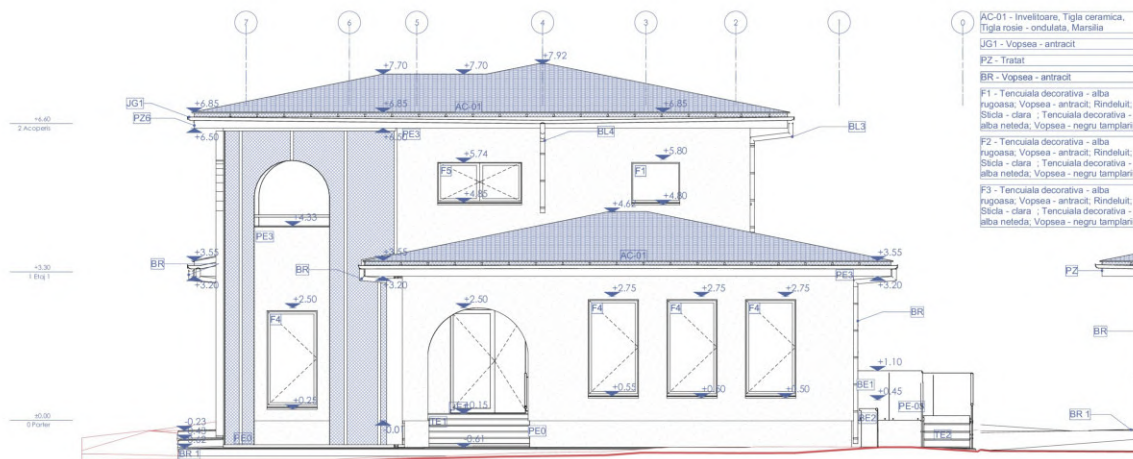

TEHNIC

FATADA SUD


1:50

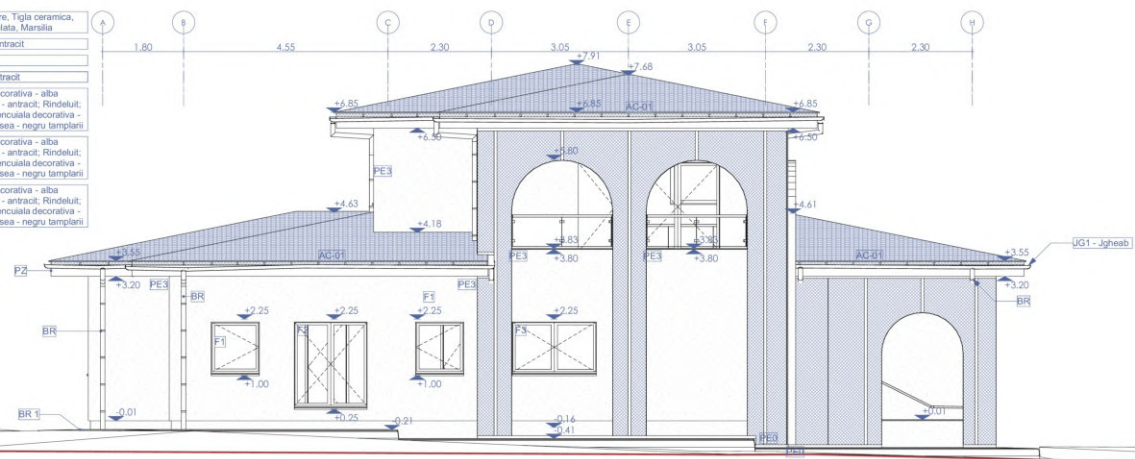

TEHNIC

FATADA VEST


1:50

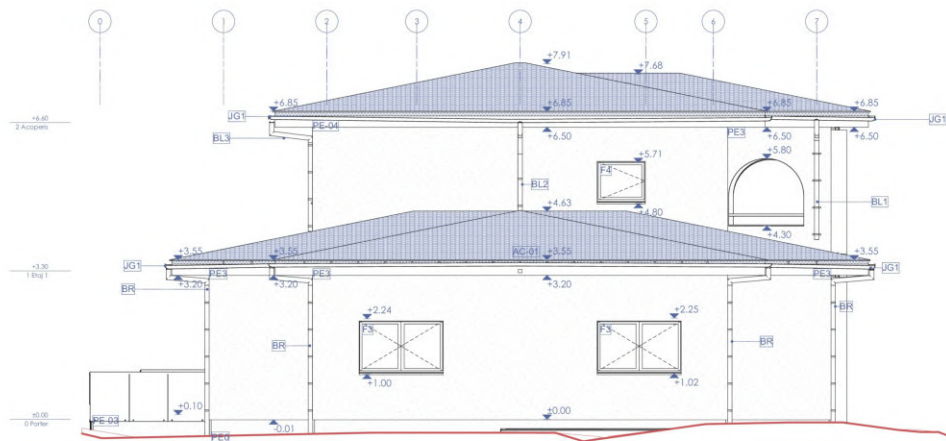


TEHNIC

FATADA NORD


1:50

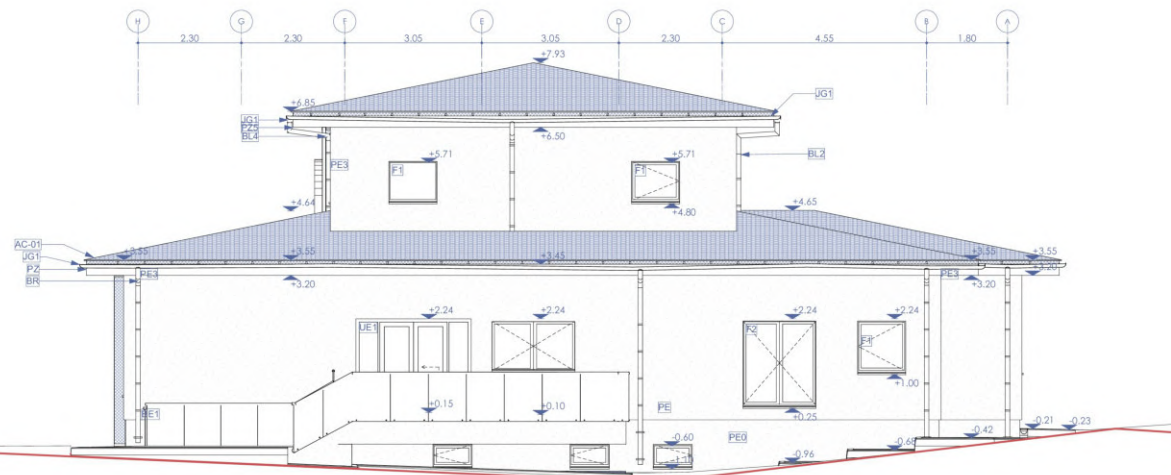


CASA DE CULTURA
SLOBOZIA

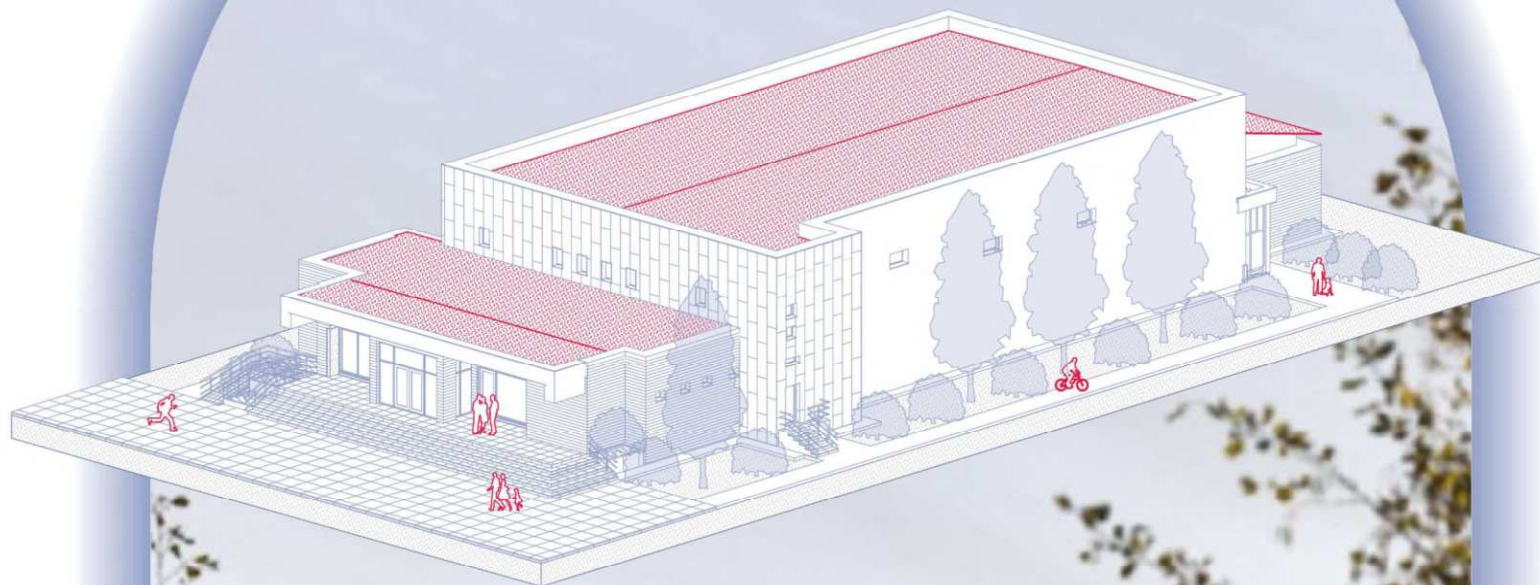

PLAN DE SITUATIE 1:400

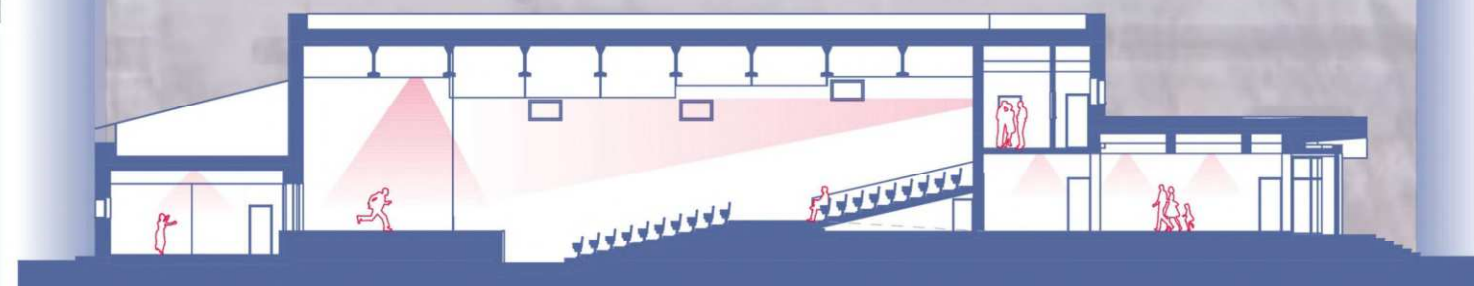

SECTIUNE A-A 1:150

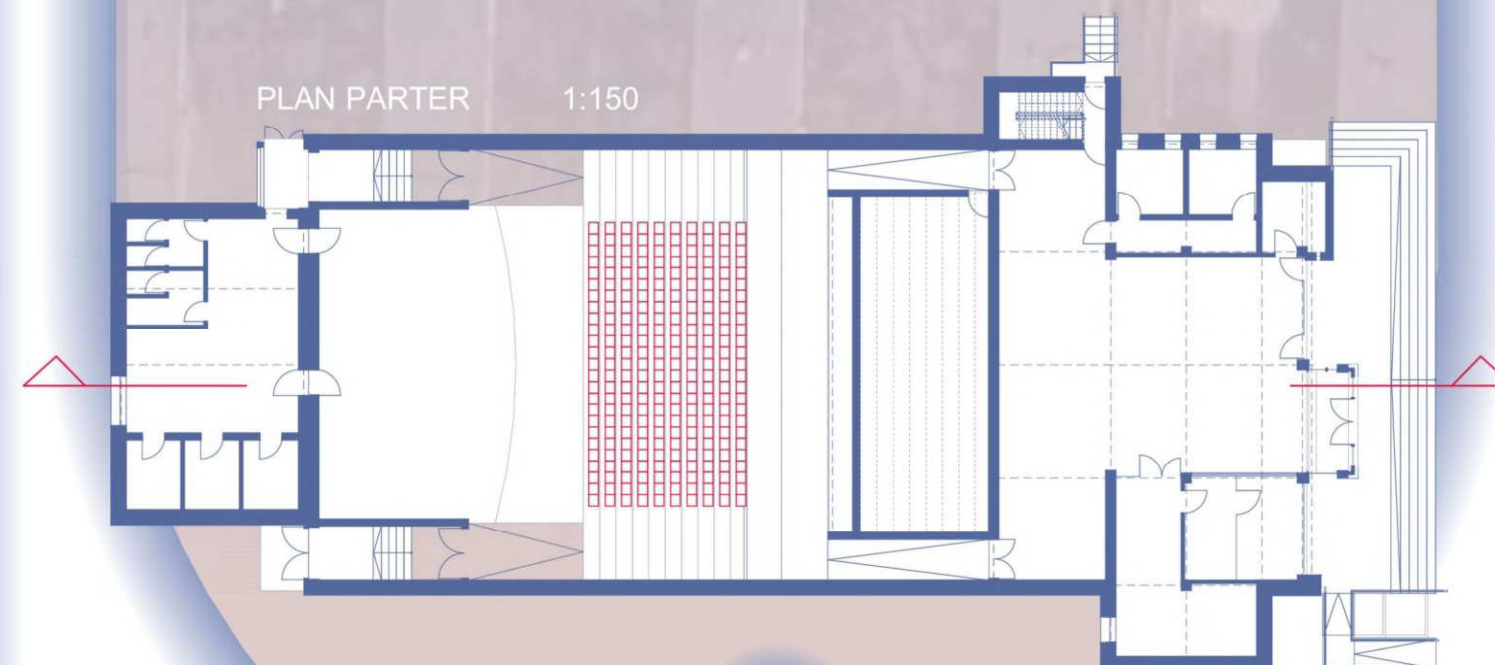

PLAN PARTER 1:150


PIATA AGRO-ALIMENTARA

STEFANESTI - BOTOSANI




SECTIUNE A-A 1:150

PLAN PARTER 1:150

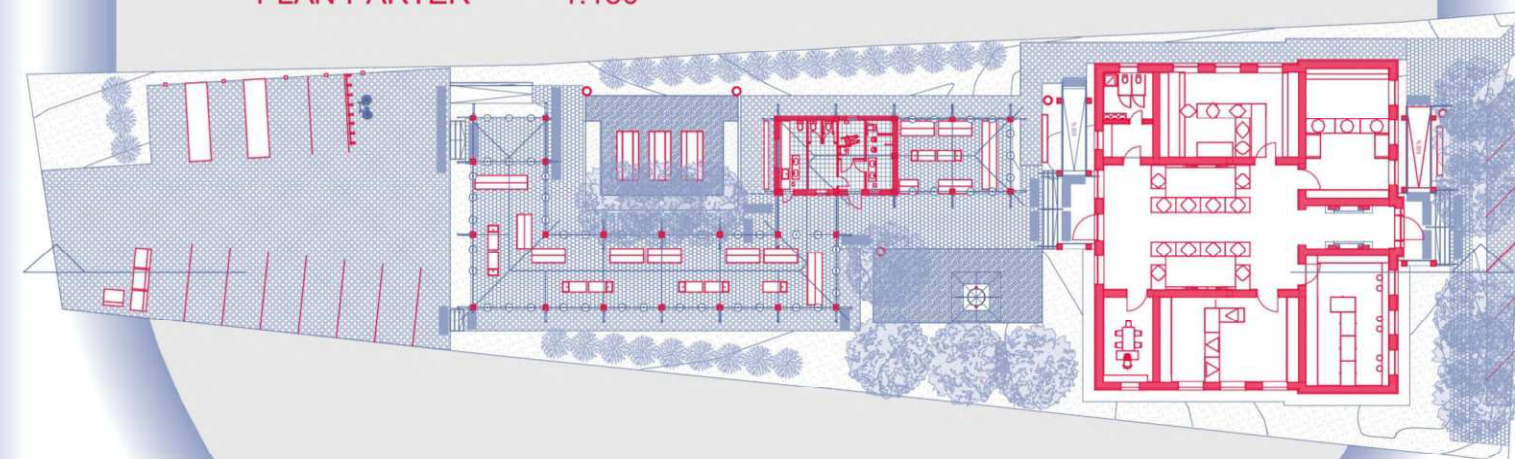





CASA SECUIENI ROMAN

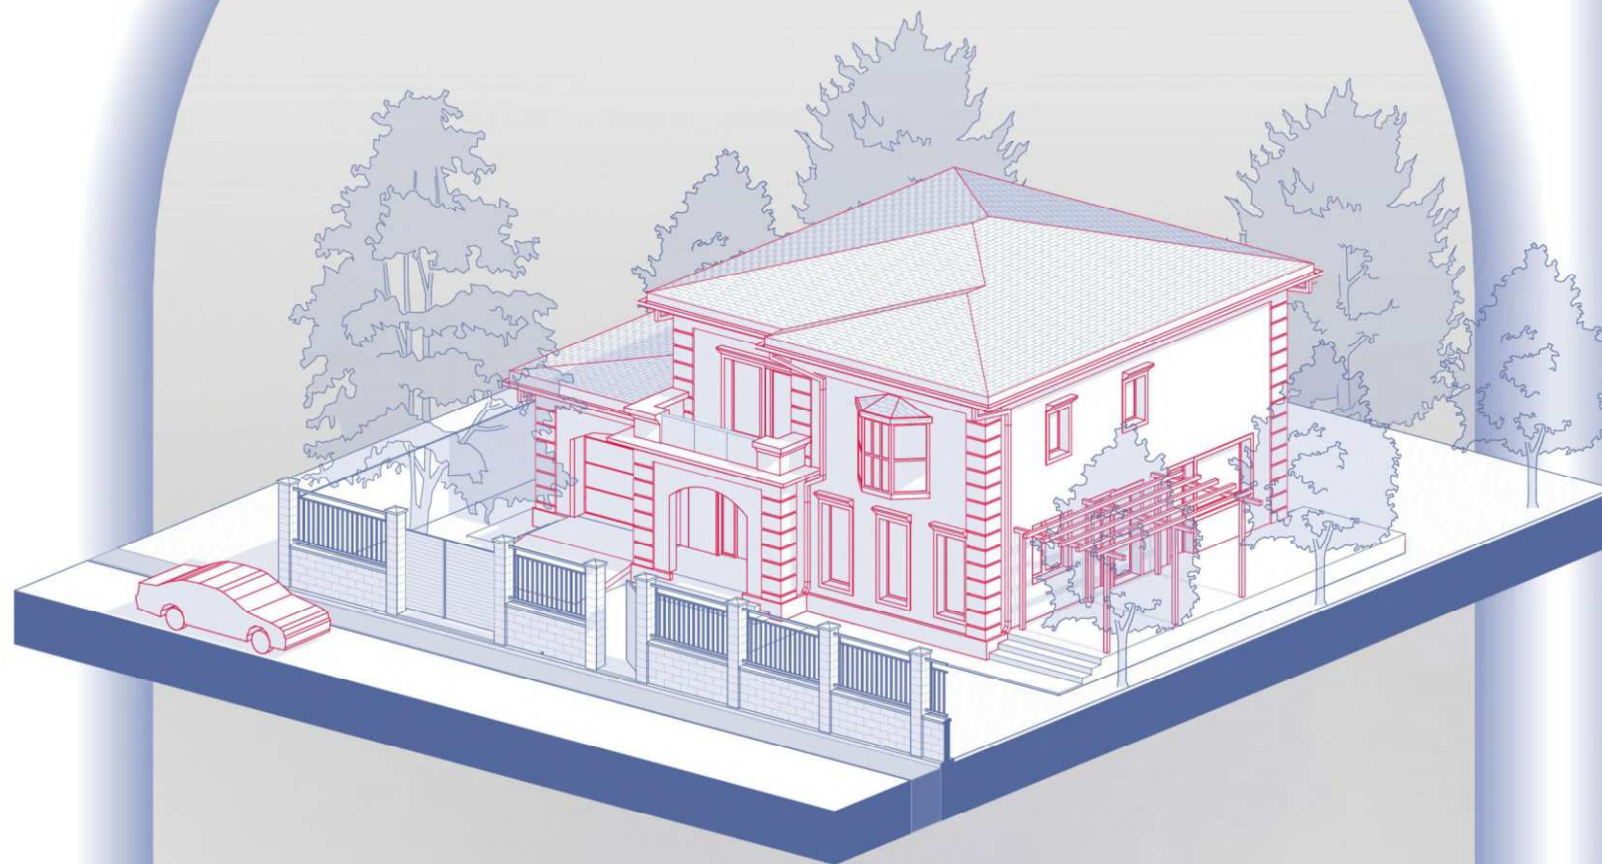


SECTIUNE A-A 1:150

PLAN PARTER 1:150

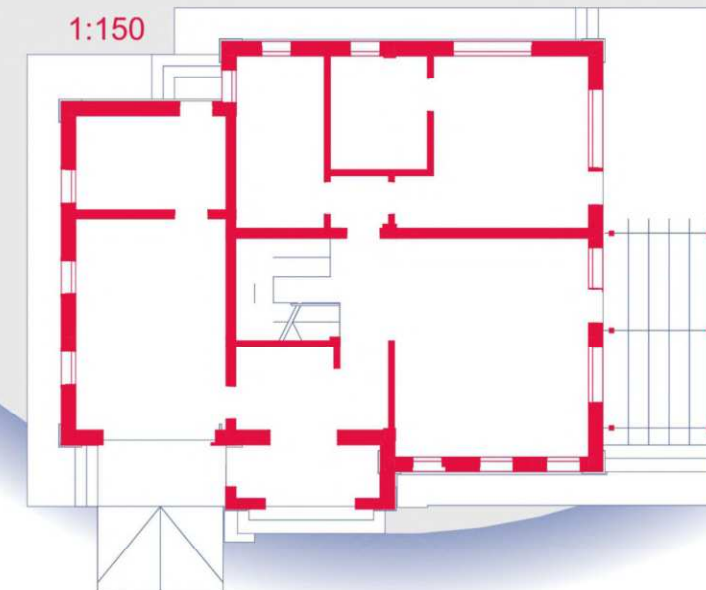


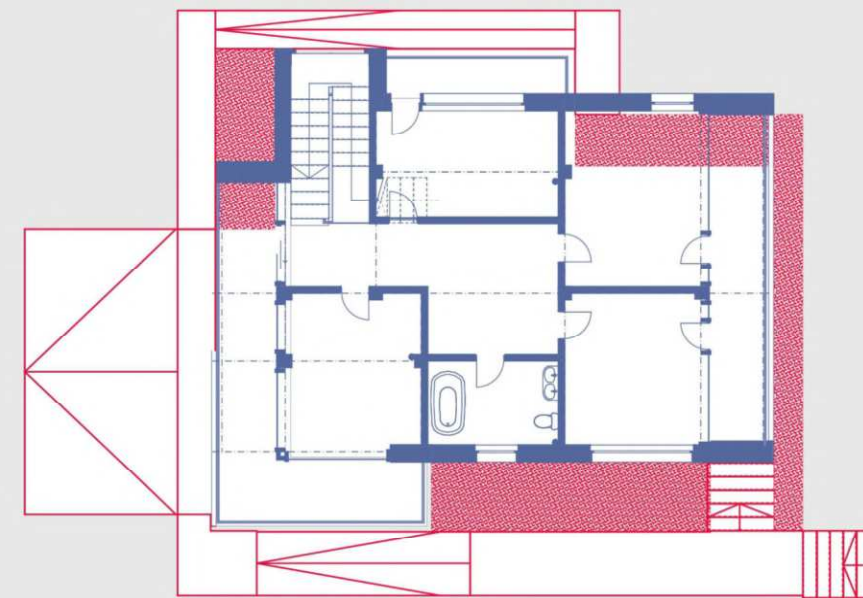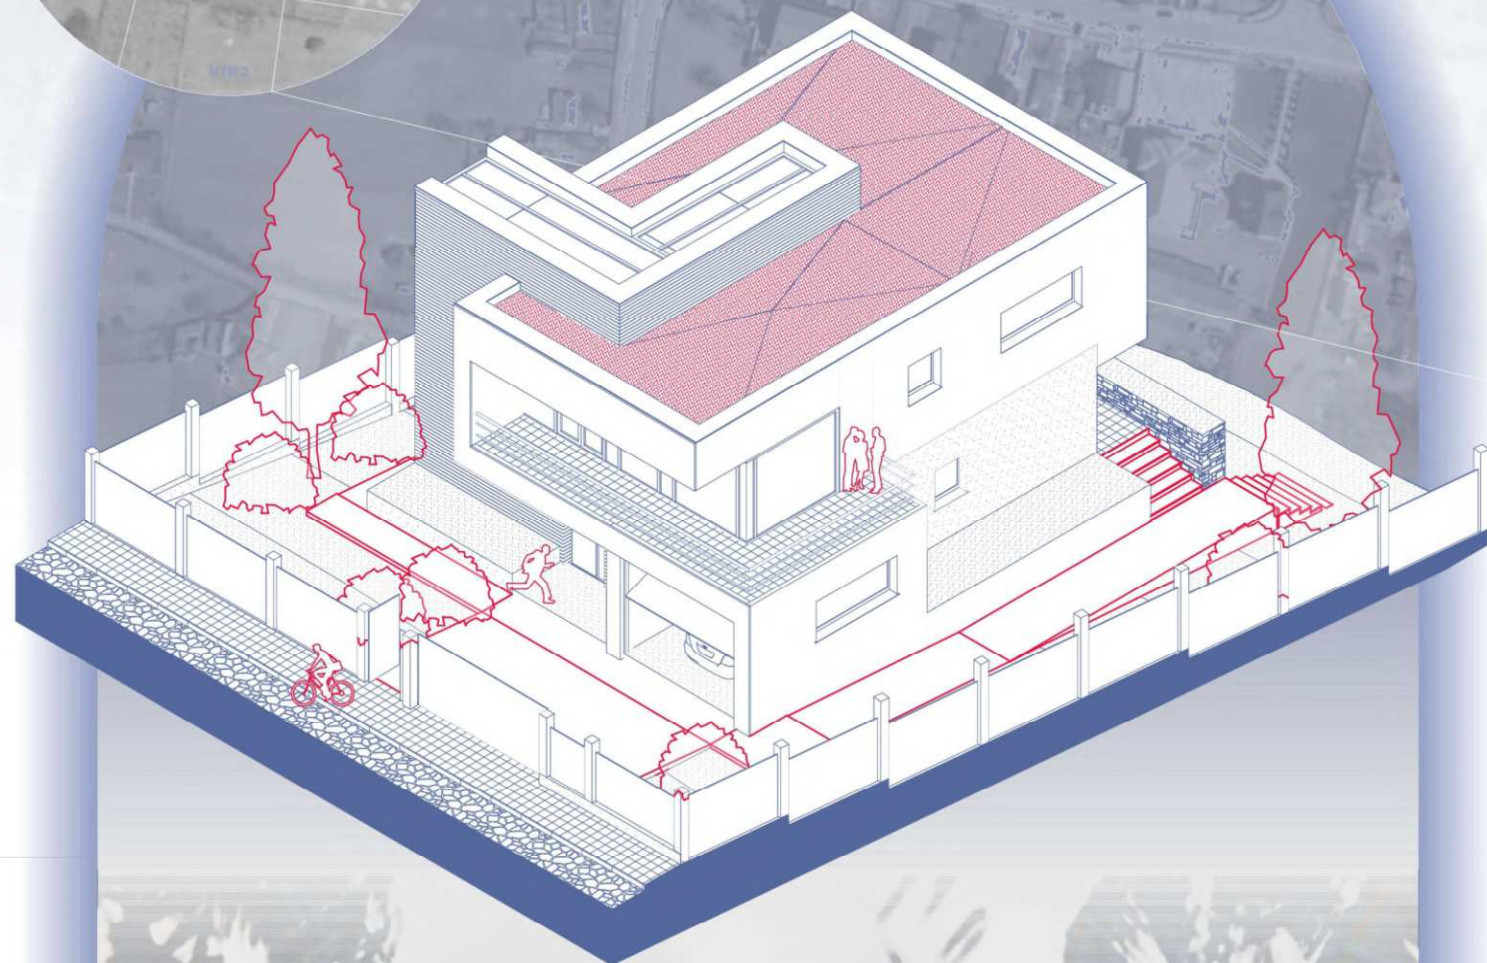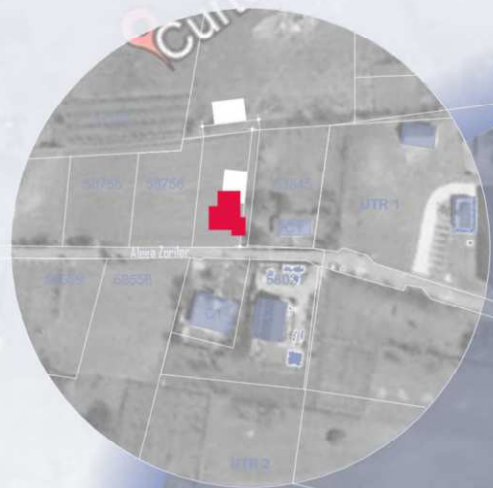

PLAN ETAJ 1:100

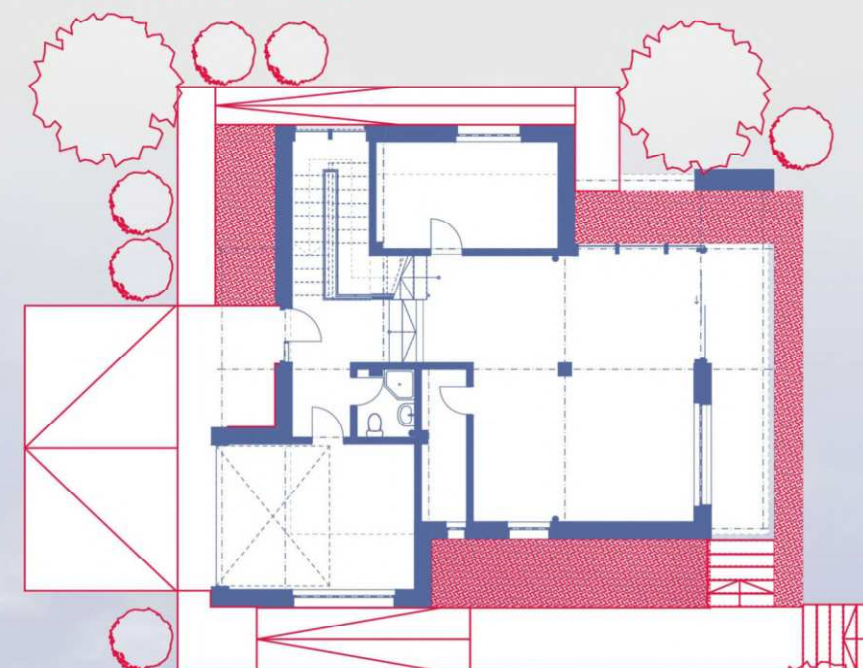

PLAN PARTER 1:100

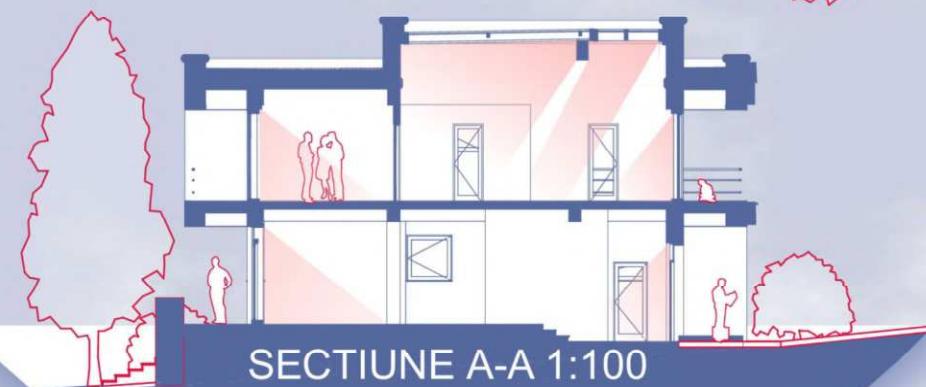


SECTIUNE A-A 1:100




MODUL SCAUN



MODUL BANCA

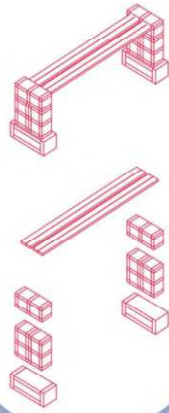





MODUL MASA

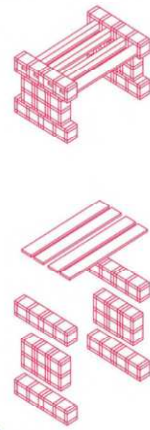


MODUL COS




PARC FONDUL ANTREPRENORILOR LOCALI | IASI

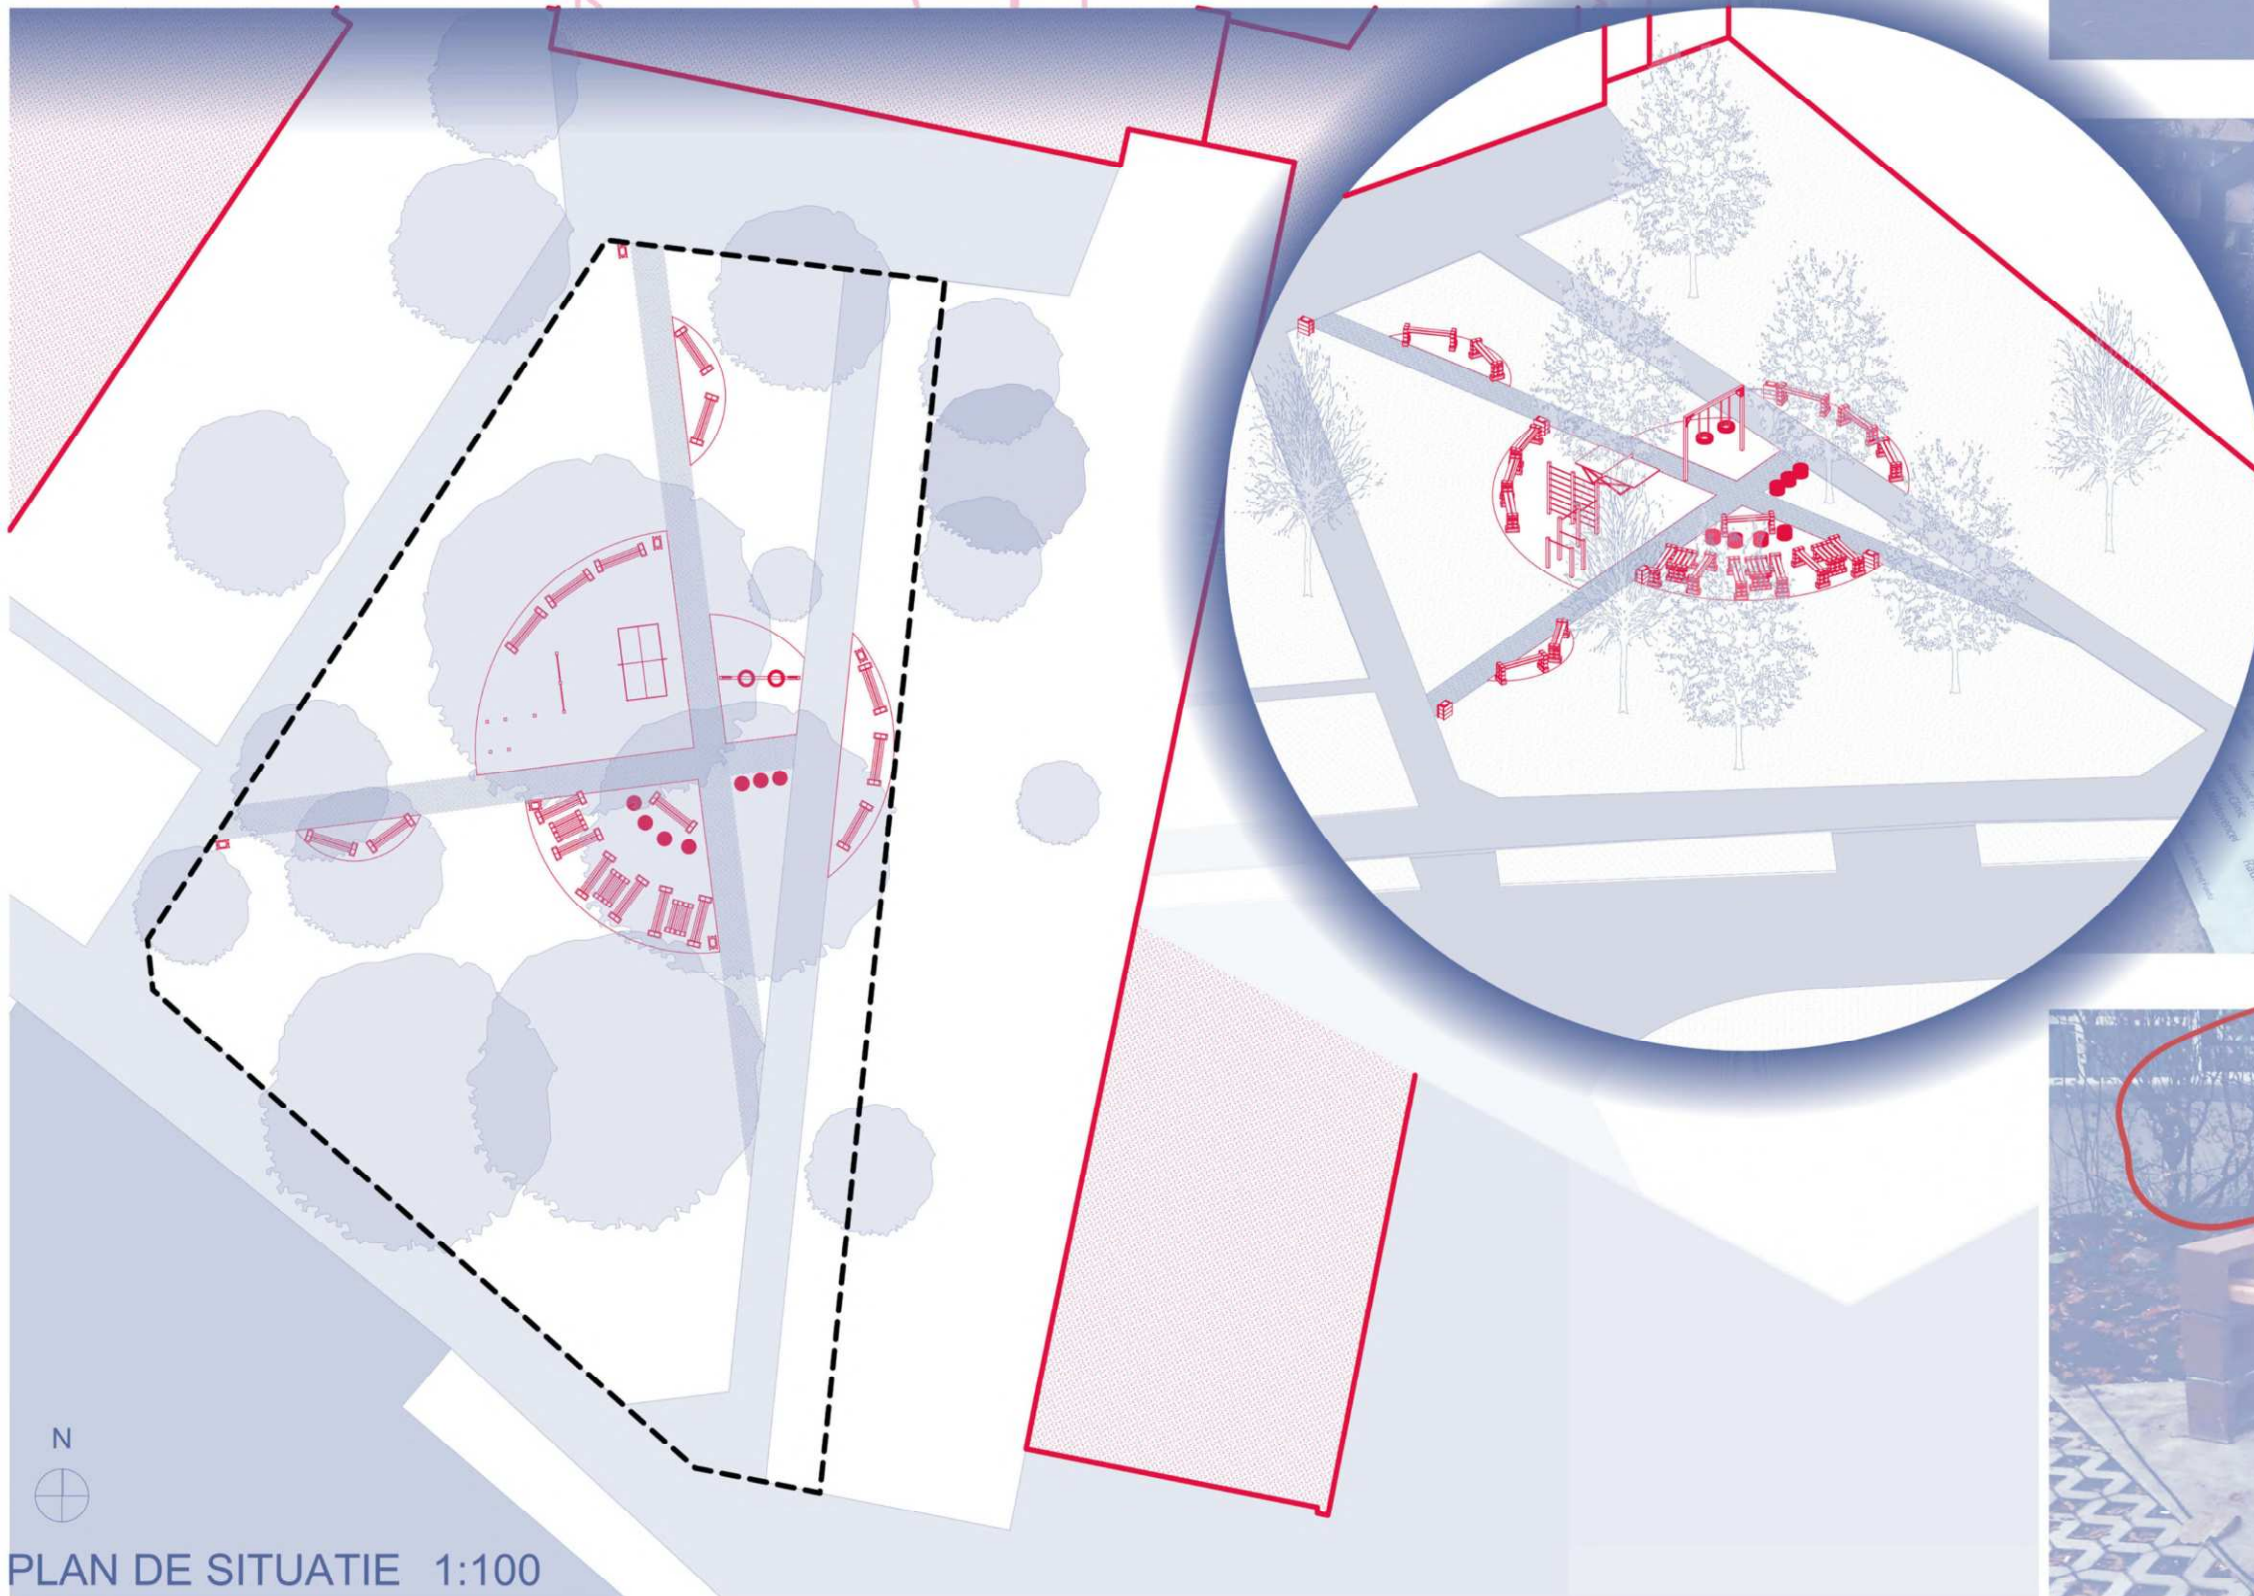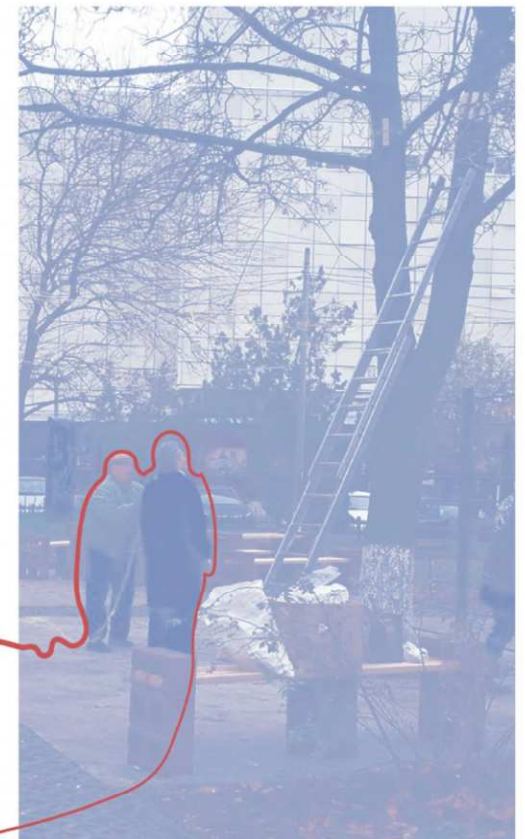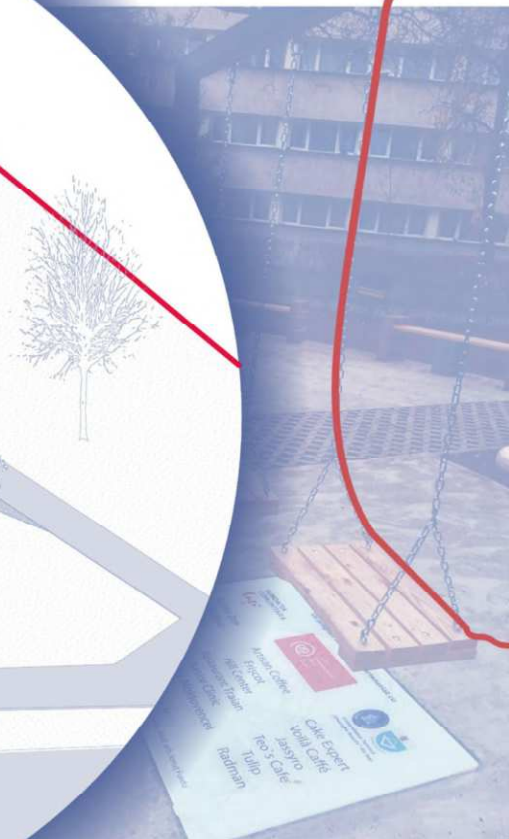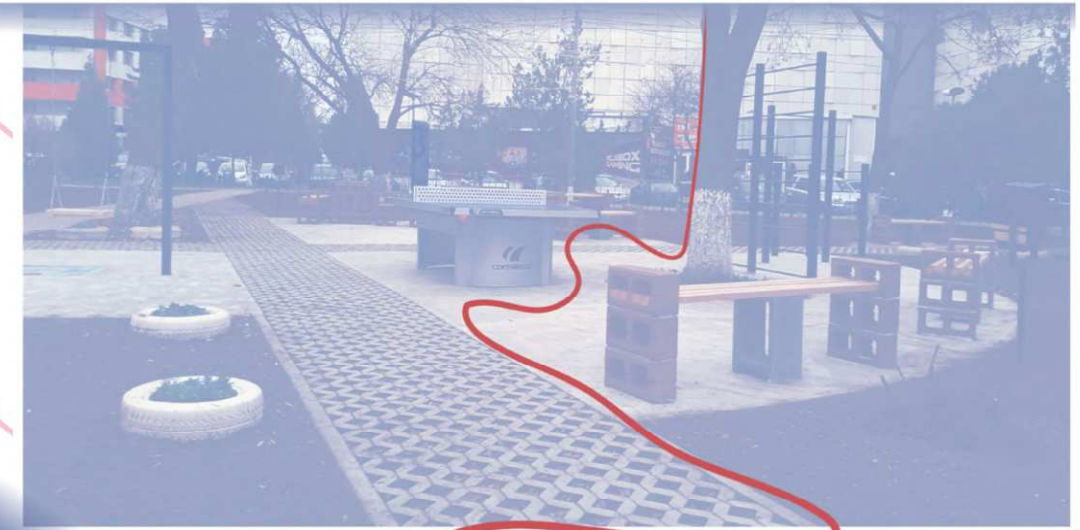


MODUL SCENA

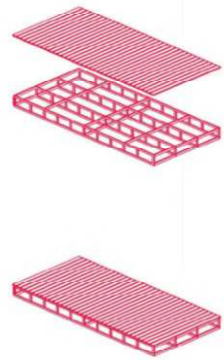





MODUL 1

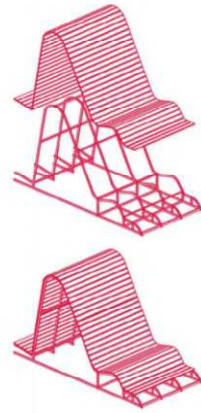

MODUL 2

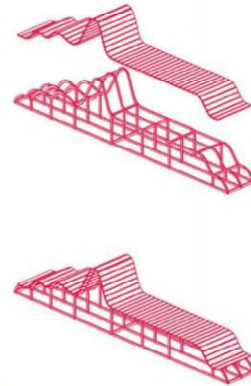

PARC TRANSGOR T10-T11 CAMPUS TUDOR VLADIMIRECU

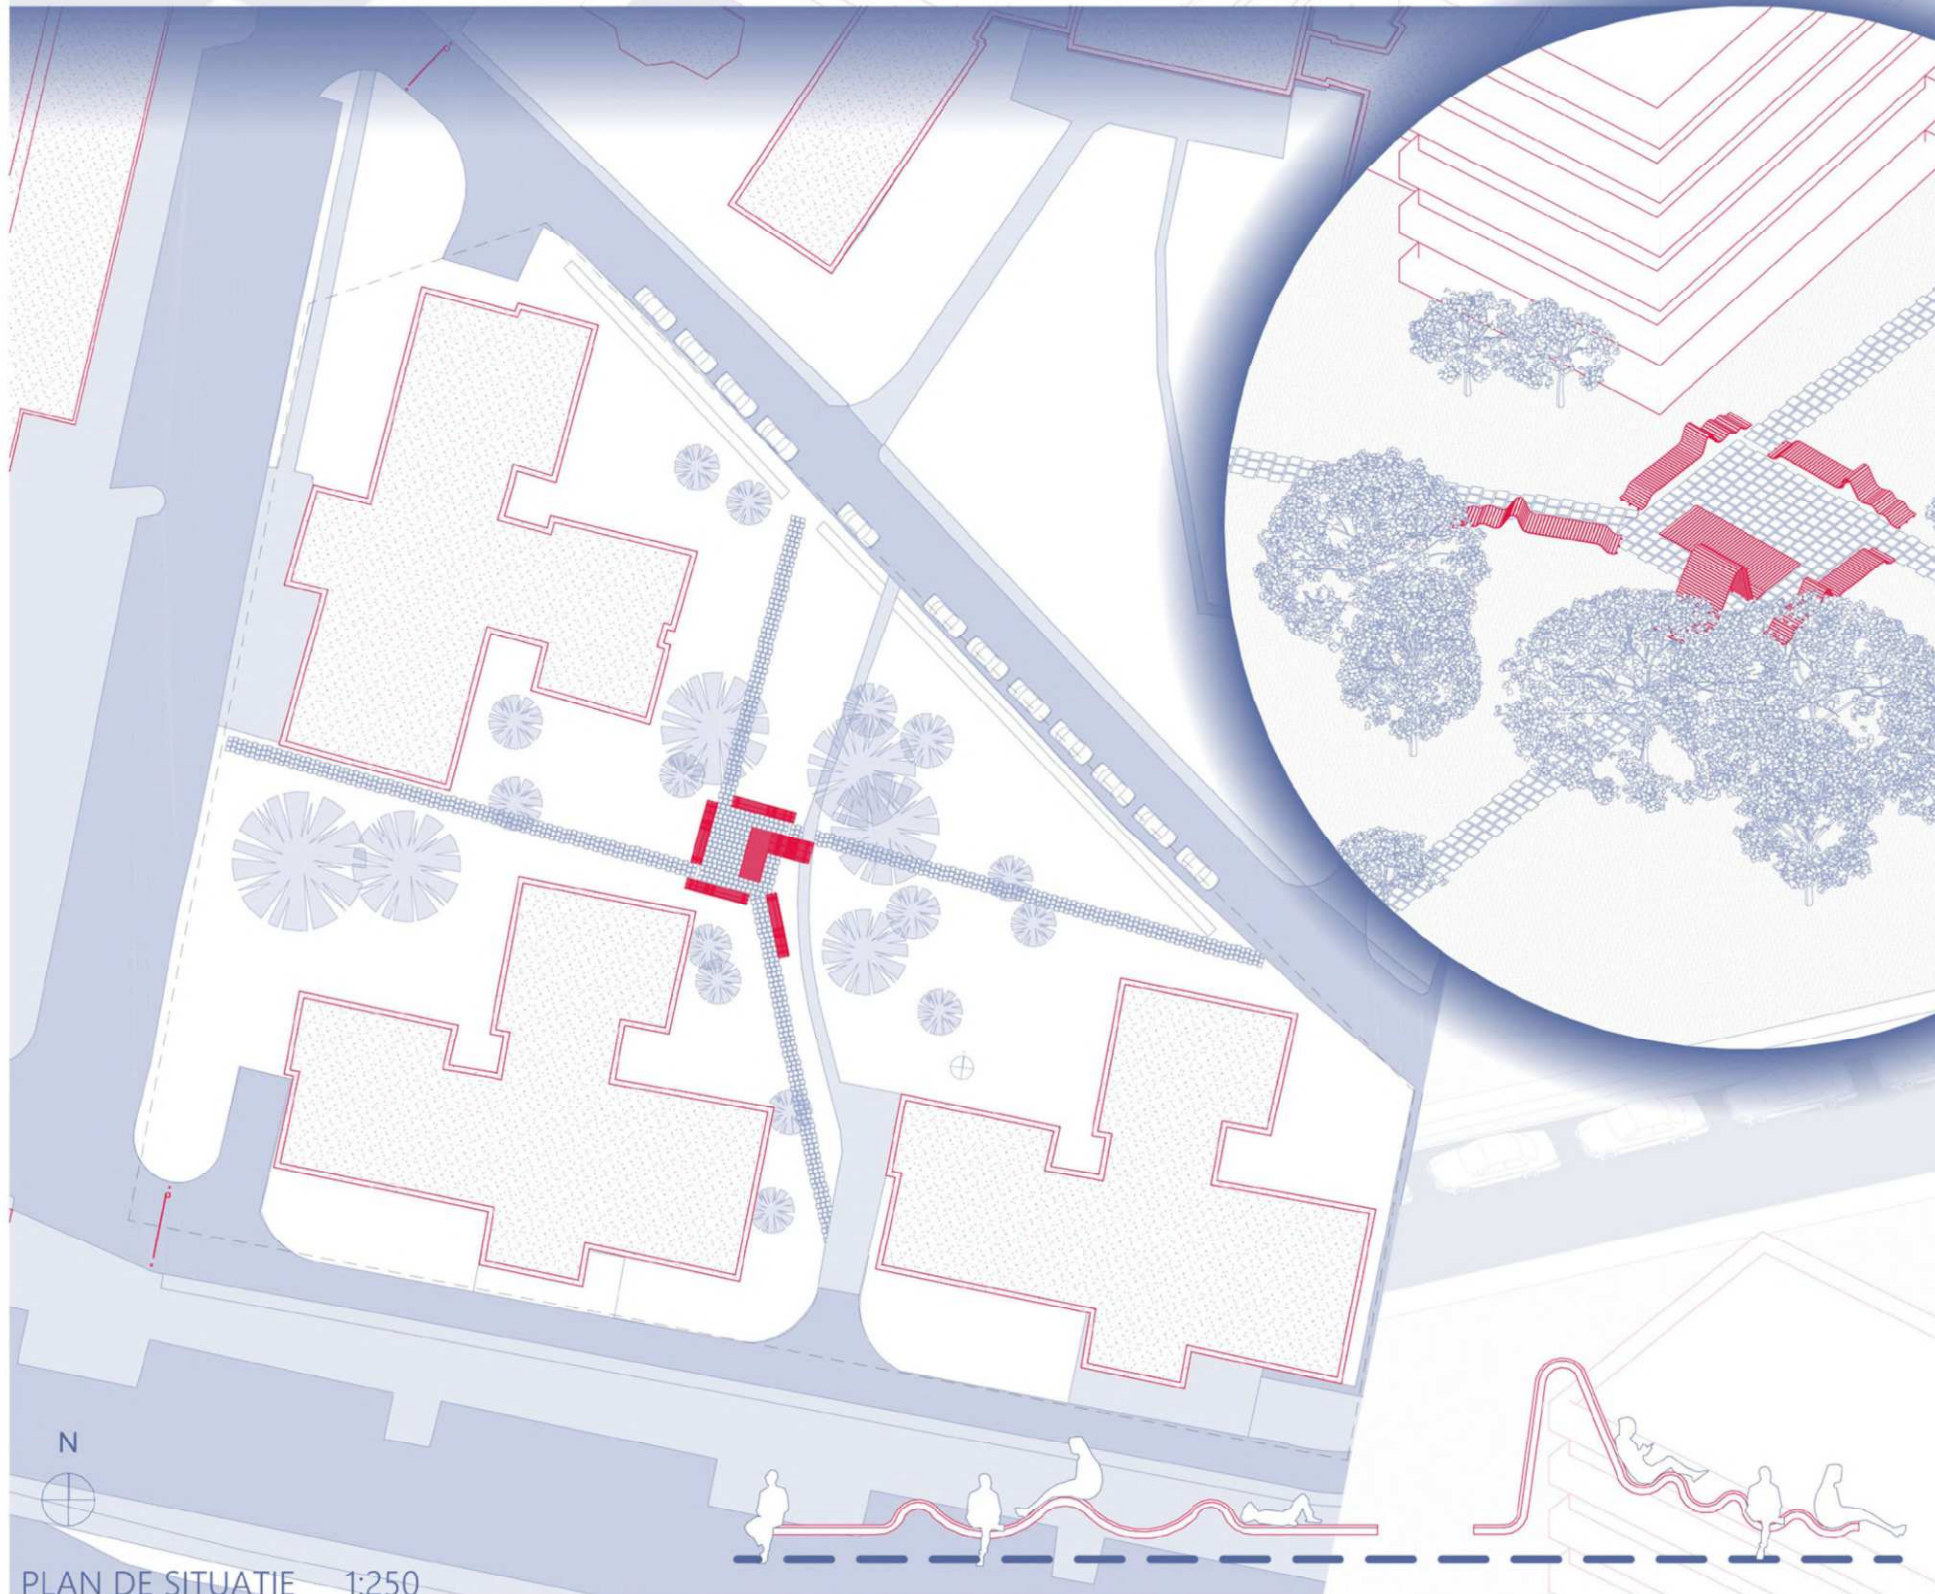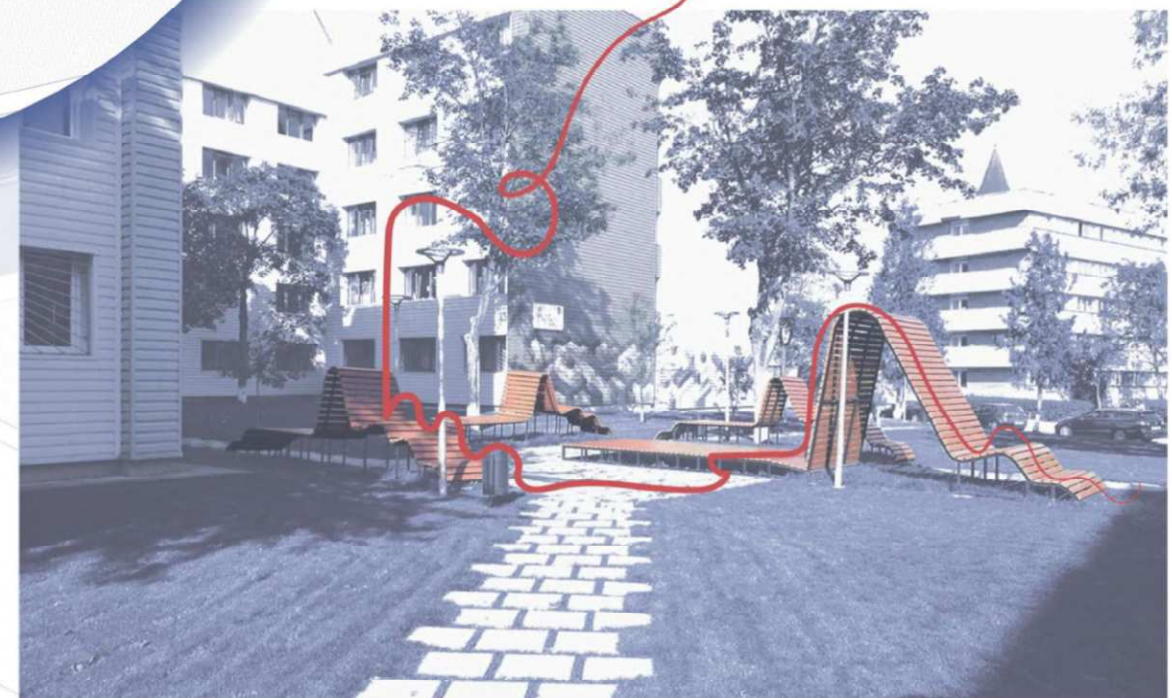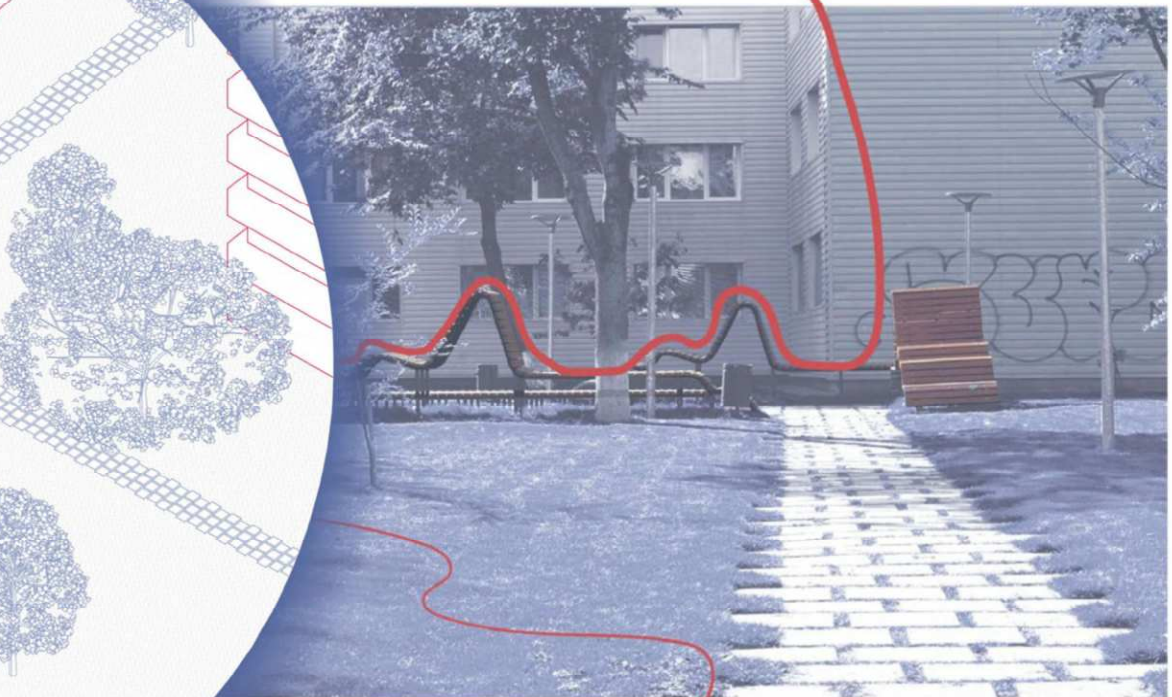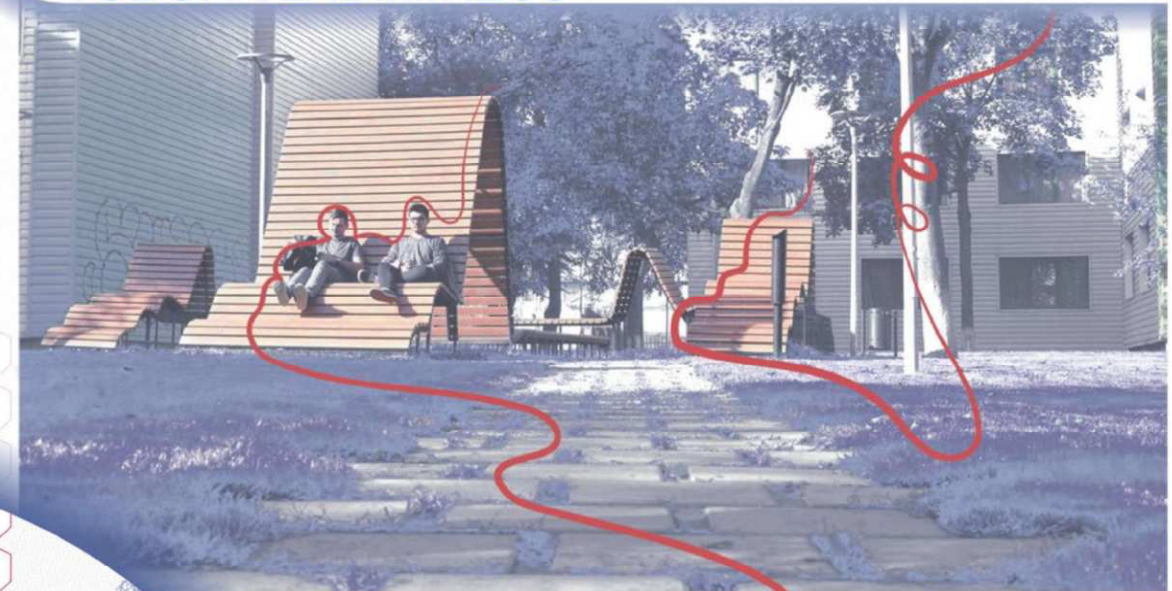

MOBILARE PRIMARIE - OFFICE

